

Товарищество с ограниченной ответственностью «Vitality Group»
ГСЛ №25009593 от 01.04.2025 г.

Рабочий проект

Корректировка рабочего проекта "Реабилитационно-диагностический центр
с гостиницей (Физкультурно-оздоровительный комплекс с гостиницей) город
Астана, район Есиль, ул. Хусейн бен Талал, зд. № 25"

Холодоснабжение

Том – 13

Альбом – 3

(ХС). Блоки 1, 2, 3, 4

г. Астана – 2026 год

Товарищество с ограниченной ответственностью «Vitality Group»
ГСЛ №25009593 от 01.04.2025 г.

Рабочий проект

Корректировка рабочего проекта "Реабилитационно-диагностический центр
с гостиницей (Физкультурно-оздоровительный комплекс с гостиницей) город
Астана, район Есиль, ул. Хусейн бен Талал, зд. № 25"

Холодоснабжение

Том – 13

Альбом – 3

(ХС). Блоки 1, 2, 3, 4

Директор

Бижигитова Б.Ж.

Главный инженер проекта

Галымжанов С.Н.

г.Астана – 2026 год

ОБЩИЕ УКАЗАНИЯ

Проект отопления вентиляции и кондиционирования выполнен на основании:
–задания на проектирование
–СП РК 2.04–01–2017 «Строительная климатология»;
–СН РК 2.04–04–2013 «Строительная теплотехника»;
–СП РК 2.04–107–2013 «Строительная теплотехника»;
–СП РК 4.02–101–2012 «Отопление, вентиляция и кондиционирование воздуха»;
–СН РК 4.02–01–2011 «Отопление, вентиляция и кондиционирование воздуха»
–СП РК 4.02–101–2012* «Отопление, вентиляция и кондиционирование воздуха»
–СН РК 2.04–21–2004* «Энергопотребление и тепловая защита гражданских зданий»;
–СП РК 3.02–108–2013 «Административные и бытовые здания».
–СП 23–101–2000 «Тепловая защита зданий»;
–ГОСТ 30494–96 «Здания жилые и общественные. Параметры микроклимата в помещениях»;
–СП РК 4.02–101–2002 “Проектирование и монтаж трубопроводов систем отопления с использованием металлополимерных труб”;
–СП РК 4.02–108–2014 “Проектирование тепловых пунктов”;
–СН РК 2.01–01–2013 «Защита строительных конструкций от коррозии»
–СП РК 2.01–101–2013 «Защита строительных конструкций от коррозии»
–СП РК2.02–101–2014 «Пожарная безопасность зданий и сооружений»

Расчетные параметры наружного воздуха:
в) летние для проектирования систем кондиционирования воздуха температура (Пар.Б (коэф. обесп. 0.98)) $t_n=+28,6^{\circ}\text{C}$; $W_{от}=4,3\%$; $P_{атм}=977,5\text{гПа}$
Средняя температура отопительного периода $t_{ср.}=-6,3^{\circ}\text{C}$;
Продолжительность отопительного периода 209 суток;
Расчетная скорость ветра в холодный период $-7,2\text{м/с}$
Расчетная скорость ветра в теплый период $3,7\text{м/с}$

Кондиционирование
Проектные решения по кондиционированию приняты с целью обеспечения нормативных параметров микроклимата в помещениях в тёплый период года и межсезонье, в

соответствии с функциональным назначением помещений.
Поддержание комфортных параметров (температуры) внутреннего воздуха в летний период в кабинетах,залах ожидания осуществляется мультизональной сплит системой кондиционирования.
В качестве хладагента применяется фреон марки R410A. Внутренние блоки системы – кассетного типа.
Наружные блоки – инверторные. Производитель Китай компания MCSQUAY.
Фреонопроводы выполнены из медных труб марки EN 12735–1.
Дренажные трубопроводы выполнены из пластиковых труб.

Сброс дренажа в канализацию предусмотреть через гидрозатвор (сифон).
Расчётные параметры наружного воздуха приняты по климатическим данным района строительства – г. Астана в соответствии с действующими нормативами для летнего периода.

Системами кондиционирования воздуха оснащаются помещения с постоянным и периодическим пребыванием людей, а также помещения с повышенными тепловыделениями, в том числе:
• вестибюльные и общественные зоны;
• тренажёрные и спортивные залы;
• залы групповых занятий;
• кабинеты медицинского и оздоровительного назначения;
• административные и офисные помещения;
• гостиничные номера;
• помещения персонала.

Размещение внутренних блоков выполнено: в подвесных потолках;
в технических зонах с возможностью сервисного доступа.
Наружные блоки размещаются на кровле и в технических зонах здания с учётом требований по шуму, вибрации и обслуживанию.

Принятые системы кондиционирования характеризуются:
• высоким коэффициентом энергоэффективности;
• возможностью поэтапного включения оборудования;
• автоматическим поддержанием заданных параметров температуры;
• надёжной и безопасной эксплуатацией.

ОСНОВНЫЕ ПОКАЗАТЕЛИ ПО ЧЕРТЕЖАМ ОТОПЛЕНИЯ И ВЕНТИЛЯЦИИ

Наименование здания (сооружения помещения)	Объем, м3	Периоды года	Расход тепла, Вт(ккал/ч)					Расход холода, Вт	Установленная мощность э/об., кВт
			на отопление	на тепловые завесы	на вентиляцию	на ГВС	общий		
АБК (Терминал)	16488	холодный –31,2	--	--	--	--	--	--	15,73
		теплый +25,5	--	--	--	36460	36460	1185850	

Перечень работ, требующих составления актов освидетельствования скрытых работ

	Наименование	Примечание
1	Промывка системы отопления	
2	Гидравлические испытания системы отопления	
3	Антикоррозионная покраска трубопроводов	
4	Тепловая защита трубопроводов	
5	Проверка на герметичность участков воздуховода скрытых строительными конструкциями методом аэродинамических испытаний	

Ведомость чертежей комплекта

Лист	Наименование	Прим.
1-5	Общие данные	
6	План кондиционирование подвала на отм. –4,050	
7	План кондиционирование 1-го этажа на отм. 0,000	
8	План кондиционирование тех. этажа на отм. +4,200	
9	План кондиционирование 2-го этажа на отм. +7,350	
10	План кондиционирование 3-го этажа на отм. +12,000	
11	План кондиционирование 4-го этажа на отм. +16,800	
12	План кондиционирование 5-го этажа на отм. +21,600	
13	План кондиционирование кровли на отм. +26,640	
14	План кондиционирование подвала на отм. –4,050	
15	План системы дренажа кондиционирование 1-го этажа на отм. 0,000	
16	План системы дренажа кондиционирование тех. этажа на отм. +4,200	
17	План системы дренажа кондиционирование 2-го этажа на отм. +7,350	
18	План системы дренажа кондиционирование 3-го этажа на отм. +12,000	
19	План системы дренажа кондиционирование 4-го этажа на отм. +16,800	
20	План системы дренажа кондиционирование 5-го этажа на отм. +21,600	
21	Схема системы кондиционирования (начало)	
22	Схема системы кондиционирования (окончание)	
23	Схема системы холодоснабжения приточных установок	
24	Индивидуальный холодильный центр. Управление холодоснабжением	

“Настоящий рабочий проект разработан в соответствии с действующими нормами, правилами, инструкциями и государственными стандартами, соответствуют требованиям взрывопожарной и пожарной безопасности и обеспечивают безопасную эксплуатацию запроектированных объектов при соблюдении предусмотренных проектом технических решений (мероприятий) “

Главный инженер проекта

 Галымжанов С.

						02/09/ФОК-ХС						
						Корректировка рабочего проекта "Реабилитационно-диагностический центр с гостиницей (Физкультурно-оздоровительный комплекс с гостиницей) город Астана, район Есиль, ул.Хусейн бен Талал, зд.№ 25"						
Изм.	Кол.	Н док	Лист	Подпись	Дата	Физкультурно-оздоровительный комплекс (блоки 1, 2, 3, 4)	Стадия	Лист	Листов			
ГИП		Галымжанов	С.		02.26		РП	1	24			
Проверил		Галымжанов	С.		02.26							
Разработал		-			02.26							
						Общие данные				ТОО "Vitality Group"		

Инв. № подл.	Подпись и дата	Взам. инв. №

ВЕДОМОСТЬ ССЫЛОЧНЫХ И ПРИЛАГАЕМЫХ ДОКУМЕНТОВ

Обозначение	Наименование	Примечание
	Ссылочные документы	
4.904-69	Детали крепления санитарно-технических приборов и трубопроводов.	
5.904-51	Зонты и дефлекторы вентиляционных систем	
5.903-21	Узлы обвязки регулирующих клапанов на трубопроводах теплоснабжения калориферных установок	
5.904-49	Заслонки воздушные унифицированные различного назначения.	
5.904-4	Двери и люки вентиляционных камер	
5.904-1	Детали креплений воздуховодов	
7.903.9-2	Тепловая изоляция трубопроводов с положительными температурами	
5.904-45	Узлы прохода вентиляционных шахт через покрытия зданий	
5.904-41	Клапаны обратные общего назначения	
	Каталоги	
Каталог фирмы "Арктос"	Воздухораспределители компании Арктос	
Каталог фирмы "VKT (Россия)"	Основной каталог продукции.	
Каталог фирмы "LG"	Основной каталог продукции.	
Каталог фирмы	Трубопроводная система	
Каталог фирмы "K-flex"	Изоляционные материалы.	
Каталог фирмы "TECOFI"	Запорно-регулирующая арматура и	
	Прилагаемые документы	
-ХС.СО	Спецификация оборудования и материалов	37 лист(ов)

ВЕДОМОСТЬ ДОКУМЕНТАЦИИ ПРИ ПРИЕМКЕ ОБЪЕКТА

ОБОЗНАЧЕНИЕ АКТОВ	ОБОСНОВАНИЕ	Необхо- димо (+) нет (-)	ПРИМЕЧ.
1. Акт освидетельствования скрытых работ испытания трубопроводов, воздуховодов при скрытой прокладке в строительных конструкциях	СНиП РК 1.03.06-2002 приложение В.2, приложение Г.	+	
2. Акт гидростатического или манометрического испытания на герметичность системы отопления	СНиП РК 3.05.01-85 раздел 4 приложение 3.	+	
3. Акт промывки системы отопления	СНиП РК 3.05.01-85 прил. 3.10	+	
4. Акт испытания системы отопления на равномерный прогрев отопительных приборов	СНиП РК 3.05.01-85 прил. 4.1	+	

						02/09/ФОК-ХС			
						Корректировка рабочего проекта "Реабилитационно-диагностический центр с гостиницей (Физкультурно-оздоровительный комплекс с гостиницей) город Астана, район Есиль, ул. Хусейн бен Талал, зд. № 25"			
Изм.	Кол.	№ док	Лист	Подпись	Дата	Физкультурно-оздоровительный комплекс (блоки 1, 2, 3, 4)	Стадия	Лист	Листов
ГИП		Галымжанов	С.	Гал	02.26		РП	2	
Проверил		Галымжанов	С.	Гал	02.26				
Разработал					02.26				
						Общие данные	ТОО "Vitality Group"		

ХАРАКТЕРИСТИКА СИСТЕМ КОНДИЦИОНИРОВАНИЯ (НАЧАЛО)

Обозначение системы	кол-во систем	Наименование обслуживаемого помещения (технологического оборудования)	Тип установки	Вентилятор						Электродвигатель				Воздухоохладитель							Компрессор				Место установки	Примечание		
				Тип вентил-лятора	№	Схема исп.	Положение	L, м3/ч	P, Па	n, об/мин	Тип, исп. по Вэры-Возац.	N, кВт	Напряжение	n, об/мин	Тип, тип	Т-ра охлаждения, °C				Расход холода, кВт	dPвс, Па	dPвг, кПа	Тип	Кол.			N, кВт	Напряжение
																Вода		Воздух										
																tв, °C	tк, °C	tв, °C	tк, °C									
K1	1	Подвал	Внутренний кассетный блок	Центробежный (радиальный)	--	--	--	350	--	--	--	0,04	1x220/50	--	MCW200VH	--	--	+25,5	+18	1,3	--	--	--	1	-- (--)	--	--	габ.570х570х260; масса-15.0кг
K1	4	Подвал	Внутренний кассетный блок	Центробежный (радиальный)	--	--	--	800	--	--	--	0,06	1x220/50	--	MCW500VH	--	--	+25,5	+18	3,1	--	--	--	1	-- (--)	--	--	габ.570х570х260; масса-17.0кг
K1	2	Подвал	Внутренний кассетный блок	Центробежный (радиальный)	--	--	--	1200	--	--	--	0,11	1x220/50	--	MCW800VH	--	--	+25,5	+18	5,0	--	--	--	1	-- (--)	--	--	габ.840х840х300; масса-27.0кг
K1	2	Общественные пом. 1-го этажа	Внутренний кассетный блок	Центробежный (радиальный)	--	--	--	350	--	--	--	0,04	1x220/50	--	MCW200VH	--	--	+25,5	+18	1,3	--	--	--	1	-- (--)	--	--	габ.570х570х260; масса-15.0кг
K1	9	Общественные пом. 1-го этажа	Внутренний кассетный блок	Центробежный (радиальный)	--	--	--	450	--	--	--	0,05	1x220/50	--	MCW300VH	--	--	+25,5	+18	1,7	--	--	--	1	-- (--)	--	--	габ.570х570х260; масса-16.0кг
K1	1	Общественные пом. 1-го этажа	Внутренний кассетный блок	Центробежный (радиальный)	--	--	--	650	--	--	--	0,05	1x220/50	--	MCW400VH	--	--	+25,5	+18	2,4	--	--	--	1	-- (--)	--	--	габ.570х570х260; масса-16.0кг
K1	4	Общественные пом. 1-го этажа	Внутренний кассетный блок	Центробежный (радиальный)	--	--	--	800	--	--	--	0,06	1x220/50	--	MCW500VH	--	--	+25,5	+18	3,1	--	--	--	1	-- (--)	--	--	габ.570х570х260; масса-17.0кг
K1	4	Общественные пом. 1-го этажа	Внутренний кассетный блок	Центробежный (радиальный)	--	--	--	950	--	--	--	0,07	1x220/50	--	MCW600VH	--	--	+25,5	+18	3,8	--	--	--	1	-- (--)	--	--	габ.840х840х300; масса-24.0кг
K1	1	Общественные пом. 1-го этажа	Внутренний кассетный блок	Центробежный (радиальный)	--	--	--	1050	--	--	--	0,09	1x220/50	--	MCW700VH	--	--	+25,5	+18	4,0	--	--	--	1	-- (--)	--	--	габ.840х840х300; масса-26.0кг
K1	2	Общественные пом. 1-го этажа	Внутренний кассетный блок	Центробежный (радиальный)	--	--	--	1200	--	--	--	0,11	1x220/50	--	MCW800VH	--	--	+25,5	+18	5,0	--	--	--	1	-- (--)	--	--	габ.840х840х300; масса-27.0кг
K1	1	Общественные пом. 1-го этажа	Внутренний кассетный блок	Центробежный (радиальный)	--	--	--	1900	--	--	--	0,16	1x220/50	--	MCW1200VH	--	--	+25,5	+18	7,1	--	--	--	1	-- (--)	--	--	габ.840х840х300; масса-32.0кг
K1	3	Тех. этаж	Внутренний кассетный блок	Центробежный (радиальный)	--	--	--	1050	--	--	--	0,09	1x220/50	--	MCW700VH	--	--	+25,5	+18	4,0	--	--	--	1	-- (--)	--	--	габ.840х840х300; масса-26.0кг

[illegible]

ХАРАКТЕРИСТИКА СИСТЕМ КОНДИЦИОНИРОВАНИЯ (ПРОДОЛЖЕНИЕ)

Обозначение системы	кол-во систем	Наименование обслуживаемого помещения (технологического оборудования)	Тип установки	Вентилятор						Электродвигатель				Воздухоохладитель							Компрессор				Место установки	Примечание		
				Тип Венти-лятора	№	Схема исп.	Положе-ние	L, м3/ч	P, Па	n, об/мин	Тип, исп. по Взы-востац.	N, кВт	Напряж-ение	n, об/мин	Тип, тип	Т-ра охлаждения, °C				Расход холода, кВт	dPвс, Па	dPвот, кПа	Тип	Кол.			N, кВт	Напряж-ение
																Вода		Воздух										
																tв, °C	tw, °C	tв, °C	tw, °C									
K1	3	Общественные пом. 2-го этажа	Внутренний кассетный блок	Центробежный (радиальный)	--	--	--	450	--	--	--	0.05	1x220/50	--	MCW300VH	--	--	+25,5	+18	1,4	--	--	--	1	-- (--)	--	--	заб.570x570x260; масса-16.0кг
K1	2	Общественные пом. 2-го этажа	Внутренний кассетный блок	Центробежный (радиальный)	--	--	--	650	--	--	--	0,05	1x220/50	--	MCW400VH	--	--	+25,5	+18	2,6	--	--	--	1	-- (--)	--	--	заб.570x570x260; масса-16.0кг
K1	3	Общественные пом. 2-го этажа	Внутренний кассетный блок	Центробежный (радиальный)	--	--	--	800	--	--	--	0,06	1x220/50	--	MCW500VH	--	--	+25,5	+18	3,4	--	--	--	1	-- (--)	--	--	заб.570x570x260; масса-17.0кг
K1	3	Общественные пом. 2-го этажа	Внутренний кассетный блок	Центробежный (радиальный)	--	--	--	950	--	--	--	0,07	1x220/50	--	MCW600VH	--	--	+25,5	+18	3,8	--	--	--	1	-- (--)	--	--	заб.840x840x300; масса-24.0кг
K1	9	Общественные пом. 2-го этажа	Внутренний кассетный блок	Центробежный (радиальный)	--	--	--	1050	--	--	--	0,09	1x220/50	--	MCW700VH	--	--	+25,5	+18	4,4	--	--	--	1	-- (--)	--	--	заб.840x840x300; масса-26.0кг
K1	8	Общественные пом. 2-го этажа	Внутренний кассетный блок	Центробежный (радиальный)	--	--	--	1200	--	--	--	0,11	1x220/50	--	MCW800VH	--	--	+25,5	+18	5,4	--	--	--	1	-- (--)	--	--	заб.840x840x300; масса-27.0кг
K1	1	Общественные пом. 3-го этажа	Внутренний кассетный блок	Центробежный (радиальный)	--	--	--	650	--	--	--	0,05	1x220/50	--	MCW400VH	--	--	+25,5	+18	2,6	--	--	--	1	-- (--)	--	--	заб.570x570x260; масса-16.0кг
K1	13	Общественные пом. 3-го этажа	Внутренний кассетный блок	Центробежный (радиальный)	--	--	--	800	--	--	--	0,06	1x220/50	--	MCW500VH	--	--	+25,5	+18	3,4	--	--	--	1	-- (--)	--	--	заб.570x570x260; масса-17.0кг
K1	8	Общественные пом. 3-го этажа	Внутренний кассетный блок	Центробежный (радиальный)	--	--	--	950	--	--	--	0,07	1x220/50	--	MCW600VH	--	--	+25,5	+18	3,8	--	--	--	1	-- (--)	--	--	заб.840x840x300; масса-24.0кг
K1	8	Общественные пом. 3-го этажа	Внутренний кассетный блок	Центробежный (радиальный)	--	--	--	1050	--	--	--	0,09	1x220/50	--	MCW700VH	--	--	+25,5	+18	4,4	--	--	--	1	-- (--)	--	--	заб.840x840x300; масса-26.0кг
K1	8	Общественные пом. 3-го этажа	Внутренний кассетный блок	Центробежный (радиальный)	--	--	--	1200	--	--	--	0,11	1x220/50	--	MCW800VH	--	--	+25,5	+18	5,4	--	--	--	1	-- (--)	--	--	заб.840x840x300; масса-27.0кг
K1	7	Общественные пом. 3-го этажа	Внутренний кассетный блок	Центробежный (радиальный)	--	--	--	1600	--	--	--	0,13	1x220/50	--	MCW1000VH	--	--	+25,5	+18	6	--	--	--	1	-- (--)	--	--	заб.840x840x300; масса-30.0кг
K1	12	Общественные пом. 3-го этажа	Внутренний кассетный блок	Центробежный (радиальный)	--	--	--	1900	--	--	--	0.16	1x220/50	--	MCW1200VH	--	--	+25,5	+18	7,1	--	--	--	1	-- (--)	--	--	заб.840x840x300; масса-32.0кг


Инв. № подл.	Подпись и дата	Взам. инв. №

						02/09/ФОК-ХС			
						Корректировка рабочего проекта"Реабилитационно-диагностический центр с гостиницей (Физкультурно-оздоровительный комплекс с гостиницей) город Астана, район Есиль,ул.Хусейн бен Талал, зд.№ 25"			
Изм.	Кол.	№ док	Лист	Подпись	Дата	Физкультурно-оздоровительный комплекс (блоки 1, 2, 3, 4)	Стадия	Лист	Листов
ГИП		Галымжанов		С. <i>Галымжанов</i>	02.26		РП	4	
Проверил		Галымжанов		С. <i>Галымжанов</i>	02.26				
Разработал		-			02.26				
						Общие данные	ТОО "Vitality Group"		

ХАРАКТЕРИСТИКА СИСТЕМ КОНДИЦИОНИРОВАНИЯ (ОКОНЧАНИЕ)


Обозначение системы	Код по системе	Наименование обслуживаемого помещения (технологического оборудования)	Тип установки	Вентилятор						Электродвигатель				Воздухоохладитель								Компрессор				Место установки	Примечание				
				Тип Вентилятора	№	Схема исп.	Положение	L, м3/ч	P, Па	n, об/мин	Тип, исп. по взры-возап.	N, кВт	Напряжение	n, об/мин	Тип, тип	Т-ра охлаждения, °C				Расход холода, кВт	dPвс, Па	dPвот, кПа	Тип	Кол.	N, кВт			Напряжение			
																Вода		Воздух													
																tв, °C	tx, °C	tв, °C	tx, °C												
K1	1	Общественные пом. 4-го этажа	Внутренний кассетный блок	Центробежный (радиальный)	--	--	--	450	--	--	--	0.05	1x220/50	--	MCW300VH	--	--	+25,5	+18	1,4	--	--	--	1	-- (--)	--	--	габ.570х570х260; масса-16.0кг			
K1	1	Общественные пом. 4-го этажа	Внутренний кассетный блок	Центробежный (радиальный)	--	--	--	650	--	--	--	0.05	1x220/50	--	MCW400VH	--	--	+25,5	+18	2,4	--	--	--	1	-- (--)	--	--	габ.570х570х260; масса-16.0кг			
K1	13	Общественные пом. 4-го этажа	Внутренний кассетный блок	Центробежный (радиальный)	--	--	--	800	--	--	--	0.06	1x220/50	--	MCW500VH	--	--	+25,5	+18	3,4	--	--	--	1	-- (--)	--	--	габ.570х570х260; масса-17.0кг			
K1	10	Общественные пом. 4-го этажа	Внутренний кассетный блок	Центробежный (радиальный)	--	--	--	950	--	--	--	0.07	1x220/50	--	MCW600VH	--	--	+25,5	+18	3,8	--	--	--	1	-- (--)	--	--	габ.840х840х300; масса-24.0кг			
K1	6	Общественные пом. 4-го этажа	Внутренний кассетный блок	Центробежный (радиальный)	--	--	--	1050	--	--	--	0.09	1x220/50	--	MCW700VH	--	--	+25,5	+18	4,4	--	--	--	1	-- (--)	--	--	габ.840х840х300; масса-26.0кг			
K1	4	Общественные пом. 4-го этажа	Внутренний кассетный блок	Центробежный (радиальный)	--	--	--	1200	--	--	--	0.11	1x220/50	--	MCW800VH	--	--	+25,5	+18	5,4	--	--	--	1	-- (--)	--	--	габ.840х840х300; масса-27.0кг			
K1	1	Общественные пом. 4-го этажа	Внутренний кассетный блок	Центробежный (радиальный)	--	--	--	1900	--	--	--	0.16	1x220/50	--	MCW1200VH	--	--	+25,5	+18	7,2	--	--	--	1	-- (--)	--	--	габ.840х840х300; масса-32.0кг			
K1	20	Общественные пом. 5-го этажа	Внутренний кассетный блок	Центробежный (радиальный)	--	--	--	1600	--	--	--	0.13	1x220/50	--	MCW1000VH	--	--	+25,5	+18	6.0	--	--	--	1	-- (--)	--	--	габ.840х840х300; масса-30.0кг			
K1	20	Общественные пом. 5-го этажа	Внутренний кассетный блок	Центробежный (радиальный)	--	--	--	650	--	--	--	0.05	1x220/50	--	MCW400VH	--	--	+25,5	+18	2.6	--	--	--	1	-- (--)	--	--	габ.570х570х260; масса-16.0кг			
K1	20	Общественные пом. 5-го этажа	Внутренний кассетный блок	Центробежный (радиальный)	--	--	--	800	--	--	--	0.06	1x220/50	--	MCW500VH	--	--	+25,5	+18	3.3	--	--	--	1	-- (--)	--	--	габ.570х570х260; масса-17.0кг			
K1	20	Общественные пом. 5-го этажа	Внутренний кассетный блок	Центробежный (радиальный)	--	--	--	1200	--	--	--	0.11	1x220/50	--	MCW800VH	--	--	+25,5	+18	5.6	--	--	--	1	-- (--)	--	--	габ.840х840х300; масса-27.0кг			
K1	20	Общественные пом. 5-го этажа	Внутренний кассетный блок	Центробежный (радиальный)	--	--	--	1050	--	--	--	0.09	1x220/50	--	MCW700VH	--	--	+25,5	+18	4.2	--	--	--	1	-- (--)	--	--	габ.840х840х300; масса-26.0кг			
K1	20	Общественные пом. 5-го этажа	Внутренний кассетный блок	Центробежный (радиальный)	--	--	--	1900	--	--	--	0.12	1x220/50	--	MCW1200VH	--	--	+25,5	+18	7.0	--	--	--	1	-- (--)	--	--	габ.840х840х300; масса-32.0кг			
K1	20	Общественные пом. 5-го этажа	Внутренний кассетный блок	Центробежный (радиальный)	--	--	--	950	--	--	--	0.07	1x220/50	--	MCW600VH	--	--	+25,5	+18	3.8	--	--	--	1	-- (--)	--	--	габ.840х840х300; масса-24.0кг			
																						02/09/ФОР-ХС									
																						Корректировка рабочего проекта "Реабилитационно-диагностический центр с гостиницей (Физкультурно-оздоровительный комплекс с гостиницей) город Астана, район Есиль, ул.Хусейн бен Талал, зд.№ 25"									
															Изм.	Кол.	N док	Лист	Подпись	Дата	Физкультурно-оздоровительный комплекс (блоки 1, 2, 3, 4)					Стадия	Лист	Листов			
															ГИП		Галымжанов		С. <i>Гал</i>	02.26											
															Проверил		Галымжанов		С. <i>Гал</i>	02.26											
															Разработал					02.26	Общие данные					ТОО "Vitality Group"					

План кондиционирование подвала на отм. -4,050

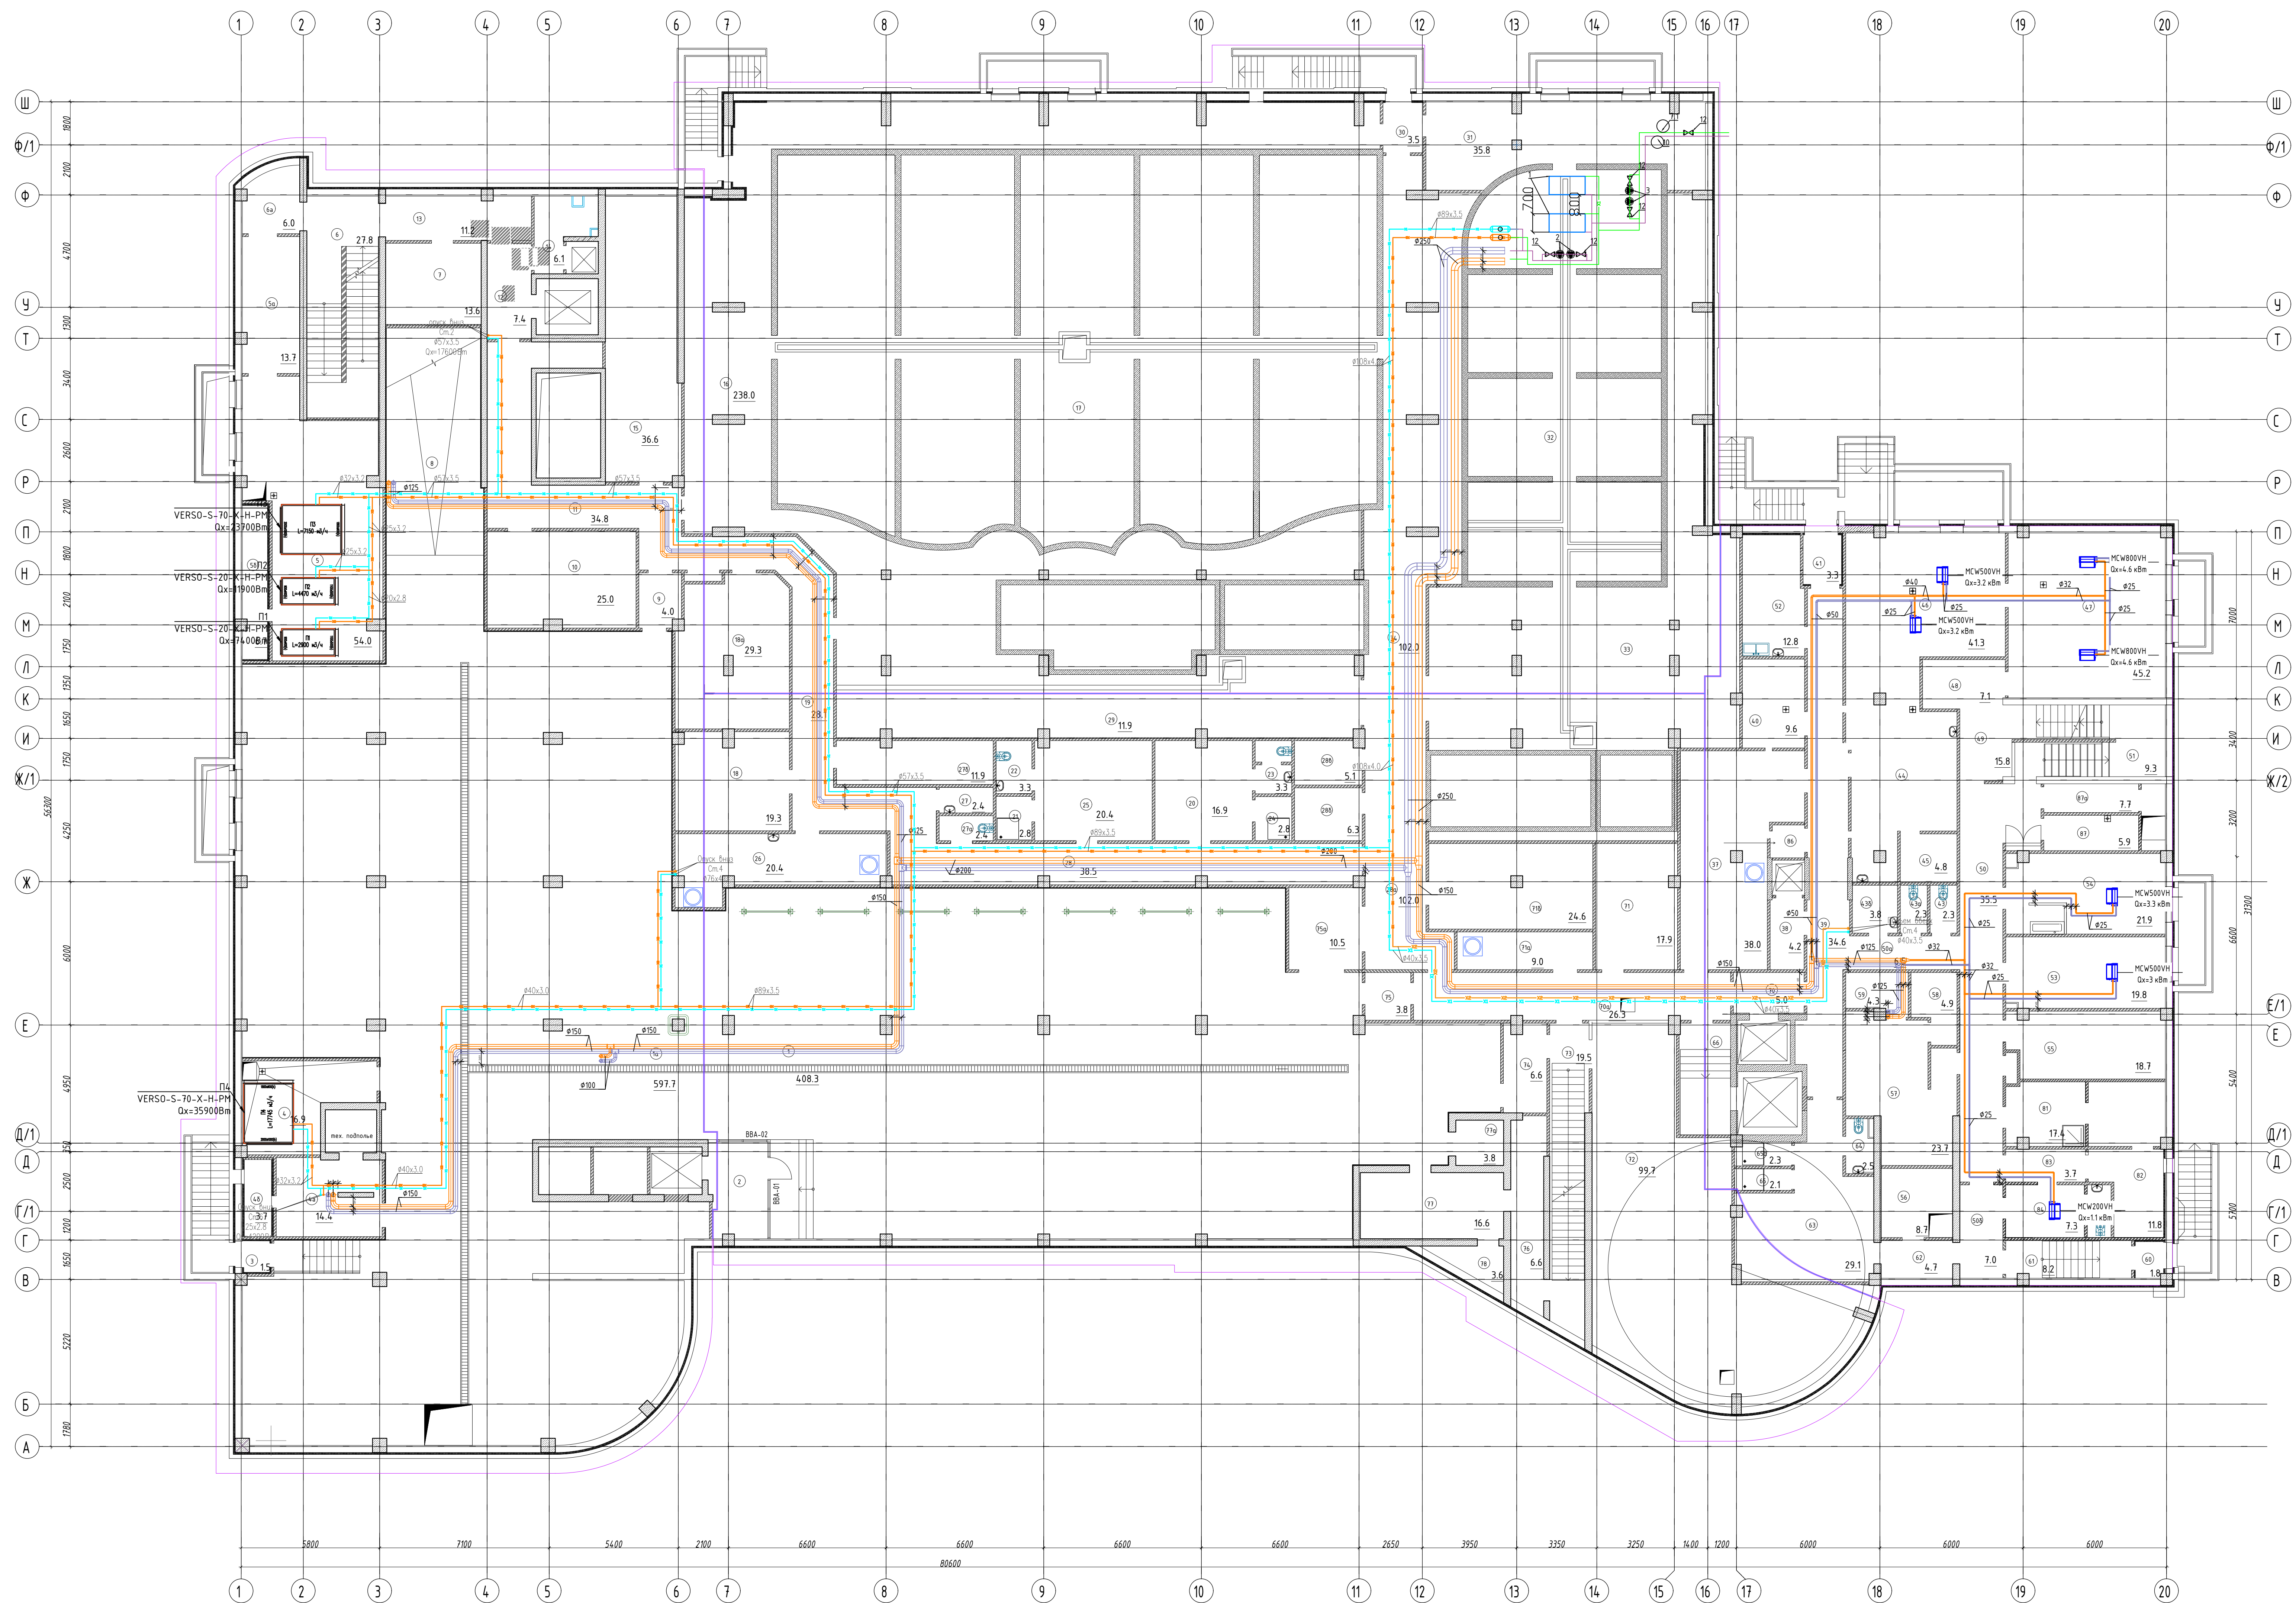


Экспликация помещений (начало)			Экспликация помещений (конец)		
Поз.	Наименование	Площадь, кв. м	Поз.	Наименование	Площадь, кв. м
1	Парикмах.	408,3	44	Пом. приема и разбора грязного белья	26,3
1а	Парикмах.	597,7	45	Пом. уборочного инвентаря	4,8
2	Тамбур с подпором воздуха	9,7	46	Помещение пастеризатор	41,3
3	Тамбур	15	47	Гладильная	45,2
4	Тех. помещение	16,9	48	Помещ.-ч. разбрызг. упаковки чистого белья	7,1
4а	Вешалка	3,7	49	Выбор чистого белья	15,8
4б	Вешалка	3,9	50	Коридор	35,5
4в	Вешалка	14,4	50а	Коридор	6,5
5	Вешалка	54,0	50б	Коридор	7,0
5а	Тех. помещение	6,7	51	Лестничная клетка	9,3
5б	Вешалка	13,7	52	Холод. камера хранения мед. отходов	12,9
6	Лестничная клетка	27,8	53	Комн. отдыха и приема пищи	21,9
6а	Коридор	6,0	54	Ночная смена	19,8
7	Кладовая	136	55	Кладовая запасов чистого (разобранного) белья	18,7
8	Ванна	50,9	56	Кладовая верхней одежды медперсонала	8,7
9	Тамбур с подпором воздуха	4,0	57	Раздевальня медперсонала (Мужской)	23,7
10	Гардероб	25,0	58	Душевая	4,9
11	Коридор	34,8	59	Санузлы	4,3
12	Тамбур с подпором воздуха	7,4	60	Тамбур	1,8
13	Коридор	11,2	61	Лестница	8,2
14	Застекленная	61,6	62	Коридор	4,7
15	Архив	36,6	63	Раздевальня медперсонала (Женский)	29,1
16	Тех. подполье	238,0	64	Санузлы	2,5
17	Тех. подполье	378,5	65	Душевая	2,1
18	Кладовая	19,3	65а	Душевая	2,3
18а	Электрокотельная	29,3	66	Лифтовый холл	10,0
19	Коридор	28,1	70	Тамбур с подпором	5,0
20	Гардеробная	26,9	70а	Коридор	17,9
21	Душевая	1,1	71	Насосная АПТ	26,3
22	Санузел	3,3	72	Пом. сбора грязного белья	9,0
23	Санузел	3,3	73	Насосная АПТ	24,6
24	Душевая	2,8	74	Насосная, тепловая узел	99,7
25	Гардеробная	20,4	75	Лестничная клетка	19,5
26	Пом. сбора грязного белья	20,4	76	Тамбур с подпором воздуха	6,6
27	Пом. уборочного инвентаря	2,4	75а	Тамбур с подпором воздуха	3,8
27а	Санузел	2,4	76а	Тех. подполье	6,6
27б	Гардеробная	11,9	77	Тех. подполье	16,6
28	Коридор	38,5	78	Тех. подполье	3,6
28а	Коридор	102,0	78а	Тех. подполье	17,6
28б	Хранение реагентов	6,3	81	Пом. приема и дезинфекции и стерилизации	31,4
28с	Хранение реагентов	6,3	82	Пом. хранения мед.инвент.	11,8
29	Узел управления бассейном	1,1	83	Санузел. Душевая	3,7
30	Тамбур	3,5	84	Охрана	7,3
31	Техническое помещение	35,8	85	Помещение хранения материалов	5,9
32	Техническое помещение	109,1	87	Пом. стерилизации и хранения мед.инвент.	7,9
33	Узел управления бассейном	10,7	87а	Помещение выдачи чистого белья (депозит)	7,7
34	Коридор	102,0			
37	Пом. временного хранения грязного белья	38,0			
38	Тамбур с подпором	4,2			
39	Коридор	34,6			
40	Холод. камера хранения ТБО	9,6			
41	Тамбур	3,3			
43	Санузел	2,3			
43а	Санузел	2,3			
43б	Комната убороч. инвентаря	3,8			

СХЕМА БЛОКИРОВКИ

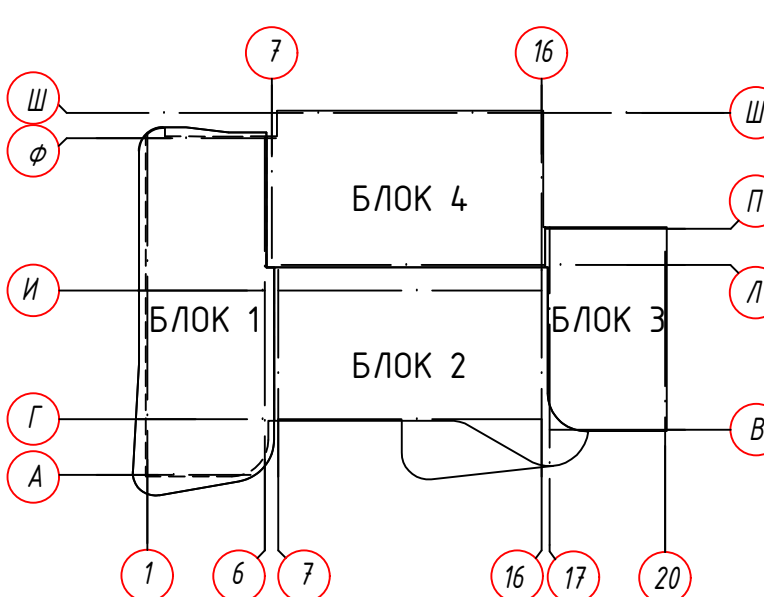


										02/09/ФСК-ХС
										Корректировка рабочего проекта "Реабилитационно-диагностический центр с госпиталью (физкультурно-оздоровительный комплекс с госпитальной оферой Алтай, район Есилен, Хакасия, село Талая, №М 25" Физкультурно-оздоровительный комплекс (Вложения 1, 2, 3, 4)
Имя	Кол.	№ документа	Листы	Подпись	Дата					
ГПМ	Галикина	С	2	<i>Сидорова</i>	02.09.26					
Проектировщик				<i>Сидорова</i>	02.09.26					
Разработчик					02.09.26					
										План кондиционирование подвала на опт. -4,950 100 "Utility Unit"

План кондиционирование 1-го этажа на отм. 0,000

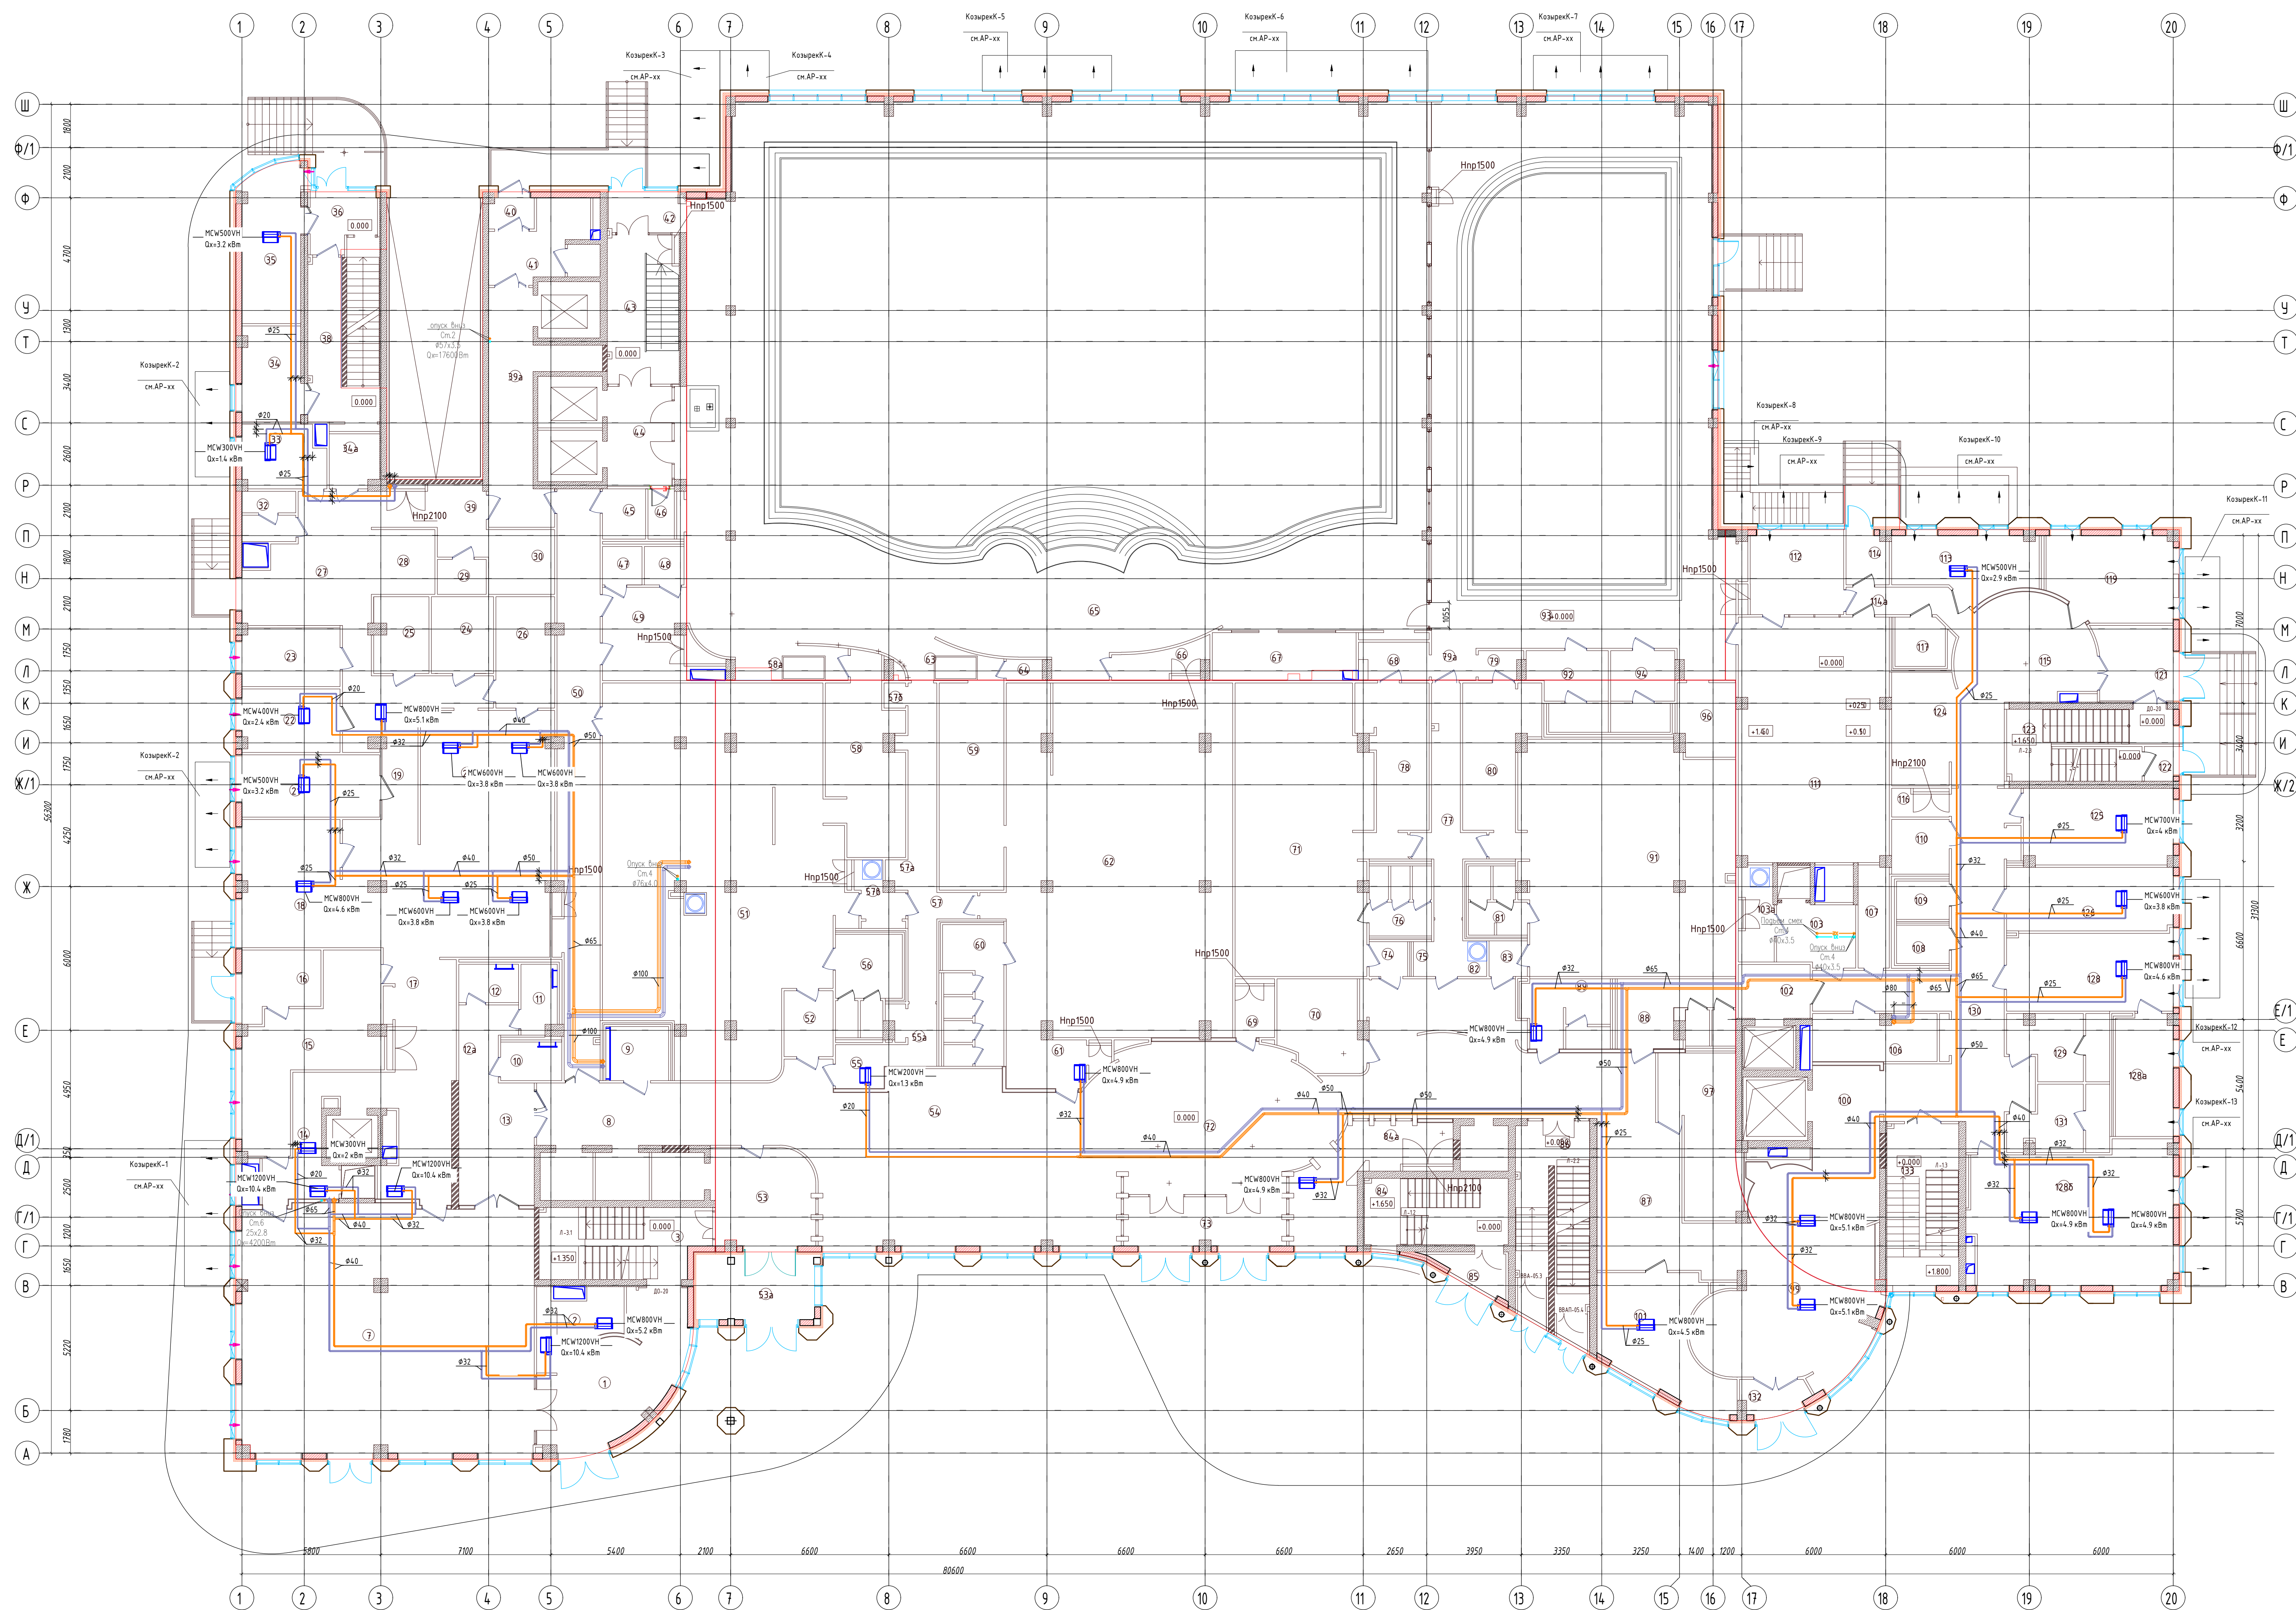


Экспликация помещений (начало)			Экспликация помещений (окончание)		
Поз	Наименование	Площадь	Поз	Наименование	Площадь
1	Ресепشن	26,0	60	Санузел	15,1
2	Гардероб	20,3	61	Тамбур	12,5
3	Лестница	89,3	61а	Поблизкое помещение	7,5
7	Обеденный зал	129,2	62	Раздевалка женская	141,4
8	Холл	18,8	63	Тамбур	3,9
9	Санузел МГН	5,9	64	Тех.помещение	15,5
10	Санузел	4,10	65	Воссеин	694,3
11	Санузел	4,2	66	Тех.помещение	5,0
12	Санузел	4,0	67	Бани Франская	9,3
12а	Тамбур	6,8	68	Тамбур	4,4
13	Холл	16,1	69	Поблизкое помещение	4,0
14	Коридор	28,0	70	Охрана	12,7
15	Менская столовая посуды	9,9	71	Раздевалка фоб	68,9
16	Тамбур	8,9	72	Холл	195,9
17	Раздевалочная	31,7	73	Тамбур	15,0
18	Холодный цех	22,8	74	Тамбур	2,2
19	Коридор	20,6	75	КВИ	1,4
20	Горячий цех	74,6	76	Санузел	7,3
21	Мясной цех	15,5	77	Тех.помещение	12,1
22	Рыбный цех	11,1	78	Душевые	25,6
23	Кладовая	10,4	79а	Тамбур	2,5
24	Общайной цех	8,2	80	Душевые	16,5
25	Кладовая общедо	7,1	81	Санузел	6,7
26	Менская кухонной посуды	16,1	82	Пом. бельепродажа	4,1
27	Зероузелная	11,2	83	Тамбур	2,4
28	Холодильная камера	7,2	84	Лестница	16,6
29	Кладовая	3,0	84а	Отдел продаж	19,1
30	Холодильная камера	7,5	85	Тамбур	19,1
32	Санузел	4,6	86	Лестница	21,1
33	Зав. производством	9,2	87	Коридор	21,5
34	Гардероб персонала	9,9	88	Санузел женский	13,4
34а	Кладовая	4,6	89	Санузел мужской	10,2
35	Помещение охраны	16,0	91	Раздевалка для мальчиков	87,0
36	Тамбур	6,3	92	Тренерская жен.	9,7
38	Лестница	20,1	93	Воссеин детский	275,4
39	Коридор	6,9	94	Тренерская муж.	8,7
39а	Коридор	23,1	96	Бани Франская	7,3
40	Тамбур	2,4	97	Гардероб	19,0
41	Зероузелная	12,2	99	Холл	16,8
42	Тамбур	5,5	100	Вестебиль	50,2
43	Лестница	18,6	101	Отдел продаж	22,5
44	Лифтовой холл	11,3	102	Лифтовой холл	6,8
45	Лазаретная	3,8	103	КВИ	8,4
46	КВИ	2,3	103а	Бельепродаж	5,9
47	Санузел	2,6	106	Помещение специализации мед.инвентаря и препаратов, вывоза/возврата	10,1
48	Санузел	2,6	107	Тех.помещение	5,5
49	Фитбол	15,4	108	Санузел	3,5
50	Коридор	4,29	109	Санузел	3,5
51	Раздевалка мужская	145,0	110	Санузел МГН	5,5
52	Тамбур	5,6	111	Воссеин	64,1
53	VIP вход	17,5	112	Раздевалка для грудничков	13,0
53а	Тамбур	13,5	113	Кабинет врача остеопата	14,6
54	Вор	12,7	114	Тамбур	19,9
55	Коридор	5,5	114а	Тамбур	12,5
55а	КВИ	2,8	115	Холл	22,5
56	Санузел	10,5	116	КВИ	2,9
57	Коридор	15,2	117	Кабинета матери и ребенка	4,2
57а	КВИ	1,0	119	Пом.грудничкового массажа и гимнастики	18,9
57б	КВИ	0,9	121	Тамбур	10,6
57б	Пом. Бельепродажа	4,3	122	Тамбур	2,2
58	Душевые	20,2	123	Лестница	86,6
58а	Тамбур	16,1	124	Гардероб	19,9
59	Душевые	23,4	125	Кабинет врача остеопата	20,2
			126	Кабинет врача переломов	18,7
			128	Кабинет врача хиропрактики/Реабилитолога	23,1
			128а	Помещение массажа	23,1
			128б	Помещение электро-физиотерапии	48,9
			129	Раздб. Мужская с душевой	10,3
			130	Коридор	55,3
			131	Раздб. Женская с душевой	10,1
			132	Тамбур	4,4
			133	Лестница	20,7

СХЕМА БЛОКИРОВКИ

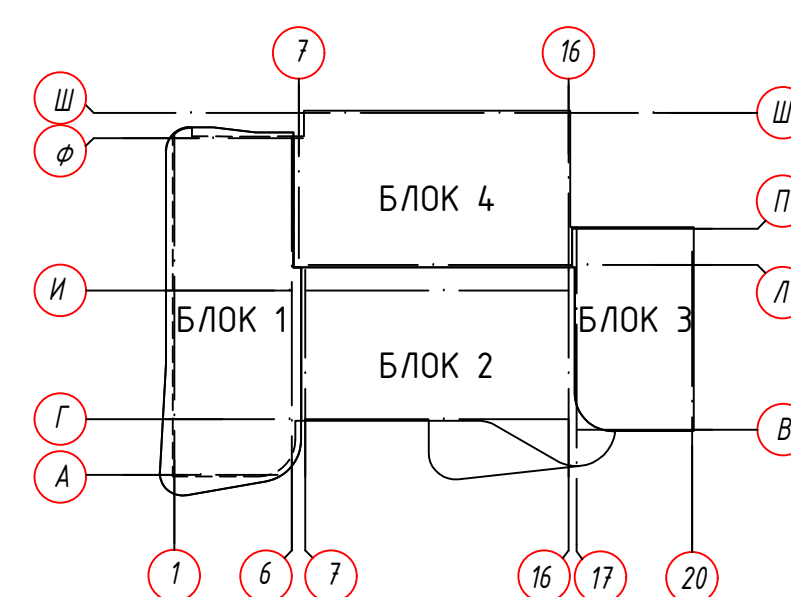


						02/09/ФСК-ХС	
						Корректировка рабочего проекта "Реабилитационно-диагностический центр с гостиницей (Физкультурно-оздоровительный комплекс с гостиницей) города Астана, район Селькуп-Хуцун в кв. Талла, д. № 25"	
ИП	Кол.	Н док	Лист	Подпись	Дата	Физкультурно-оздоровительный комплекс	
Гиз	Галимжанов			<i>Г. Галимжанов</i>	02.06	Этап	Листов
Проверил					02.06	РП	7
Разработал					02.06		•
						План кондиционирования 1-го этажа на о.т.м. 0,000	
						100 "Vinylit Group"	

План кондиционирование тех. этажа на отм. +4.200

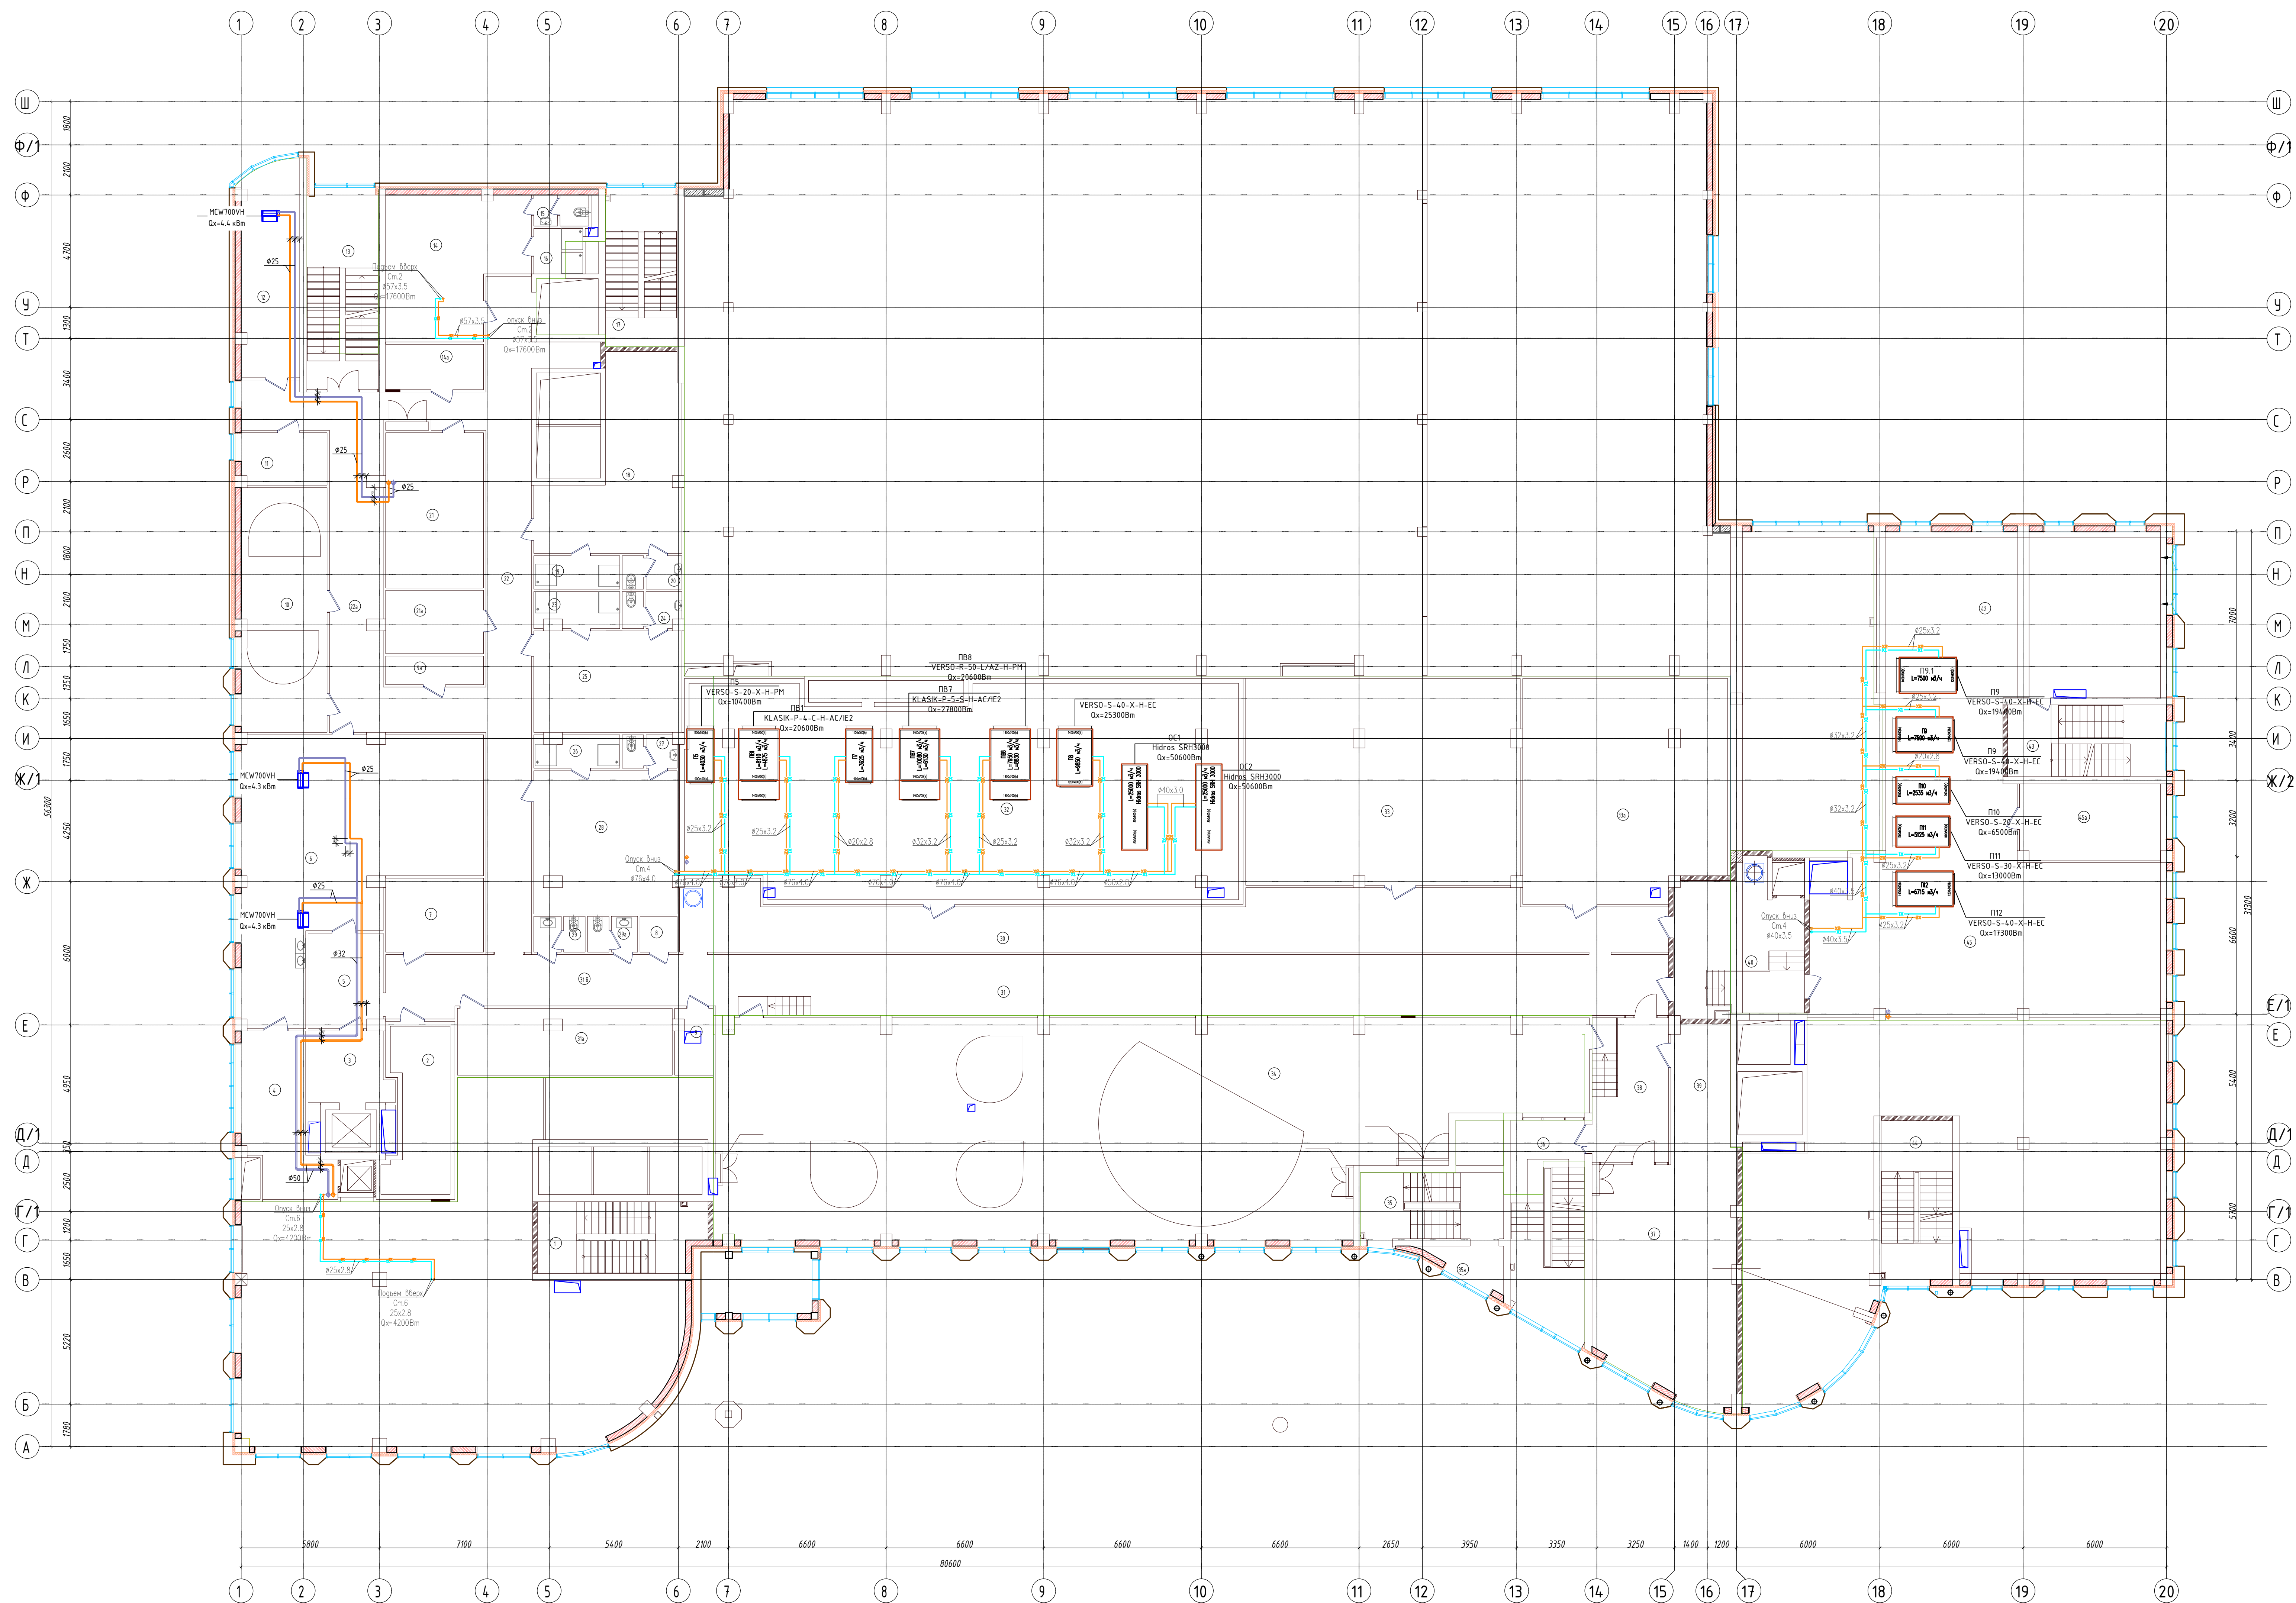


Экспликация помещений			
Поз	Наименование	площадь	Кат. помеще-ния
1	Лестничная клетка	20.1	
2	Ванная	20.6	
3	Сервировочная	9.9	
4	Мужская	20.9	
5	Сервировочная	12.3	
6	Столовая персонала	86.1	
7	Пом. Официантов	12.70	
8	Тех. помещение	2.3	
9	Клн	4.30	
9а	Тех. помещение	4.9	
10	Тех. помещение	37.60	
11	Тех. помещение	8.20	
12	Диспетчерская	21.7	
13	Лестничная клетка	25.2	
14	Гардеробная	31.70	
14а	Курительная	7.80	
15	Санузлы	2.9	
16	Душевая	3.80	
17	Лестничная клетка	19.9	
18	Гардеробная	35.1	
19	Душевая	3.0	
20	Санузел	5.4	
21	Комната хранения персонала	26.60	
22	Коридор	53.8	
22а	Коридор	52.70	
23	Душевая	63	
24	Санузел	3.6	
25	Гардеробная	26.40	
26	Душевая	4.70	
27	Санузел	3.1	
28	Гардеробная	35.9	
29	Санузел	3.2	
29а	Санузел	3.1	
30	Коридор	91.7	
31	Коридор	101.9	
32а	Центральная	25.20	
31б	Коридор	31.1	
32	Ванная	210.4	
33	Тех. помещение	98.9	
33а	Тех. помещение	78.20	
34	Тех. помещение	299.70	
35	Лестничная клетка	16.60	
35а	Лоджия	4.5	
36	Лестничная клетка	27.1	
37	Тех. помещение	55.1	
38	Коридор	19.4	
39	Тех. помещение	14.8	
40	Гардеробный холл	31.20	
42	Тех. помещение	98.7	
43	Лестничная клетка	19.56	
44	Лестничная клетка	19.51	
45	Тех. помещение	112.4	
45а	Кроссовая	19.90	

СХЕМА БЛОКИРОВКИ

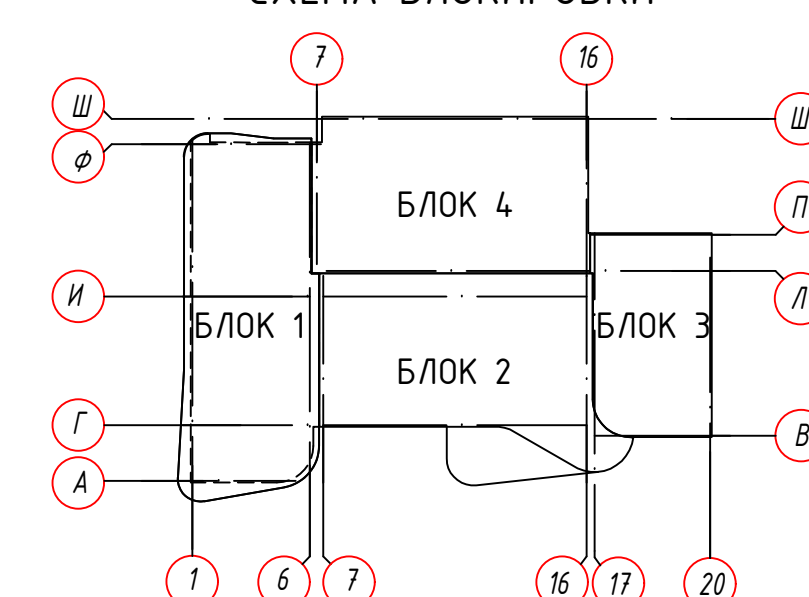


					02/09/ФОК-КС				
					Корректировка рабочего проекта "Реабилитационно-диагностический центр с асфальтированной (Физкультурно-оздоровительный комплекс с асфальтированной дорожкой Асфальт, район Есиль-Хуан, район Талас, аз № 25"				
Изм.	Кол.	Н	В	Лист	Подпись	Дата			
Гип				Галимжанов С.		02.26			
Проверка						02.26			
Разработка						02.26			
							Физкультурно-оздоровительный комплекс (Листы 1, 2, 3, 4)		
							РП		
							8		
							•		
							План кондиционирования тех. этажа на оим. «4.200		
							ТОО "Vitality Group"		

План кондиционирование 2-го этажа на отм. +7,350

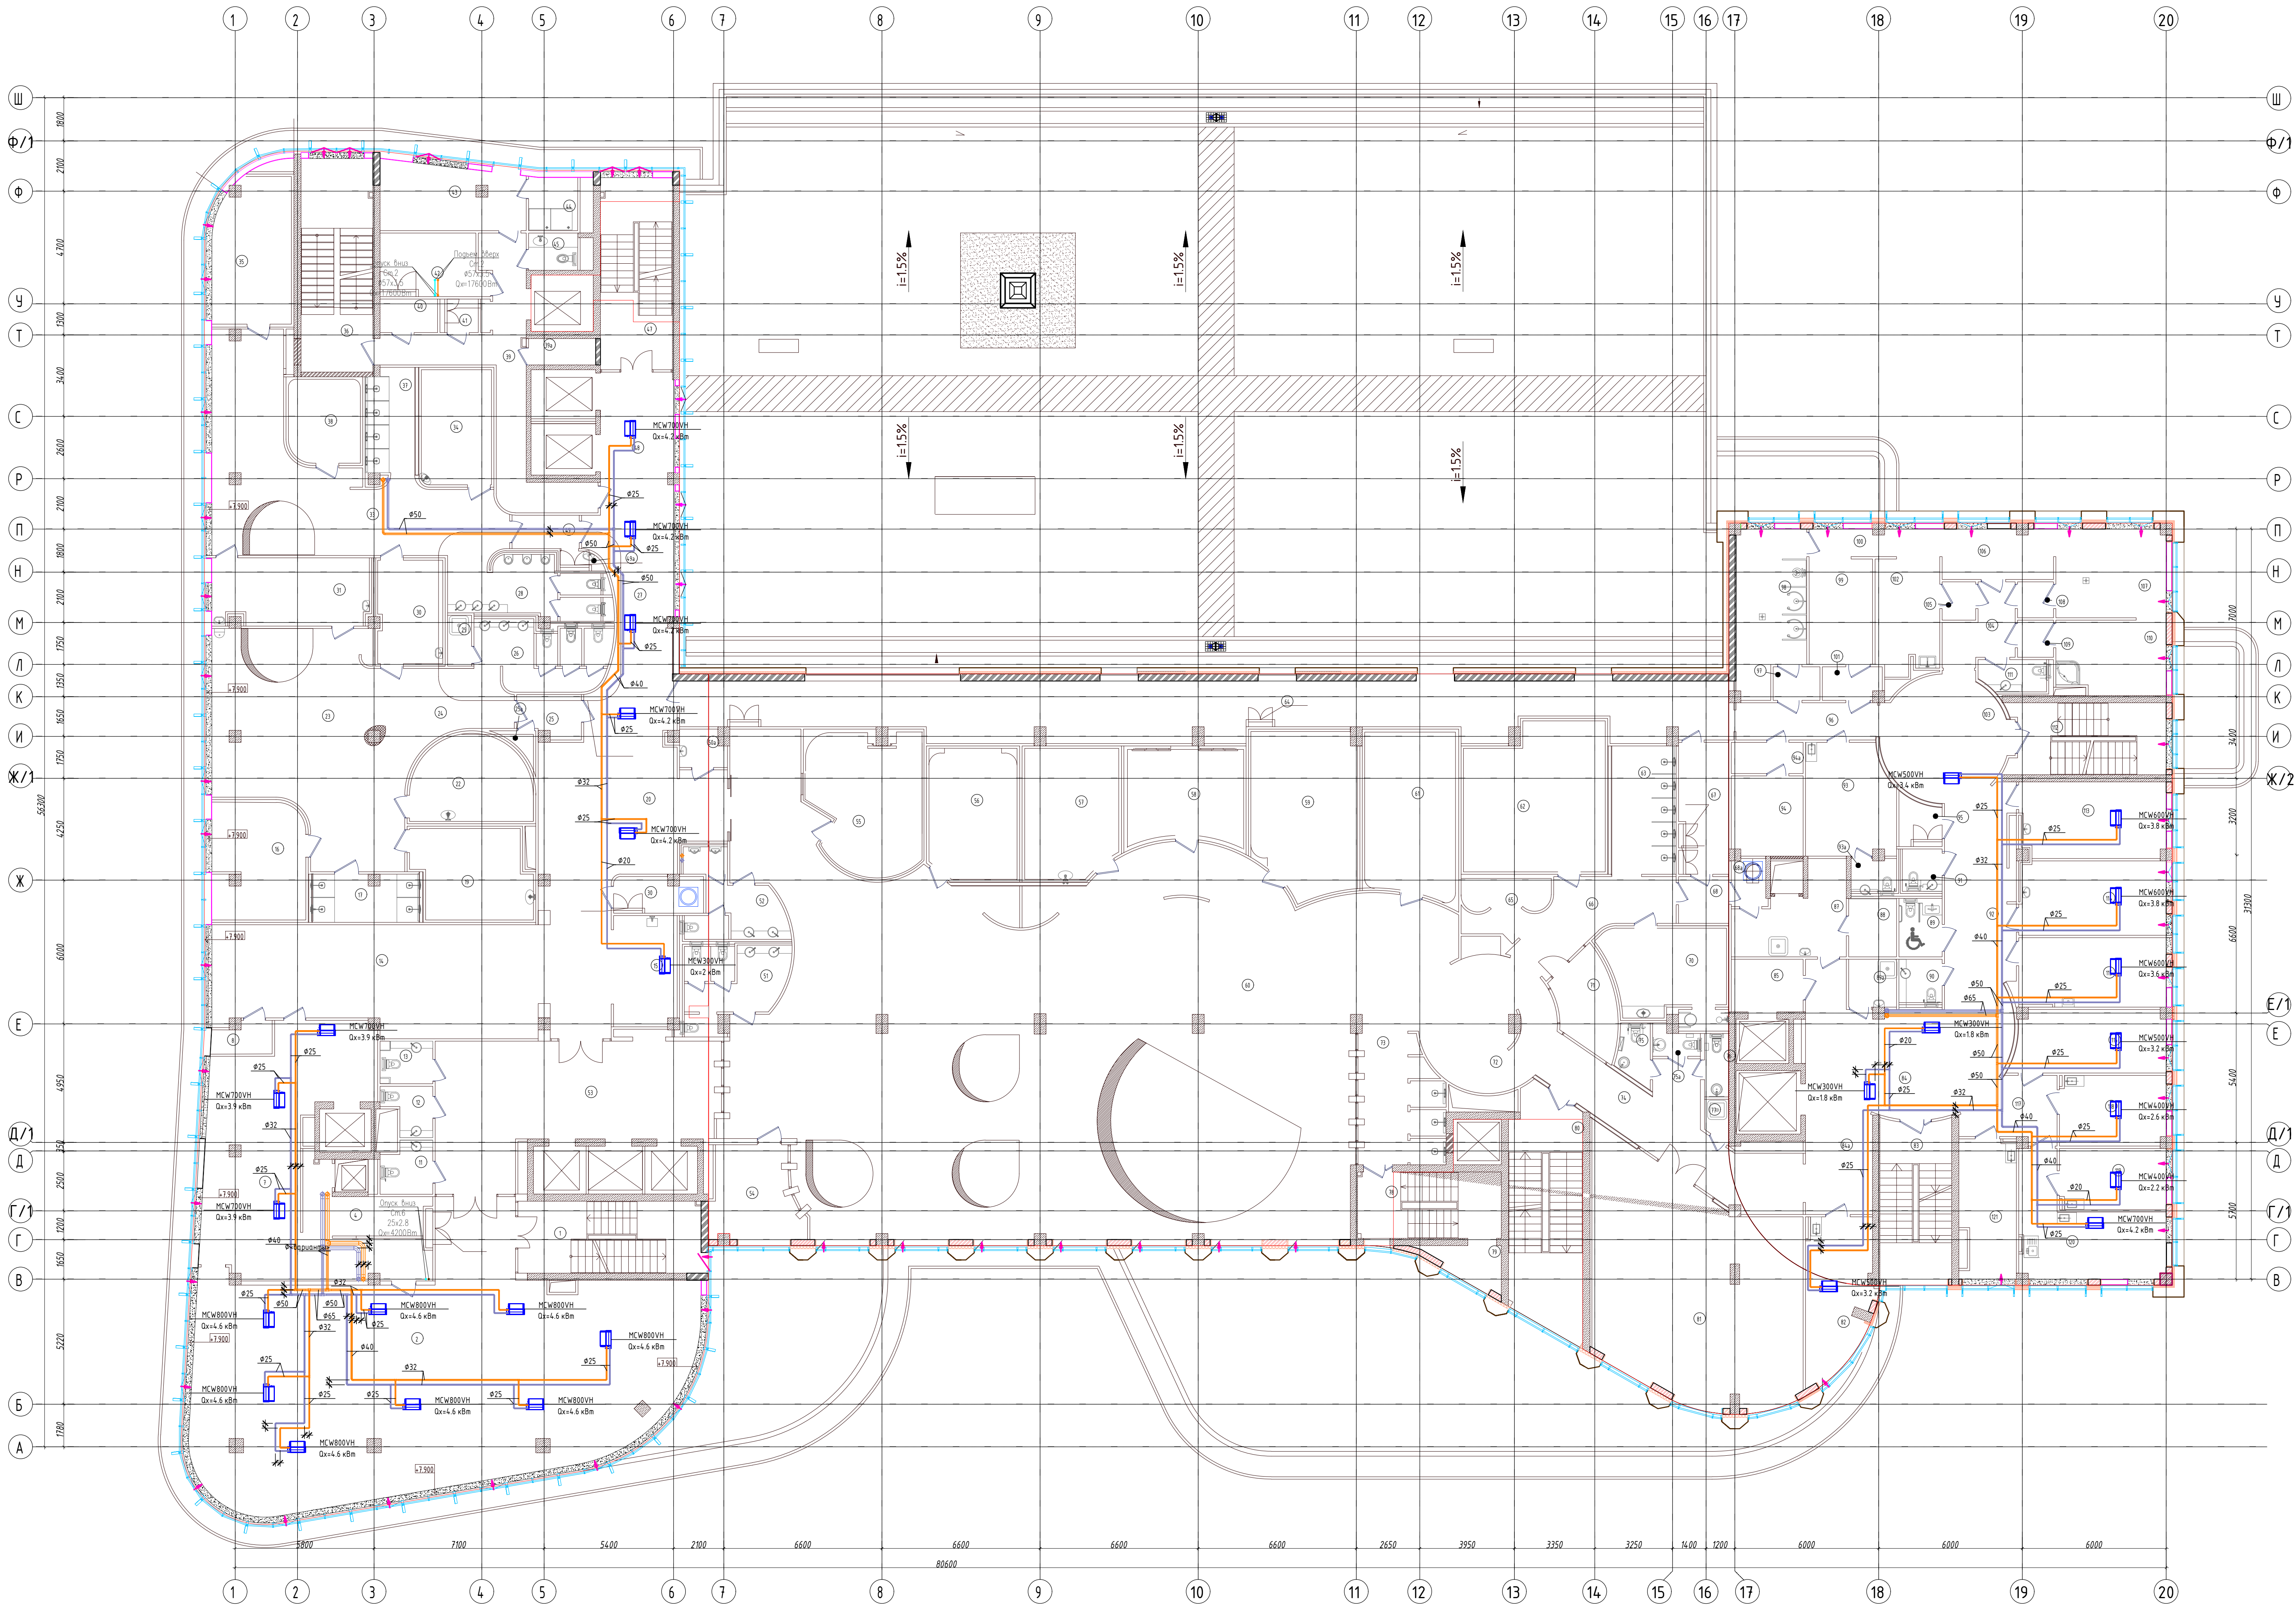


Экспликация помещений (начало)			Экспликация помещений (окончание)		
Поз	Наименование	Площадь	Поз	Наименование	Площадь
1	Лестничная клетка	22.5	83	Лестница	19.4
2	Ресторан	183.25	84	Холл	
4	Цех преобразования. Очистки и сортировки посуды	10.32	84а	Коридор	11.81
7	Догодочная-сервировочная бара	57.93	85	Лифтовой холл	6.39
8	Комната для курения	2.94	87	К/И	41.32
11	Санузел	4.3	88	Холл. Камеры временного хранения отходов	4.7
12	Санузел	3.49	89	Санузел ММГН	4.22
13	Санузел	3.76	89а	К/И	13.42
14	Зона фито бара	59.96	90	Санузел	3.12
15	Фито бар	12.35	91	Санузел	2.8
16	Русская баня	18.4	92	Коридор	22.3
17	Душевая	8.44	93	Процедурный кабинет гидроколлапроктологии с гигиеническим душем	16.44
19	Персон. Хамам-пилингочная	17.26	93а	Санузел	2.42
20	Ресторан	55.21	94	Тех.помещение	9.68
22	Хамам	16.14	94а	К/И	3.73
23	Женское отделение	63.37	95	Кабинет хранения чистого белья	2.81
24	Коридор	14.66	96	Коридор	9.32
25	Коридор	3.65	97	Раздевальня посетителей	3.19
25а	К/И	1.09	98	Душ-шаржа	18.31
26	Санузел	13.32	99	Душ-виши	11.62
27	Холл	32.6	100	Коридор	5.87
28	Санузел	12.7	101	Раздевальня посетителей	3.19
29	К/И	2	102	Талассотерапия	12.36
30	Индивидуальное парение	11.61	103	Холл	22.94
31	Пиллинг	9.04	104	Коридор	7.42
32	Пиллинг	8.25	105	Раздевальня посетителей	2.12
33	Мужское отделение	56.87	106	Помещение обслуживающего персонала	9.67
34	Персон. Хамам-пилингочная	14.03	107	Кабинет гидроассажа	16.8
35	Сауна	19.09	108	Раздевальня посетителей	2.13
36	Лестница	26.26	109	Раздевальня посетителей	2.2
37	Душевые	9.49	110	Кабинет гидроассажа	13.57
38	Хамам	10.24	111	Санузел	3.47
39	Коридор	25.05	112	Лестница	18.82
39а	Тех. Помещение	2.92	113	Кабинет врача проктолога	18.65
40	Комната слабых токов	3.27	114	Процедурный кабинет аппаратной термалитической коррекции (восточной)	18.39
41	Оборуд. Хамам	1.71	115	Процедурный кабинет косметолога лица и тела	17.17
42	Тех. Помещение	10.45	116	Процедурный кабинет аппаратной термалитической коррекции (криолитализ)	16
43	Помещение персонала	15.76	117	Коридор	9.37
44	Душевая	4.37	118	Кабинет врачей-косметологов	12.62
45	Санузел	3.04	119	Процедурный кабинет массажа	10.96
47	Лестница	23.6	120	Процедурный кабинет обертывания/уходов	20.67
48	Холл	14.26	121	Криосауна	12.75
49	Коридор	3.76			
49а	К/И	0.94			
50	К/И	5.02			
50а	К/И	2.78			
51	Санузел X	12.17			
52	Санузел M	10.15			
53	Холл	55.18			
54	Баня травяная	13.03			
55	Баня кожан	25.68			
56	Баня арома-фруктовая	19.73			
57	Хамам	20.56			
58	Баня каменная	18.2			
59	Баня русская мажельная	28.35			
60	Зал	410.35			
61	Баня финская	25.58			
62	Баня общая	34.43			
63	Душ	14.23			
64	Коридор	92.33			
65	Душ	7.51			
66	Коридор	15.45			
67	Тех. Помещение бани	10.59			
68	Тандыр	3.94			
68а	Помещение Вальтерабда	2.73			
70	Индивиду парение (2 стола)	18.51			
71	Снежная комната	8.86			
72	Холл	27.48			
73	Душевые	15.98			
74	Коридор	29.93			
75	Санузел	2.98			
75а	Санузел	2.02			
76	Санузел	2.55			
77	К/И	1.53			
78	Лестница	16.25			
79	Тандыр	3.61			
80	Лестница	28.83			
81	Салонная комната + Тепловизор	76.28			
82	Кабинет фито и прессо терапии	15.39			

СХЕМА БЛОКИРОВКИ

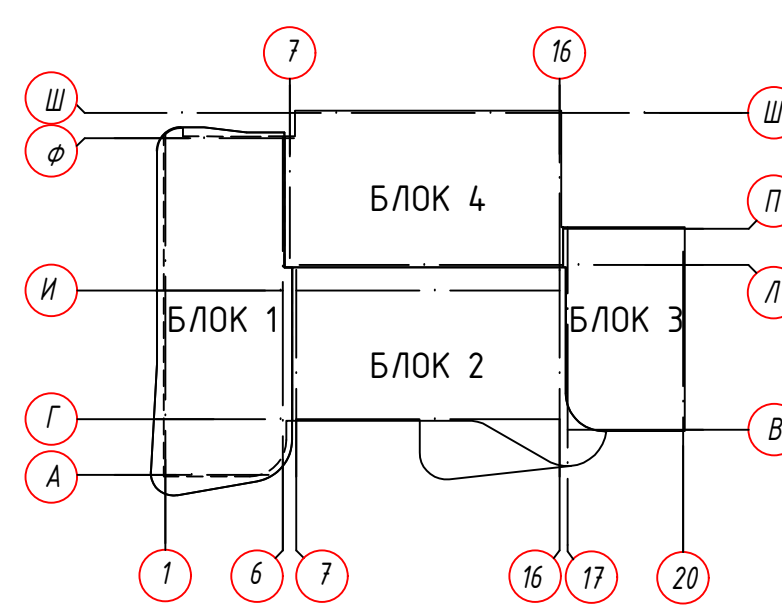


02/09/ФОК-ХС									
Корректировка рабочего проекта Реабилитационно-диагностический центр с остеохондрозом (Физиотерапия-аппаратный комплекс с использованием аппар. Алмаз, район Соснов. ур. Курорт-Вос. Таган. адм. 25)									
Изм.	Код	И.В.И.И.	Подпись	Дата	02.09	02.09	02.09	02.09	02.09
ИП	Г	А	С	С	С	С	С	С	С
Проектирование	Разработка	Разработка	Разработка	Разработка	Разработка	Разработка	Разработка	Разработка	Разработка
План кондиционирования 2-го этажа на отм. +7,350									
100 "Vitality Group"									

План кондиционирование 3-го этажа на отм. +12,000

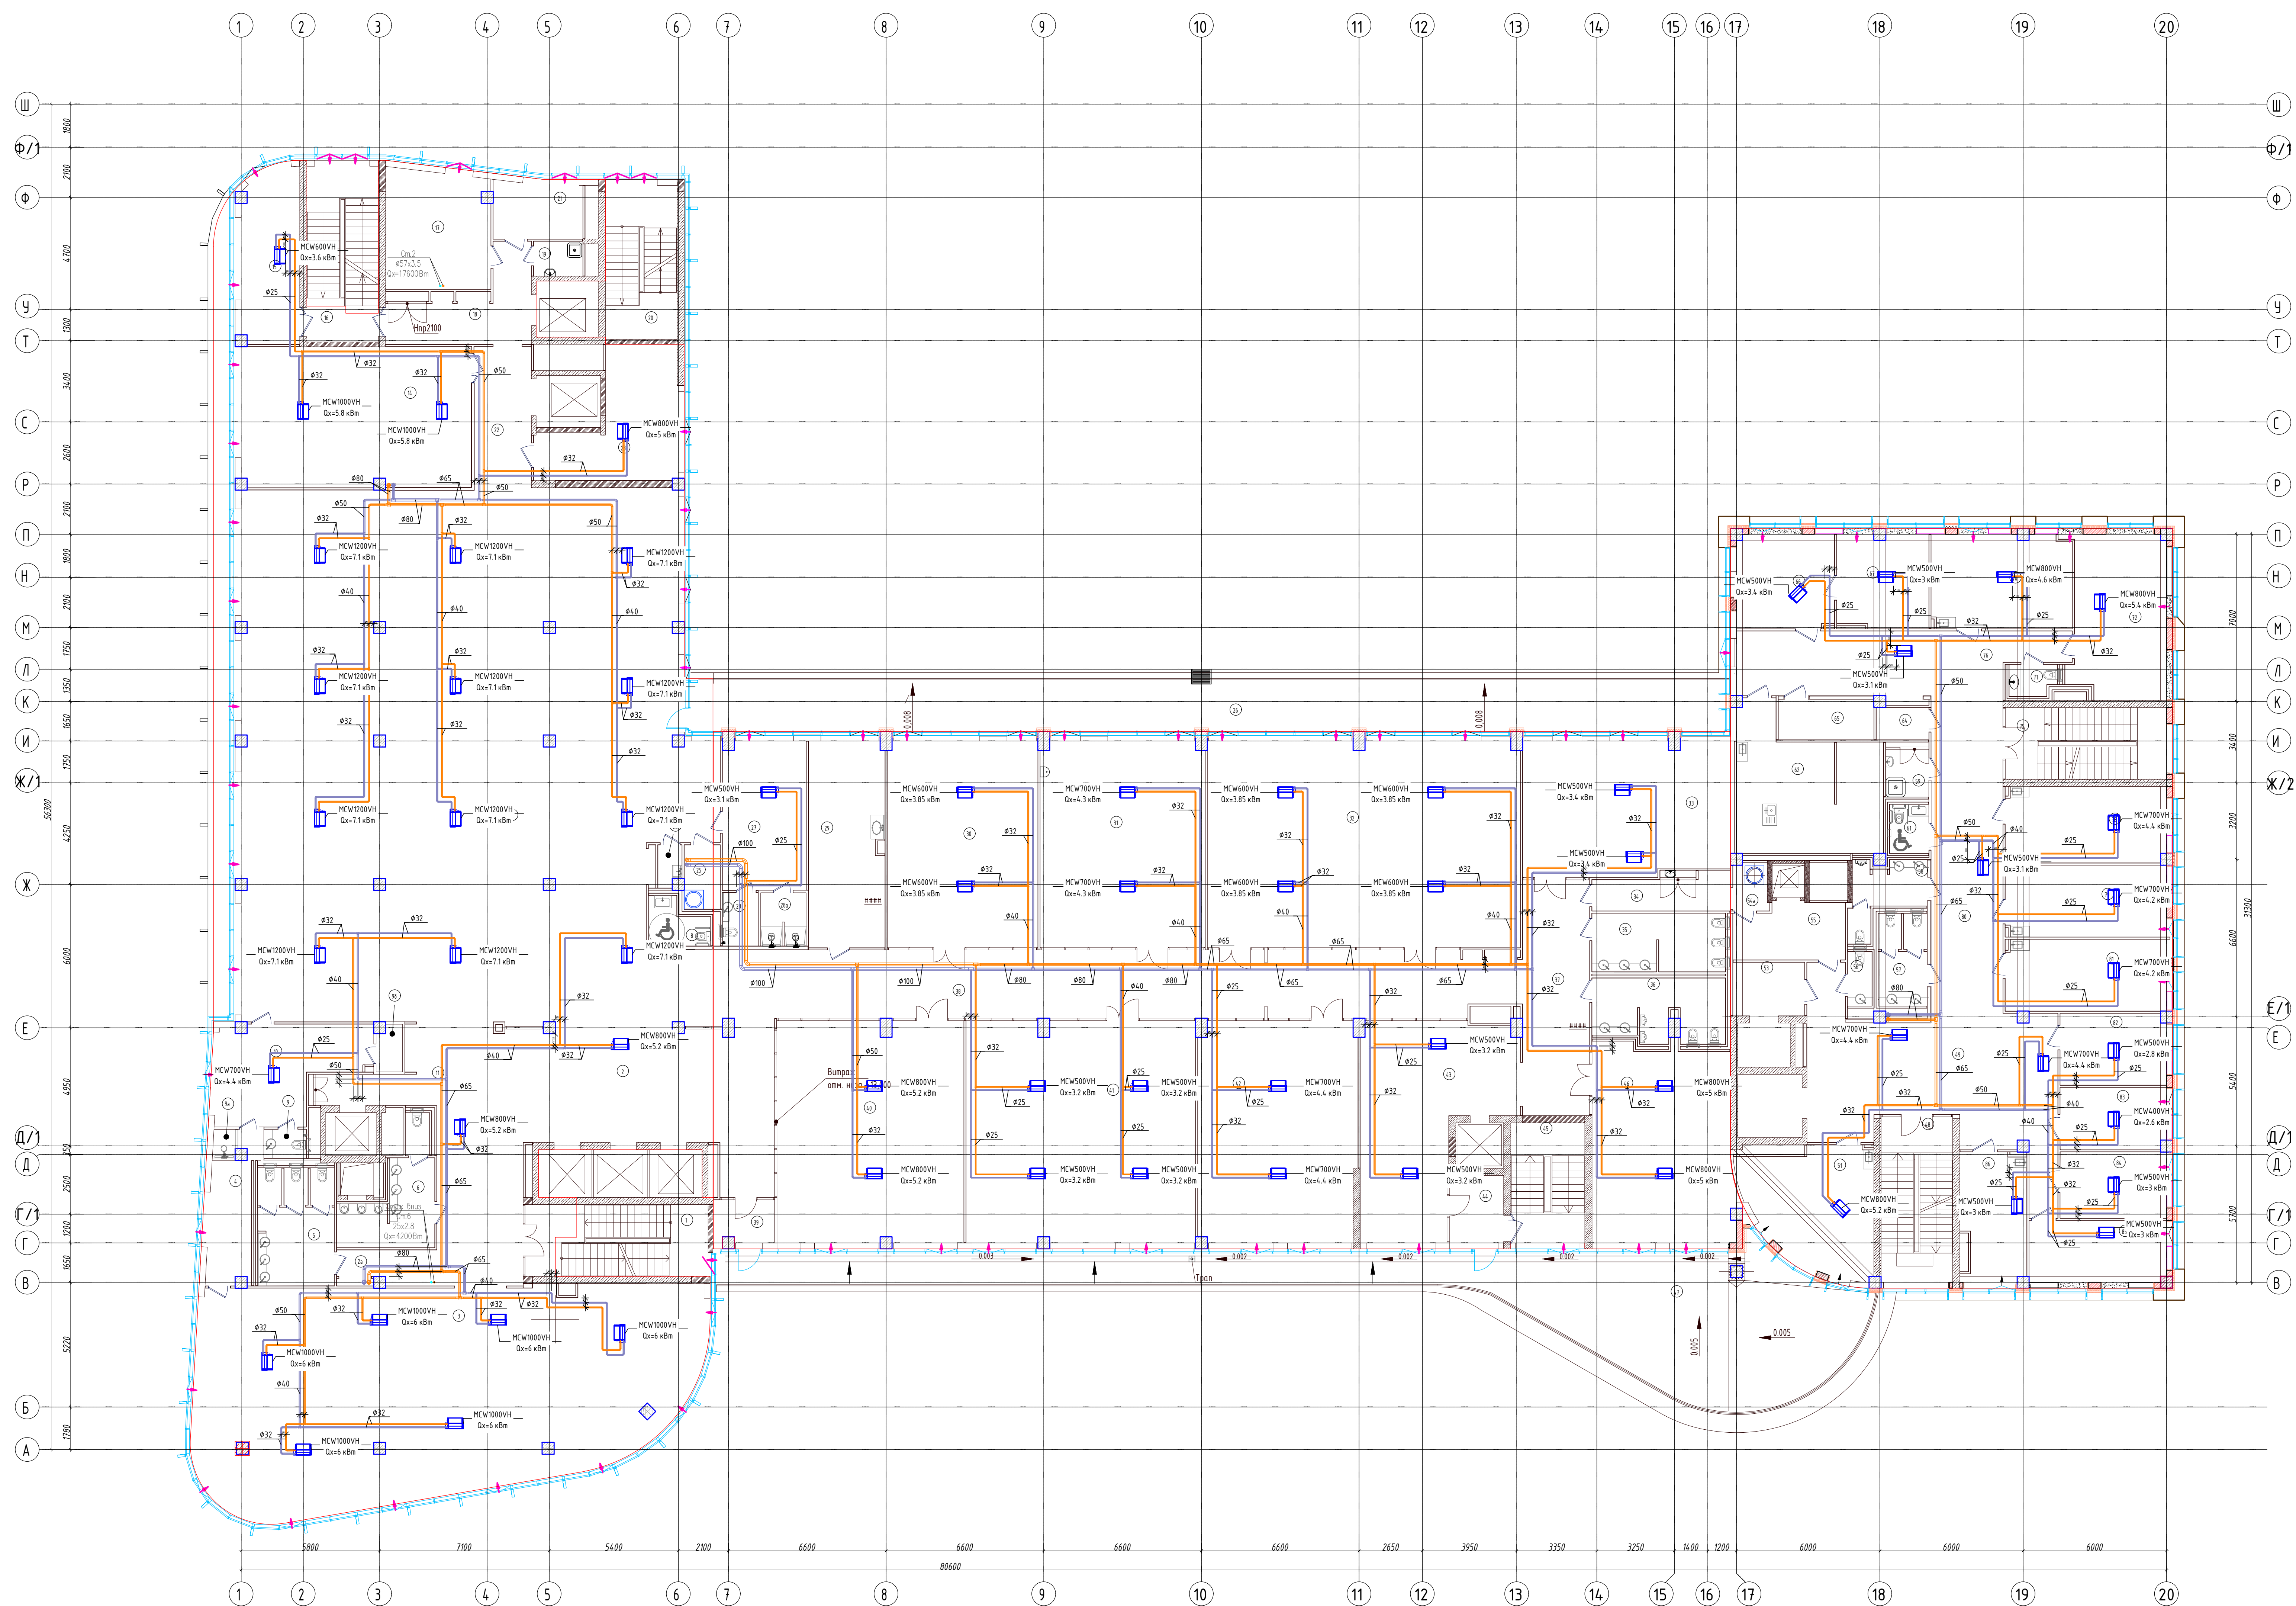


Поз	Экспликация помещений		Кол. помещений
	Назначение	площадь	
1	Лестничная клетка	231	
2	Холл	68.6	
2а	Коридор	27.1	
3	Зона кардио тренажеров	179.6	
4	Зал персонального тренера	9.80	
5	Санузел Х	16.92	
6	Санузел М	12.61	
8	Санузел	4.2	
9	Санузел	2.2	
9а	Душевая	2.2	
9б	Душевая	2.2	
10	Тренажерная М	2.0	
11	Фойе/бар	13.4	
12	Тренажерный зал	426.4	
14	Скайл студия	57.9	
15	Кабинет менеджера	17.7	
16	Лестница	22.8	
17	Тех. помещение	21.6	
19	К/И	36.6	
20	Лестница	19.9	
21	Инжендерная	9.4	
22	Коридор	16.1	
23	Кабинет персонального тренера	24.3	
25	Тех. помещение	6.0	
26	К/И	1.6	
26а	Лоджия	91.8	
27	Теренерская Х	22.2	
28	Санузел	3.3	
28а	Душевые	2.6	
29	Кабинет менеджера	28.1	
30	Спортивный зал/бассейн/Занятия пилатес	55.5	
31	Студия бального искусства	60.7	
32	Взрослая и детская студия групповых и танцевальных занятий	165.4	
33	Детская клуб	4.9	
34	Коридор	8.1	
35	Санузел	13.5	
36	Санузел	13.52	
37	Коридор	56.6	
38	Коридор	72.8	
39	Тамбур	4.8	
40	Studio Body & Mind, Yoga, Aerobic	73.8	
41	Взрослая и детская студия групповых и танцев. занятий	90.8	
42	Детская спортивно-сервиз студия	62.5	
43	Ресторан	45.26	
44	Санузел	6.55	
45	Лестница	16.2	
46	Детская студия функциональной пренерники	49.2	
47	Лоджия	117.1	
48	Лестница	21.4	
49	Холл	57.3	
51	Кабинет УЗИ	25.8	
53	Лифтовой холл	6.70	
54а	Белье/бар	2.75	
55	Холод. Камеры временного хранения отходов	10.7	
56	Санузел	2.3	
57	Санузел	7.7	
58	Санузел	7.2	
59	К/И	3.42	
61	Санузел М/МГН	3.3	
62	Лаборатория – заборы крови и материала	21.3	
64	Корсвая	3.0	
65	Кладовая хранения чистого белья	6.7	
66	Кабинет врача дерматоло-венеролога	16.3	
67	Процедурный кабинет дерматоло-венеролога	14.9	
70	Кабинет врача гинеколога	22.8	
71	Санузел посетителя	2.5	
72	Процедурный кабинет гинеколога	26.6	
75	Лестница	20.2	
76	Коридор	35.2	
78	Кабинет врача онколога	21.4	
79	Кабинет врача эндокринолога	20.3	
80	Коридор	40.8	
81	Кабинет врача кардиолога	20.5	
82	Кабинет Глазного врача	13.50	
83	Кабинет Сан.гл.врача	11.70	
84	Кабинет бьюти-терапии	12.6	
85	Процедурная	15.0	
86	Кабинет врача диетолога-нутрициониста	14.8	

СХЕМА БЛОКИРОВКИ

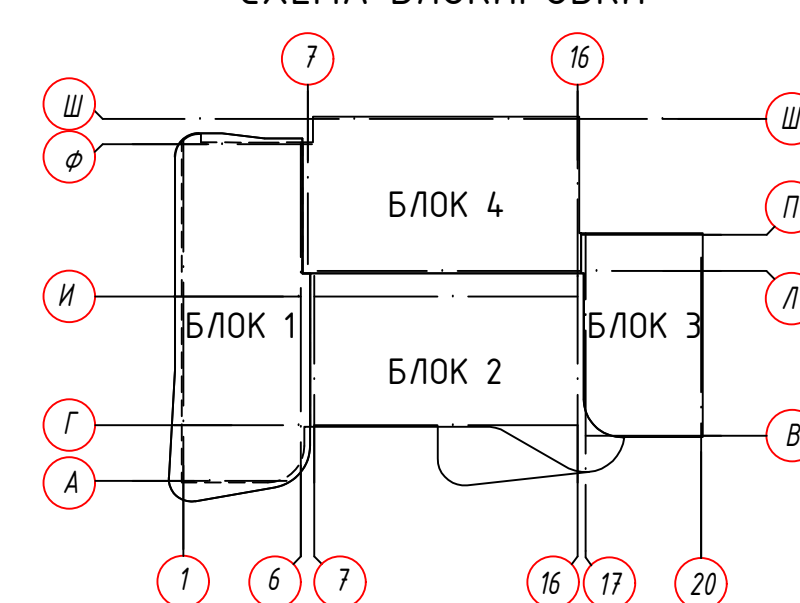


					02/09/ФМК-КС				
					Корректировка рабочего проекта "Реализационно-диагностический центр с ассоциированной физкультурно-олимпийской комплекс с олимпийской горой Астана, район Есиль-Хуань в г. Астана, ст. № 25"				
					Физкультурно-олимпийский комплекс (Этапы 1, 2, 3, 4)				
Изм.	Кол.	Н	В	Лист	Подпись	Дата	Сводный	Таблица	Листов
Гип				Галимжанов С.		02.26			
Проверка						02.26	РП	10	•
Разработка						02.26			
План кондиционирования 3-го этажа на о.п. = 12,000							ТОО "Vitality Group"		

План кондиционирования 4-го этажа на отм. +16.800

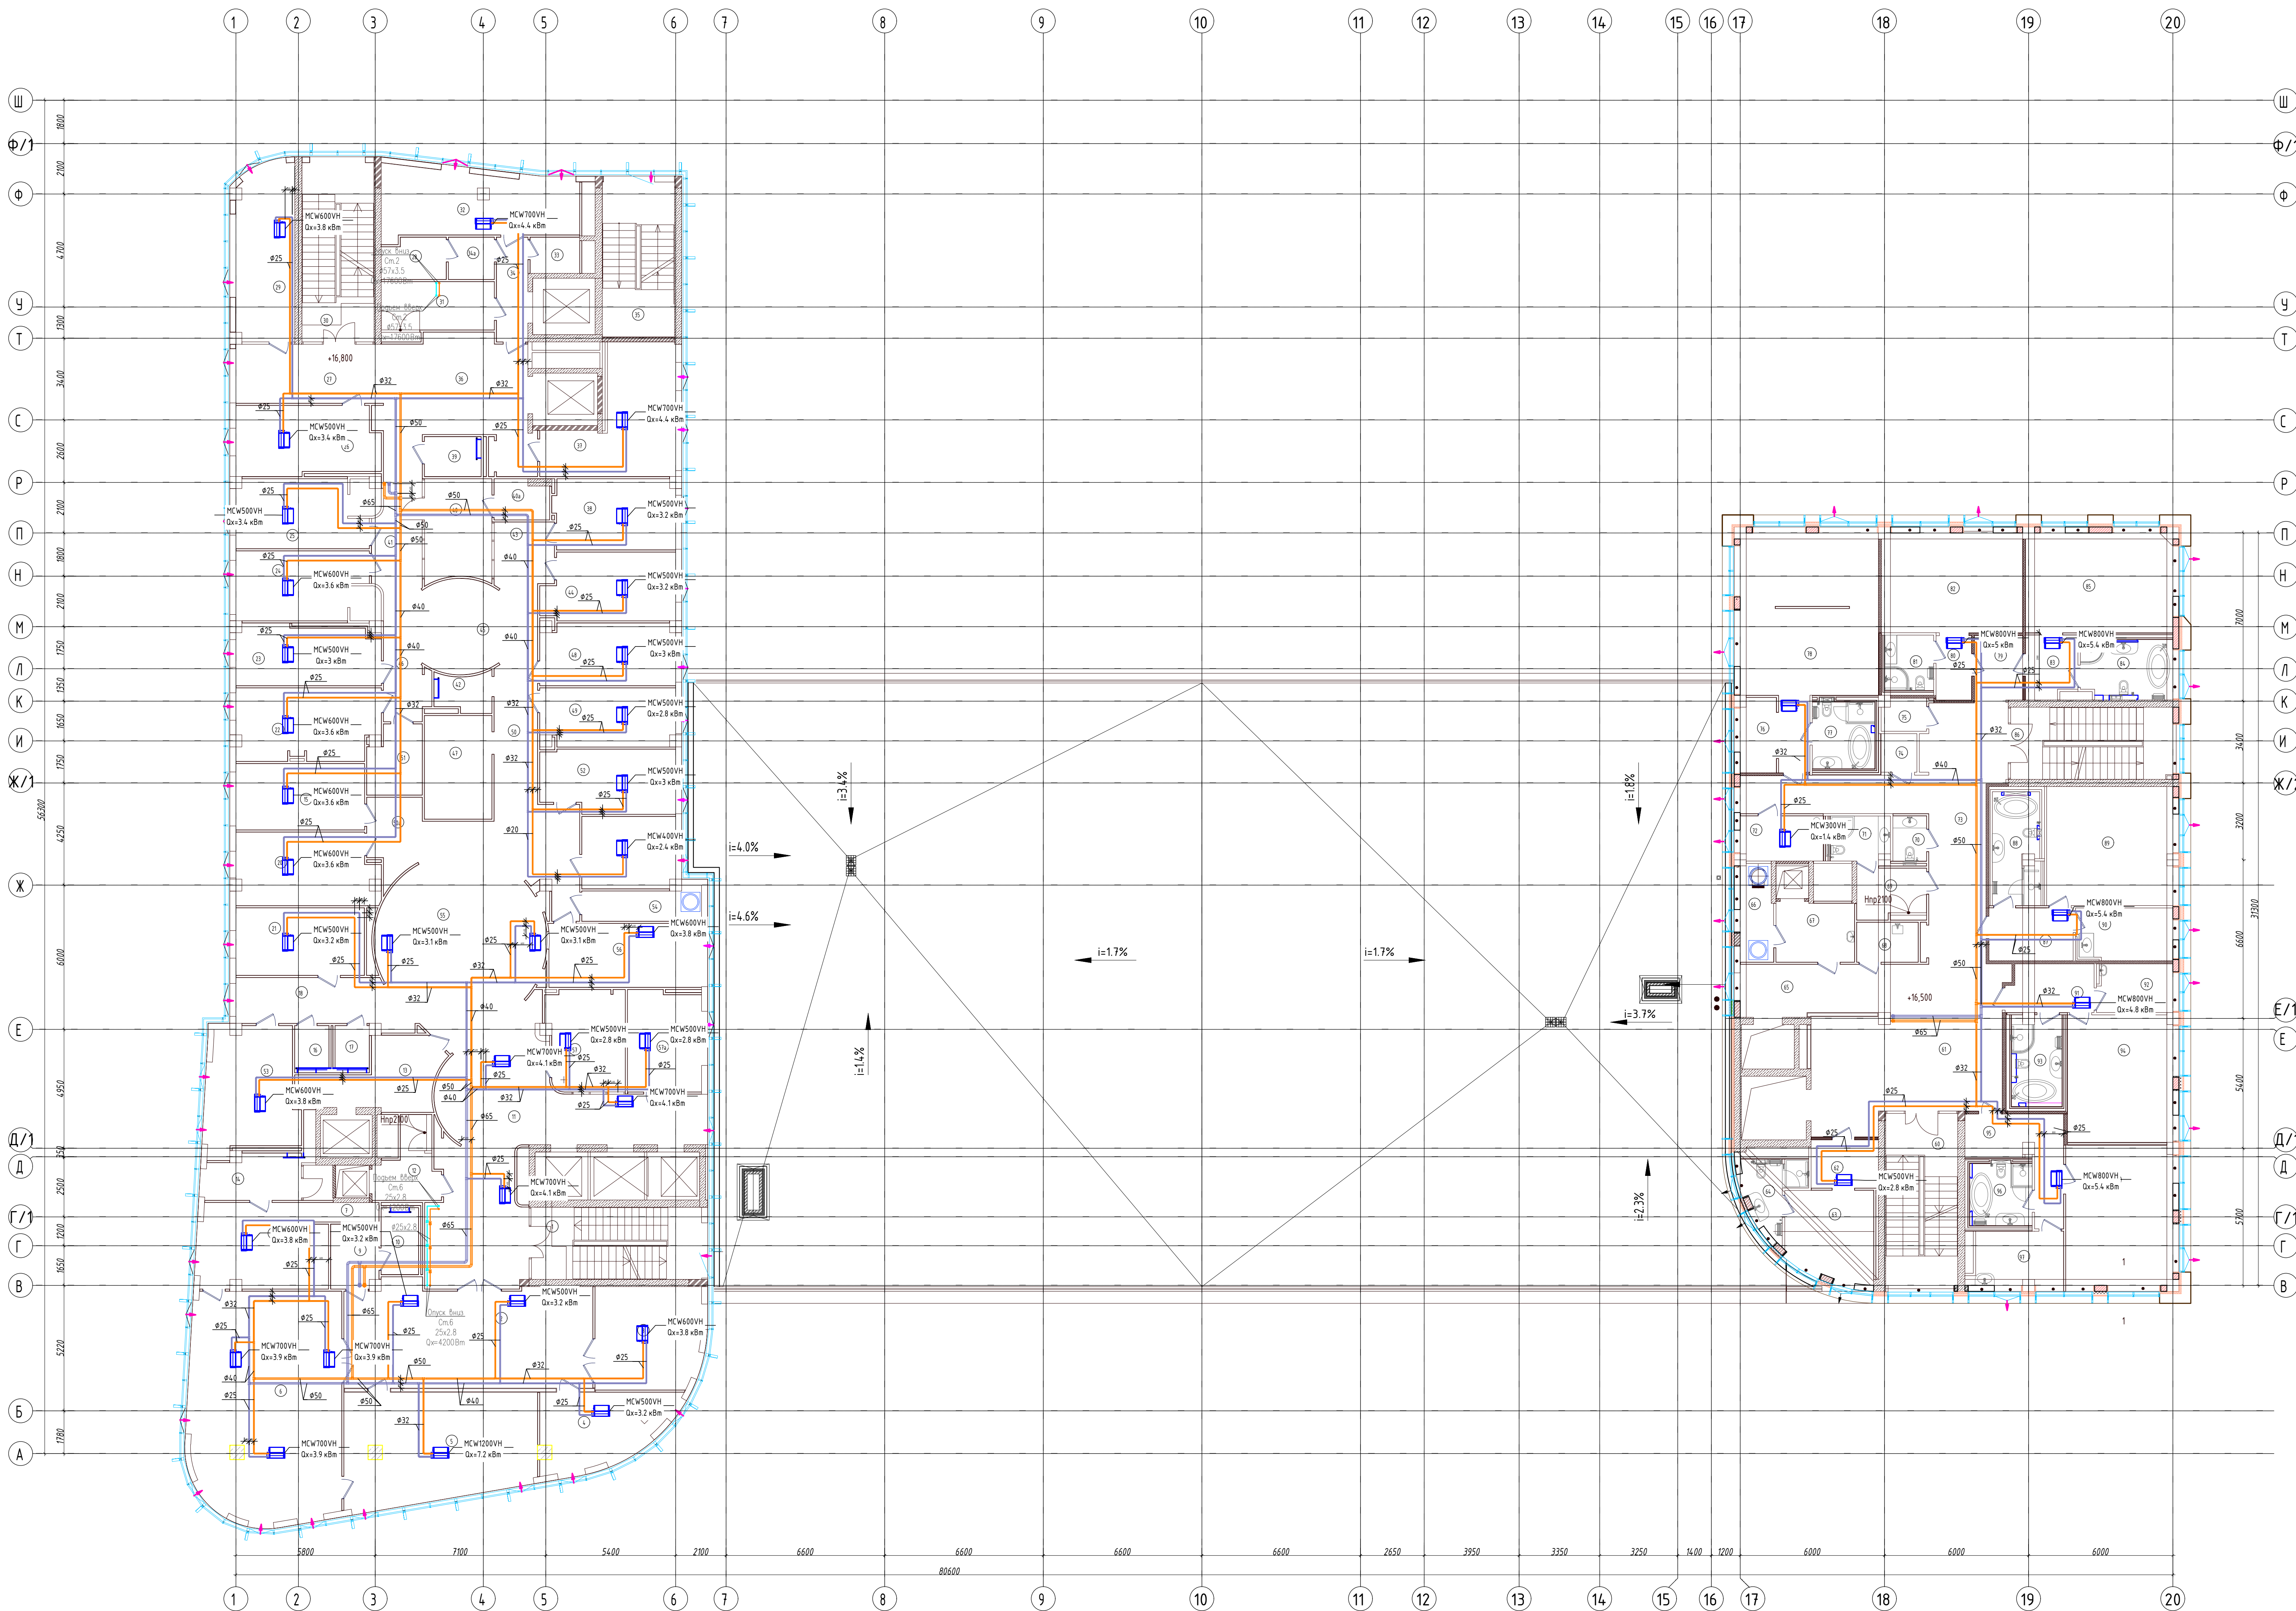


Экспликация помещений				Экспликация помещений			
Поз	Наименование	площадь	Кат. помеще-ния	Поз	Наименование	площадь	Кат. помеще-ния
Блок 1				Блок 3			
1	Лестничная клетка	218		60	Лестничная клетка	218	
2	Ресепшен	4,27		61	Лифтовый холл	44,50	
3	Кабинет	19,0	№0		Номер 1		
4	Кабинет	15,7			в том числе		
5	Переоборная	35,9	62	Холл		5,60	
6	Кабинет ген-директора	58,9	63	Спальня		13,5	
7	Помещение	2,2	64	Санузел		5,8	
8	Канцелярия отдыха	18,7	65	Лифтовый холл		13,3	
9	Мужской туалет	5,2	66	Тех.помещение		5,8	
10	Санузел	2,5	67	К/М		8,1	
11	Холл	61,6	68	Кухня		4,2	
12	К/М	7,0	69	Помещение персонала		6,4	
13	Сервер ресепшен	2,5	70	Санузел		2,6	
14	Санузел	7,5	71	Санузел		4,5	
15	Каб. маникюра и педикюра	30,6	72	Книжная мастерская		6,7	
16	Санузел	2,5	73	Коридор		42,30	
17	Санузел	2,5	74	Бельевая		2,4	
18	Коридор	13,5	75	Красочная		2,5	
19	Барбер		№0	Номер 2			
20	Парикмахерская	17,4			в том числе		
21	Парикмахерская	15,2	76	Холл		5,3	
22	Кабинет	17,6	77	Санузел		7,2	
23	Кабинет	14,8	78	Спальня		41,3	
24	Кабинет	17,2	79	Коридор		5,4	
25	Кабинет	16,7	№0	Номер 3			
26	Кабинет Впл. косметолога	15,6			в том числе		
27	Коридор	16,9	80	Холл		3,9	
28	Электропешковая и красочная	4,4	81	Санузел		4,7	
29	Персональный мастер	18,6	82	Спальня		25,0	
30	Лестница	22,9	№4	Номер 4			
31	Стерилизационная	10,2			в том числе		
32	Помещение персонала	22,0	83	Холл		5,5	
33	Санузел	3,1	84	Спальня		10,0	
34	Коридор	5,7	85	Санузел		26,7	
34а	К/М	3,3	86	Лестница		20,8	
35	Лестница	19,9	№0	Номер 5			
36	Холл	31,6			в том числе		
37	ВМТ маникюра и педикюр	22,1	87	Холл		7,7	
38	Кабинет	15,2	88	Спальня		25,45	
39	Санузел	3,9	89	Санузел		26,8	
40	Парк аппарат	11,7	90	Массажная		8,8	
40а	Красочная	3,6	№0	Номер 6			
41	Коридор	7,0			в том числе		
42	Санузел	3,3	91	Холл		7,1	
43	Коридор	6,8	92	Массажная		6,7	
44	Кабинет	15,3	93	Санузел		7,8	
45	Холл	14,0	94	Спальня		24,0	
46	Коридор	9,1		Номер 7			
47	Кабинет	12,0			в том числе		
48	Кабинет	14,6	95	Холл		10,7	
49	Кабинет	13,6	96	Санузел		6,8	
50	Коридор	14,2	97	Массажная		8,9	
50а	Коридор	23,3	98	Спальня		27,6	
51	Склад бельевая	6,1				462,28	
52	Каб. маникюра и педикюра	14,6					
53	Кабинет	18,5					
54	К/М	6,4					
55	Ресепшен	4,09					
56	Кабинет директора салона	17,4					
57	Визажист	13,2					
57а	Укладочная сушилка	13,3					

СХЕМА БЛОКИРОВКИ

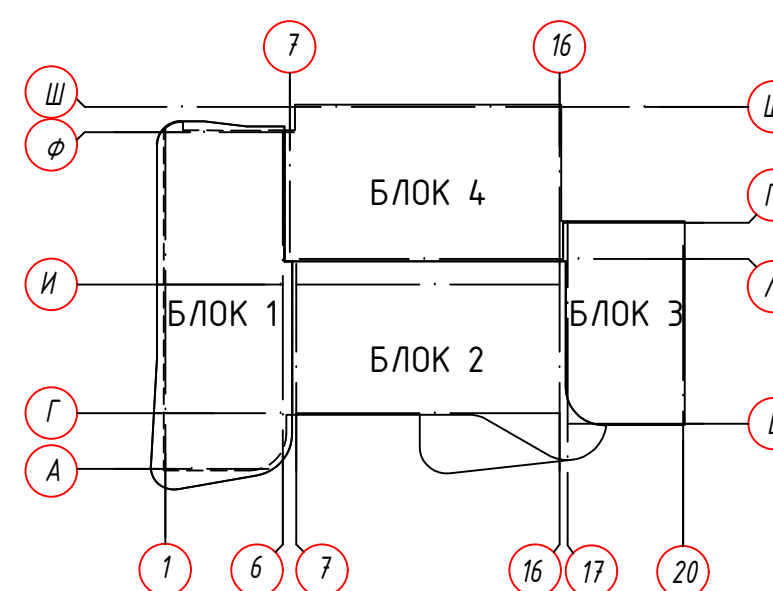


					02/09/90К-Х				
					Корректировка рабочего проекта "Реабилитационно-диагностический центр с отделениями (Физикультура-образовательный комплекс с отделениями) города Астана, район Селькупы-Бет Талас, 39 М 25"				
Изм.	Кол.	Н док	Лист	Подпись	Дата	Физикультура-образовательный комплекс			
ГП		Галимжанов	С		02.26	Худейев	Лист	Лист	25
Проверил					02.26	РП	11	•	
Разработал					02.26				
План кондиционерования 4-го этажа на отп. +16.80						ТОО "Vitality Group"			

План кондиционирования 5-го этажа на отм. +21.600

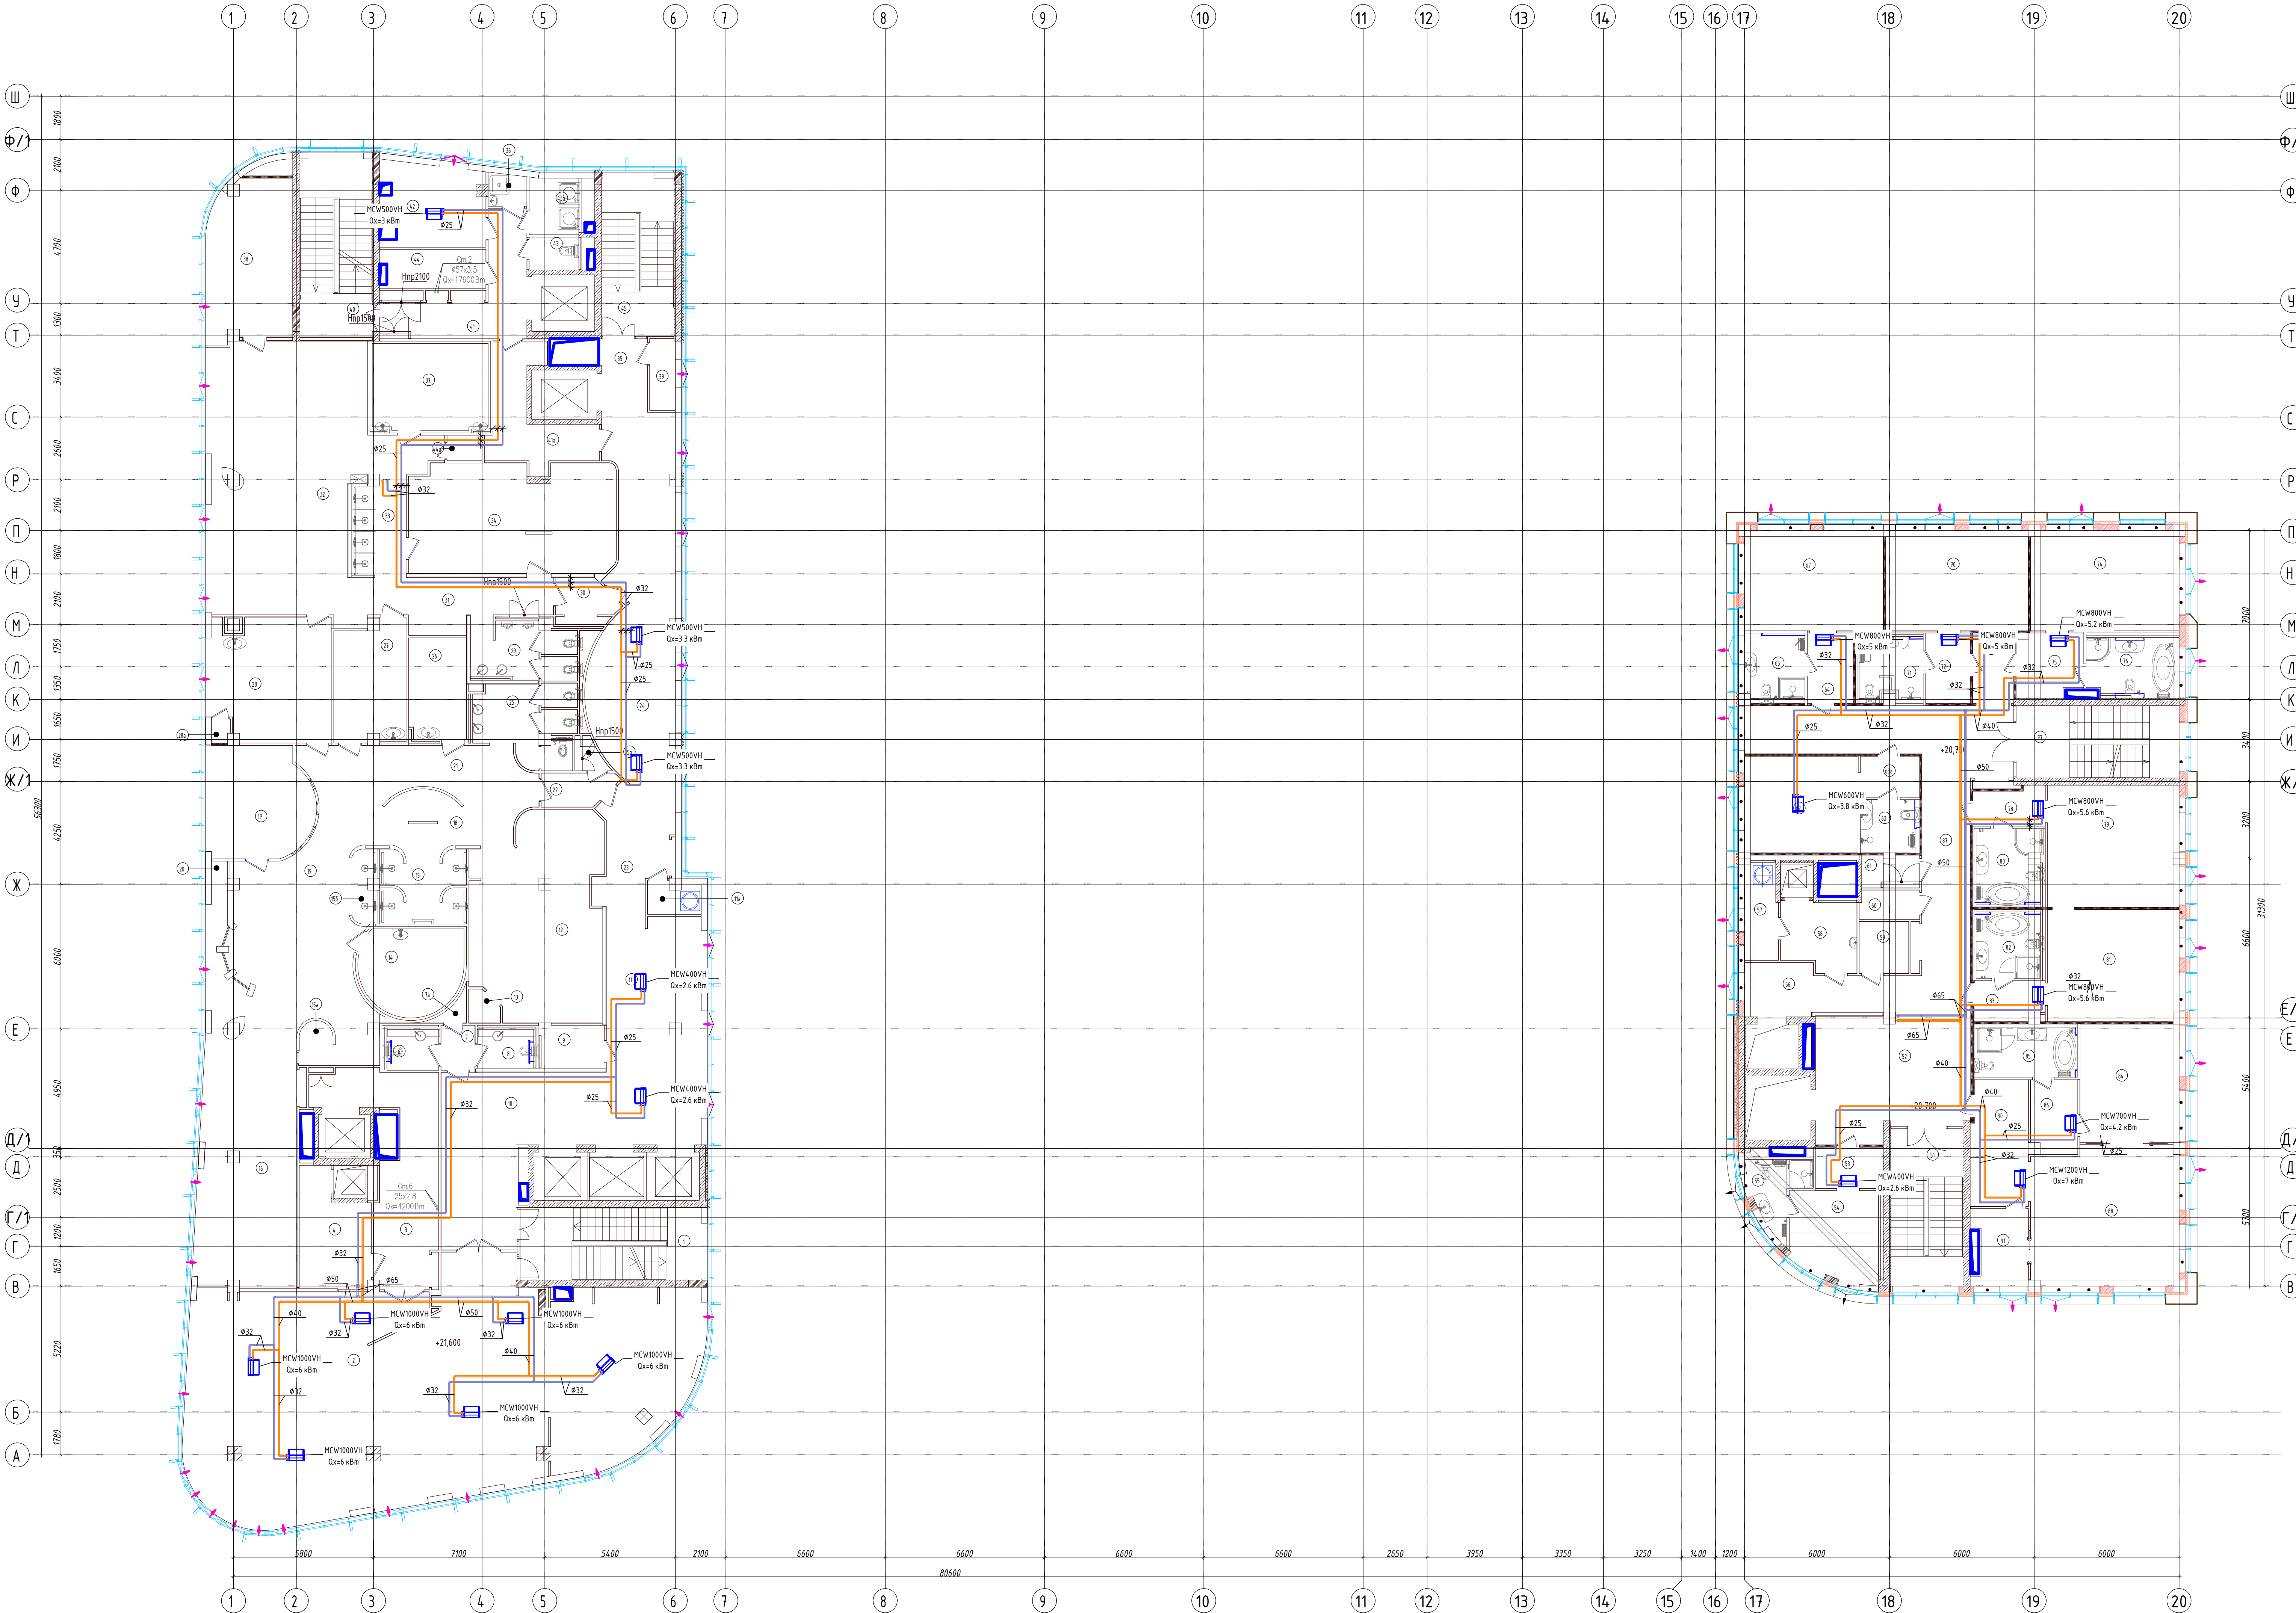

Экспликация помещений (начало)			Экспликация помещений (окончание)		
Поз	Наименование	площадь	Поз	Наименование	площадь
Блок 3					
1	Лестничная клетка ЛМ-3.1	23.2	51	Лестница ЛМ-13	19.60
2	Помещение	180.0	52	Холл	315
3	Раздаточная	25.4		Номер 1	
4	Очистка, сортировка пудры	12.60		В том числе	
5	Санузел	3.60	53	Холл	5.4
7	Тандыр	2.6	54	Санузел	12.8
7а	Оборудование камин	1.0	55	Санузел	5.4
8	Санузел	3.8	56	Лифтовый холл	16.2
9	Гардероб	4.5	57	Подсобное помещение	5.4
10	Холл	45.4	58	ПИИ	8.6
11	Ресторан	25.7	59	Кухня	4.4
11а	Пом. Бельевого	2.8	60	Кроссовая	2.9
12	Пом. Бельевого	43.1	61	Бельевая	3.0
13	Канната переобивания	1.5		Номер 2	
14	Хаммам	15.30		В том числе	
15	Душевые	10.9	62	Санузел	18.8
15а	Душевые	2.4	63	Санузел	5.0
15b	Душевые	2.9	63a	Холл	4.2
16	Зона отдыха	85.2		Номер 3	
17	Сауна	19.4		В том числе	
18	Фены	7.0	64	Холл	5.5
19	Холл	54.0	65	Санузел	6.7
20	Тех.помещение	1.2	67	Санузел	24.4
21	Коридор	18.4		Номер 4	
22	Тандыр	3.9		В том числе	
23	Холл	15.6	70	Спальня	24.4
24	Холл	32.4	71	Санузел	6.5
25	Санузел	12.1	72	Холл	5.4
25a	Санузел	1.4	73	Тандыр	4.9
26	Массажная	10.0		Номер 5	
27	Индивидуальное парение	13.85		В том числе	
28	Массажная	24.63	74	Спальня	25.4
28a	Тех.помещение	0.35	75	Холл	7.2
29	Санузел	9.9	76	Санузел	20.2
30	Тандыр	4.3	77	Лестница ЛМ-2.3	9.1
31	Коридор	15.9		Номер 6	
32	Зона отдыха	75.44		В том числе	
33	Душевые	8.30	78	Холл	4.6
34	Вип раздевалка	37.90	79	Спальня	27.4
35	Лифтовый холл	21.3	80	Санузел	8.2
36	КШ	2.1		Номер 7	
37	Хаммам	18.8		В том числе	
38	Сауна	23.6	81	Спальня	25.2
39	Канната для курения	3.4	82	Санузел	7.4
40	Лестница ЛМ-2.1	22.8	83	Холл	4.7
41	Коридор	13.2		Номер 8	
41a	Коридор	12.72		В том числе	
42	Канната персонала	15.0	84	Спальня	20.1
43	Санузел	2.3	85	Санузел	8.4
43a	Душевые	4.80	86	Гардероб	5.8
44	Тех.помещение	7.0	87	Коридор	5.64
44a	Душ	1.5	88	Гостиная	34.7
45	Лестница ЛМ-11	20.3	90	Холл	12.3
			91	Кухня	6.8

СХЕМА БЛОКИРОВКИ

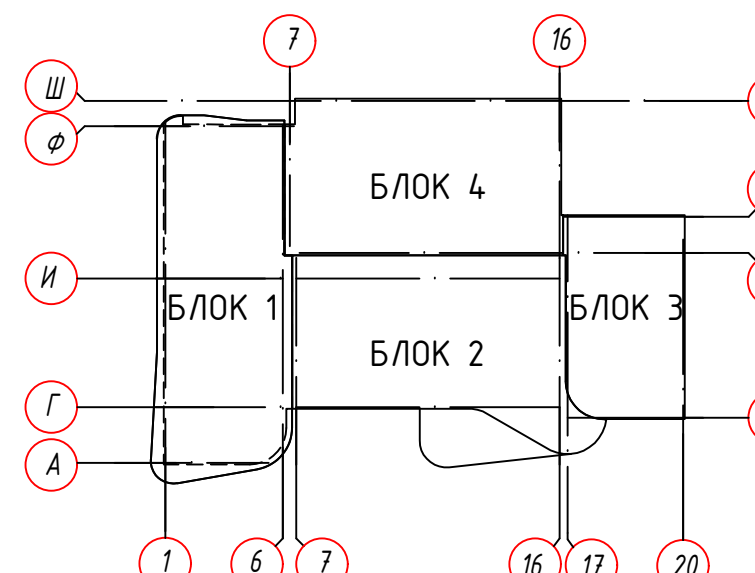

План кондиционирование тех. этажа на отм. +26,640



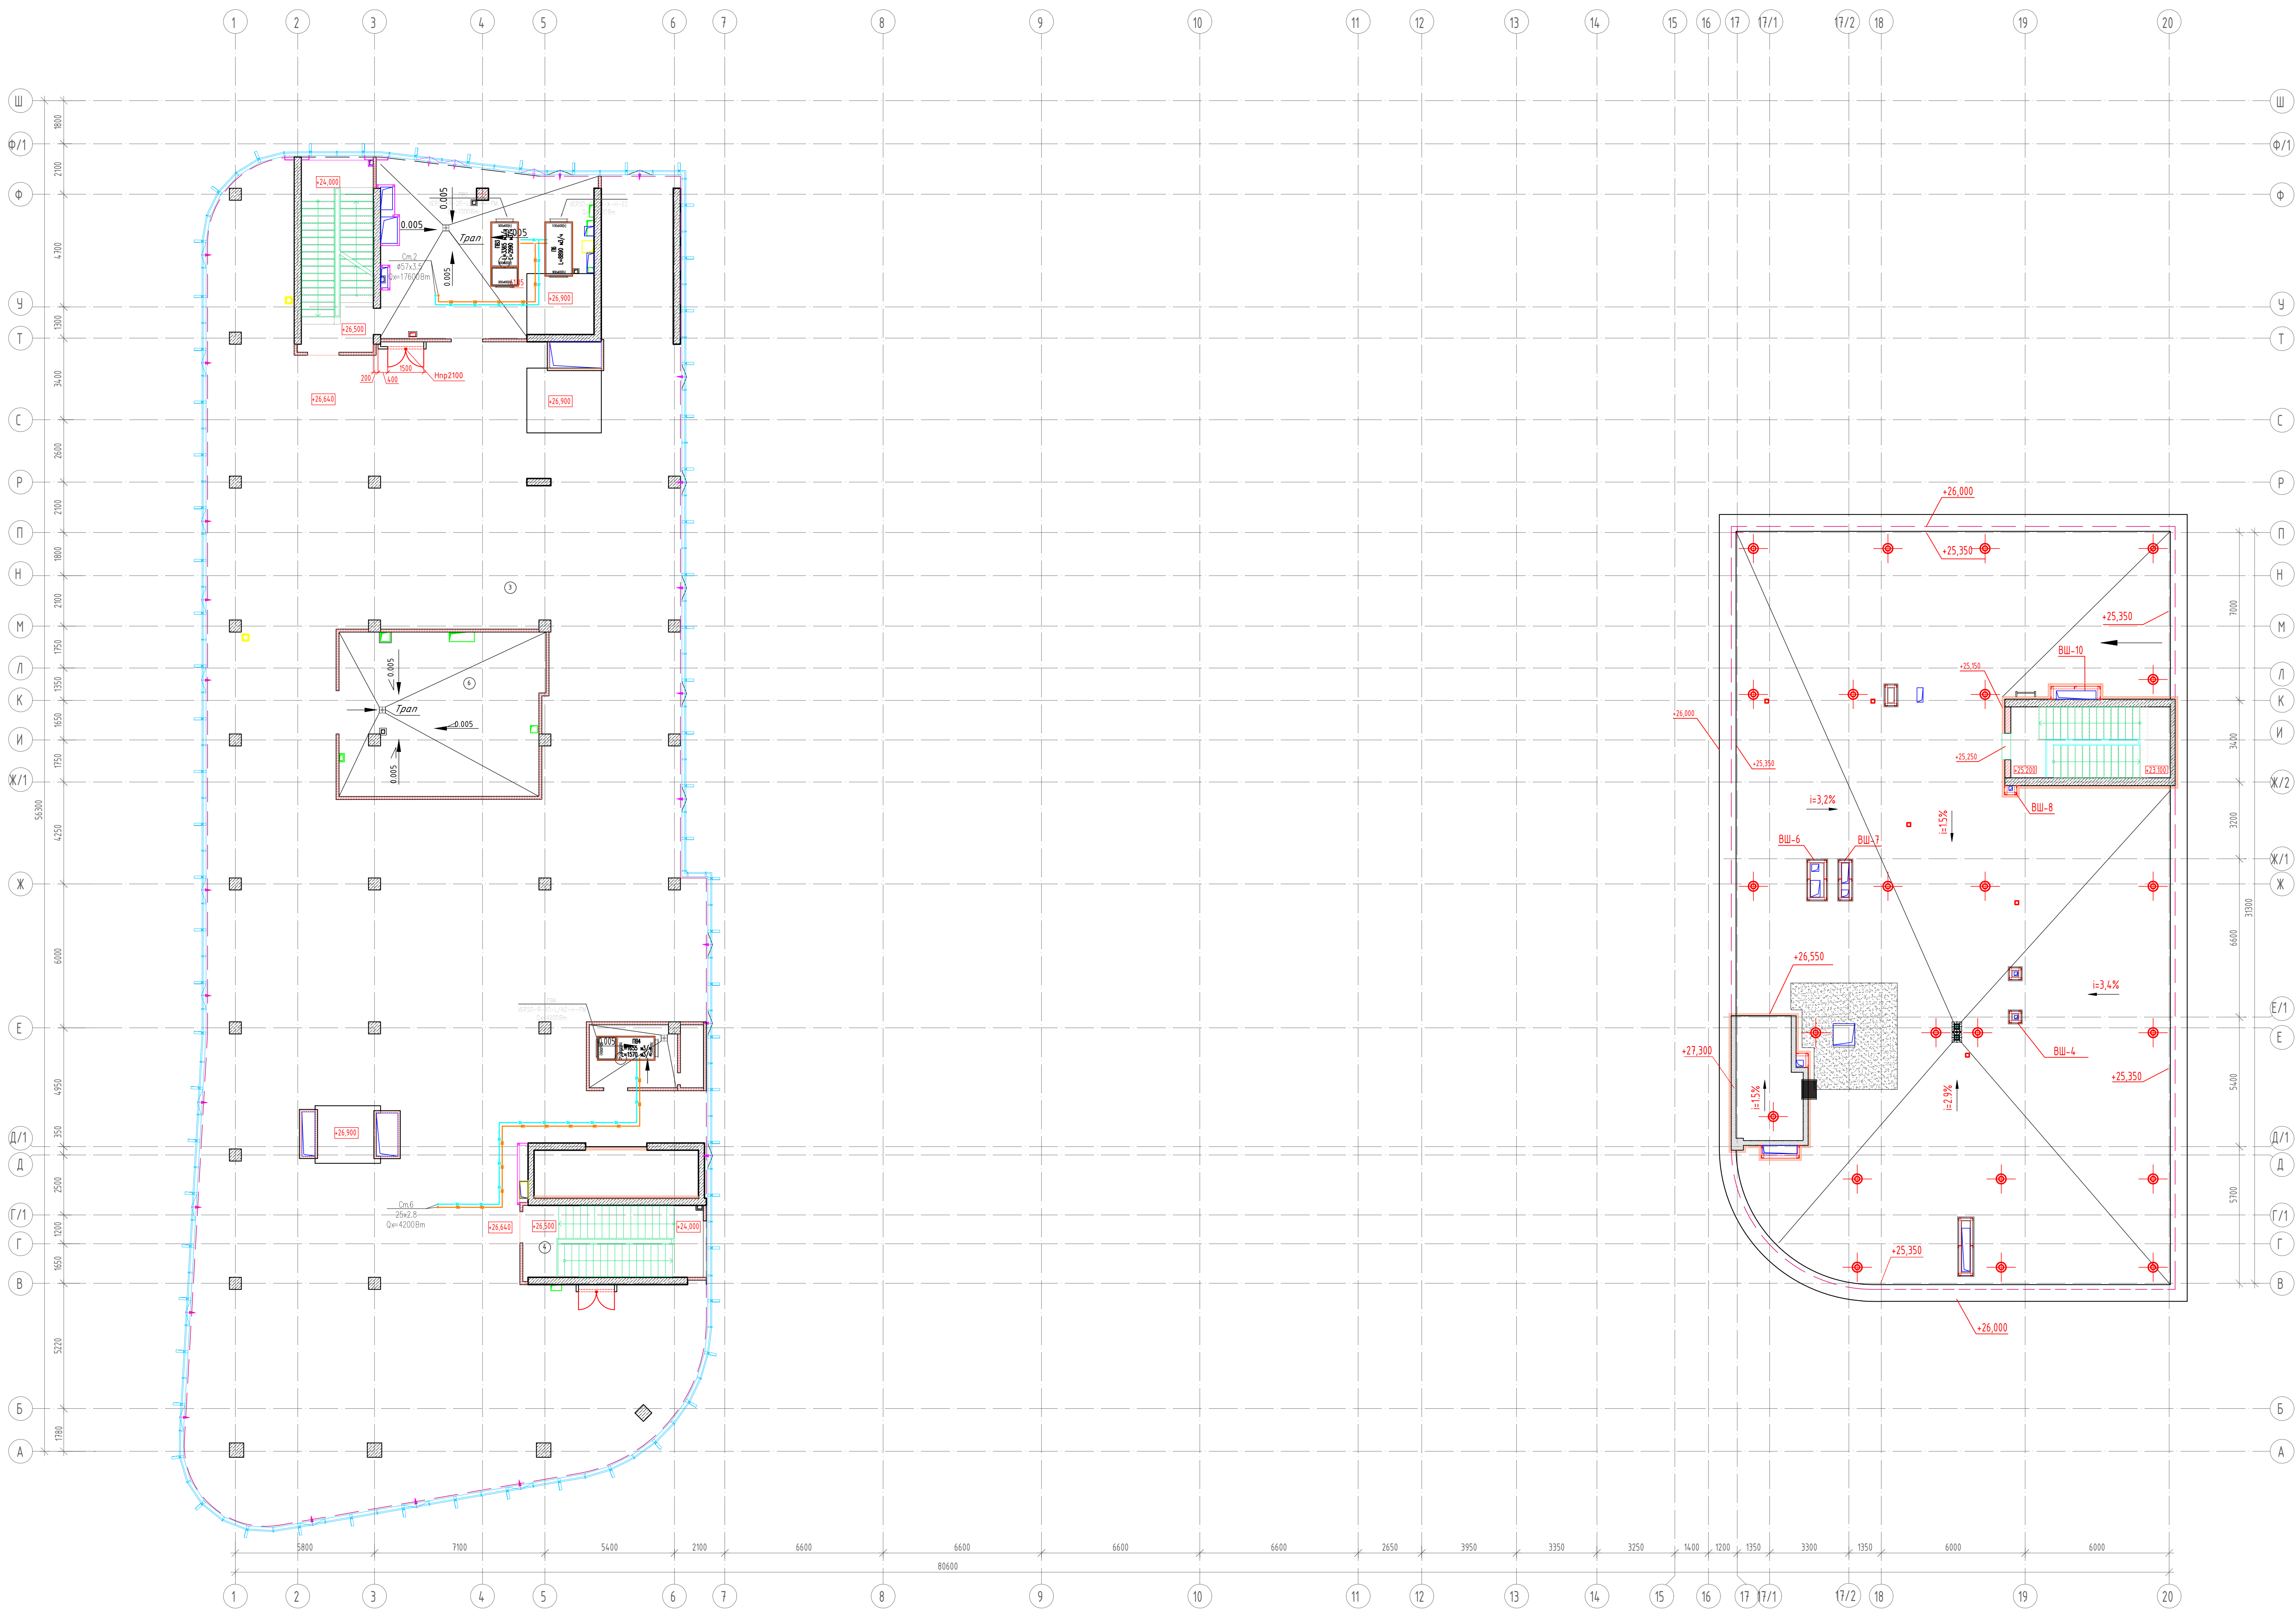


СХЕМА БЛОКИРОВКИ

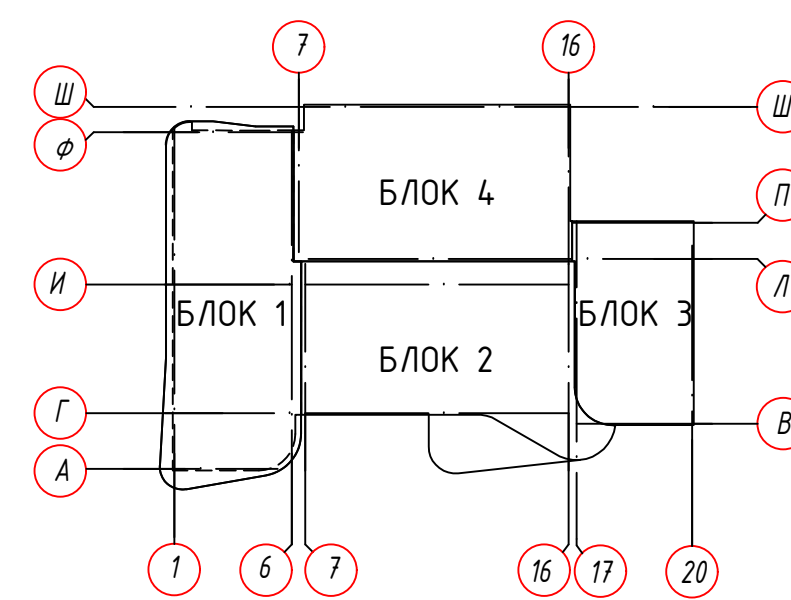

02/09/ФОК-ХС									
Корректировка рабочего проекта "Реализационно-диагностический центр с гостиницей (Физкультурно-оздоровительный комплекс с гостиницей) в г. Алматы, район Сосновка/Жуков-Вн.Телем, 25"									
Изм.	Кол.	И.Вн.	Лист	Подпись	Дата	02.26			
Г/П	Г/П	Г/П	Г/П	Г/П	Г/П	02.26			
Проектировщик						02.26			
Разработчик						02.26			
План кондиционирования кровли на отм. +26,640						100 "Unitary Group"			

План кондиционирование подвала на отм. -4,050

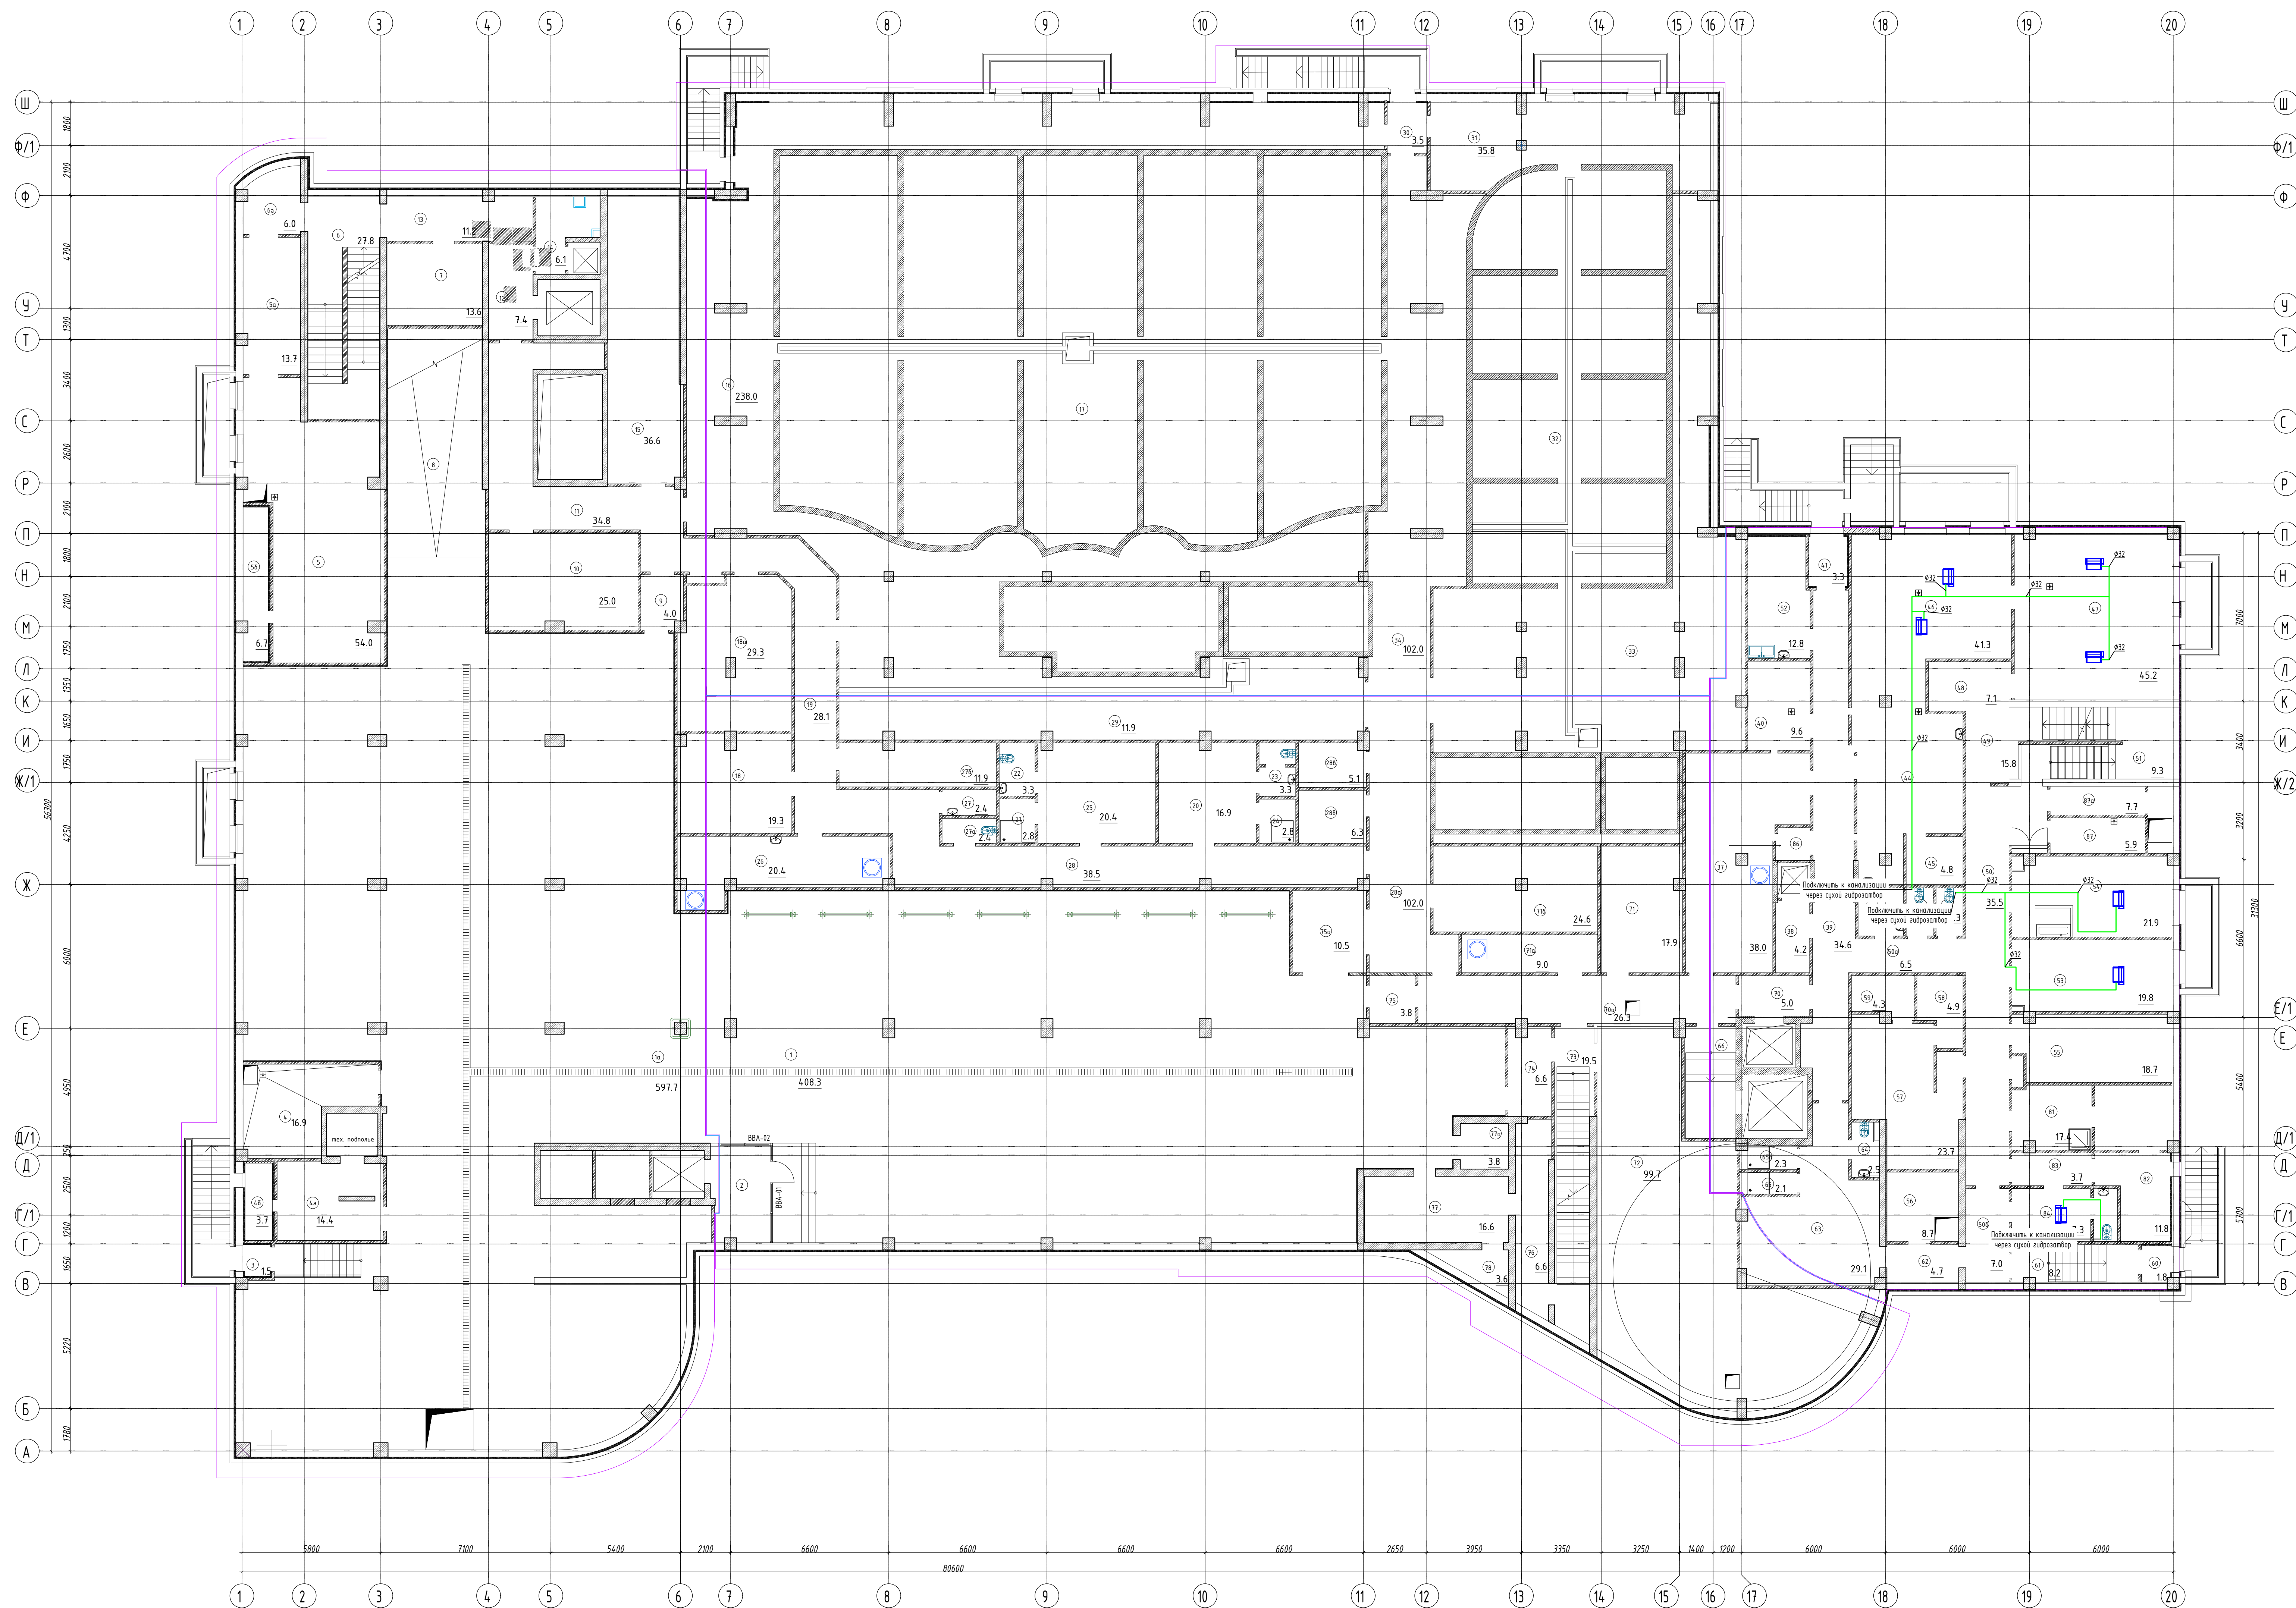


Экспликация помещений:

Поз	Наименование	Площадь, кв. м2	Кол. помещений
1	Парикмах.	483,3	
1а	Парикмах.	597,7	
2	Танцд. с полноразм. базиллю.	9,7	
3	Танцд.	15	
4	Тек. помещение	36,9	
4а	Вензакшени	3,7	
4б	Вензакшени	14,4	
5	Вензакшени	54,8	
5а	Тек. помещение	6,7	
5б	Вензакшени	19,7	
6	Лестничная клетка	278	
6а	Коридор	6,6	
7	Кладовая	3,6	
8	Гимн.	5,9	
9	Танцд. с полноразм. базиллю.	48,9	
10	Секретария	25,0	
11	Коридор	34,8	
12	Танцд. с полноразм. базиллю.	7,4	
13	Коридор	11,2	
14	Детская	3,6	
15	Аудит.	61,1	
16	Тек. помещ.	238,0	
17	Тек. помещ.	385,5	
18	Кладов.	19,3	
18а	Звончатый	23,7	
19	Коридор	38,1	
20	Гардеробная	9,9	
21	Душевая	2,6	
22	Санител.	3,3	
23	Санител.	3,3	
24	Душевая	2,8	
25	Гардеробная	29,4	
26	Пом. для хранения белья	2,4	
27	Пом. уборочного инвентаря	20,4	
27а	Санител.	2,4	
27б	Гардеробная	11,9	
28	Коридор	38,5	
28а	Коридор	102,8	
28б	Хранение резиновых	6,3	
28в	Хранение резиновых	11,9	
29	Узел уборочных бассейнов	51	
30	Танцд.	3,5	
31	Техническое помещ.	35,8	
32	Техническое помещ.	101,1	
33	Узел уборочных бассейнов	112,7	
34	Коридор	102,8	
35	Пом. хранения резины и резиновых вещей	30,6	
38	Танцд. с полноразм.	4,2	
39	Коридор	34,6	
40	Хран. инвент. хранения	9,6	
41	Танцд.	3,3	
43	Санител.	2,3	
43а	Санител.	2,3	
43б	Комната убороч. инвентаря	3,9	


Экспликация помещений

Поз.	Наименование	Площадь, м ²	Кол. ламп, шт.
44	Пок. крыши и разбор арочного беля	26,3	
45	Пок. фронцонного свингерора	4,8	
46	Помещение пестерочной	413	
47	Галлельная	45,2	
48	Помещ-е разборки, укладкой чистого беля	51	
49	Вальцы чистого беля	25,8	
50	Коридор	75,7	
51	Коридор	65	
52	Коридор	70	
53	Лестничная клетка	9,3	
54	Холод. камер хранения мед. отходов	12,9	
55	Ком. отходов и приемо. пункт	99,9	
56	Помещ-е зана	219	
57	Кладовая запасов чистого фибровального беля	87	
58	Кладовая фиброваль. отходов и отходов	8,7	
59	Разделочная измерительная (Умюной)	23,7	
60	Душевая	4,9	
61	Санузел	4,3	
62	Тембур	18	
63	Лестничная	8,2	
64	Коридор	47	
65	Разделочная измерительная (Женской)	21	
66	Санузел	2,5	
67	Душевая	2,1	
68a	Душевая	23	
69	Лифтовый холл	10,0	
70	Тембур с подпорным	56,3	
71a	Коридор	20,0	
72	Носососна АИТ	7,0	
73	Пок. черт. арочного беля	19,0	
74	Носососна	24,8	
75	Носососна, тепловый узел	99,7	
76	Лестничная клетка	99,9	
77	Тембур с подпорным бойцами	6,6	
78	Тембур с подпорным бойцами	6,6	
79a	Тембур с подпорным бойцами	10,5	
80	Тех. подполье	6,6	
81	Тех. подполье	3,8	
82	Тех. подполье	3,6	
83	Пок. крыши и дезинфекции и стерилизации	17,4	
84	Пок. хранения медицинских	118	
85	Санузел, Душевая	3,7	
86	Офис	31	
87	Помещ-е хранения лекарств	19,9	
88	Пок. стерилизации и хранения медицинских	5,9	
89a	Помещение бытовых отходов (Воспек)	7,7	

СХЕМА БЛОКИРОВКИ

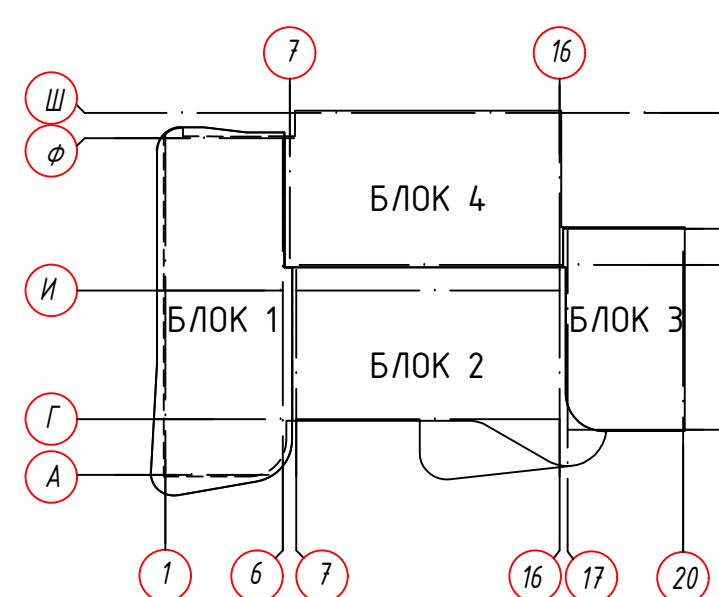


План системы дренажа кондиционирование 1-го этажа на отм. 0,000

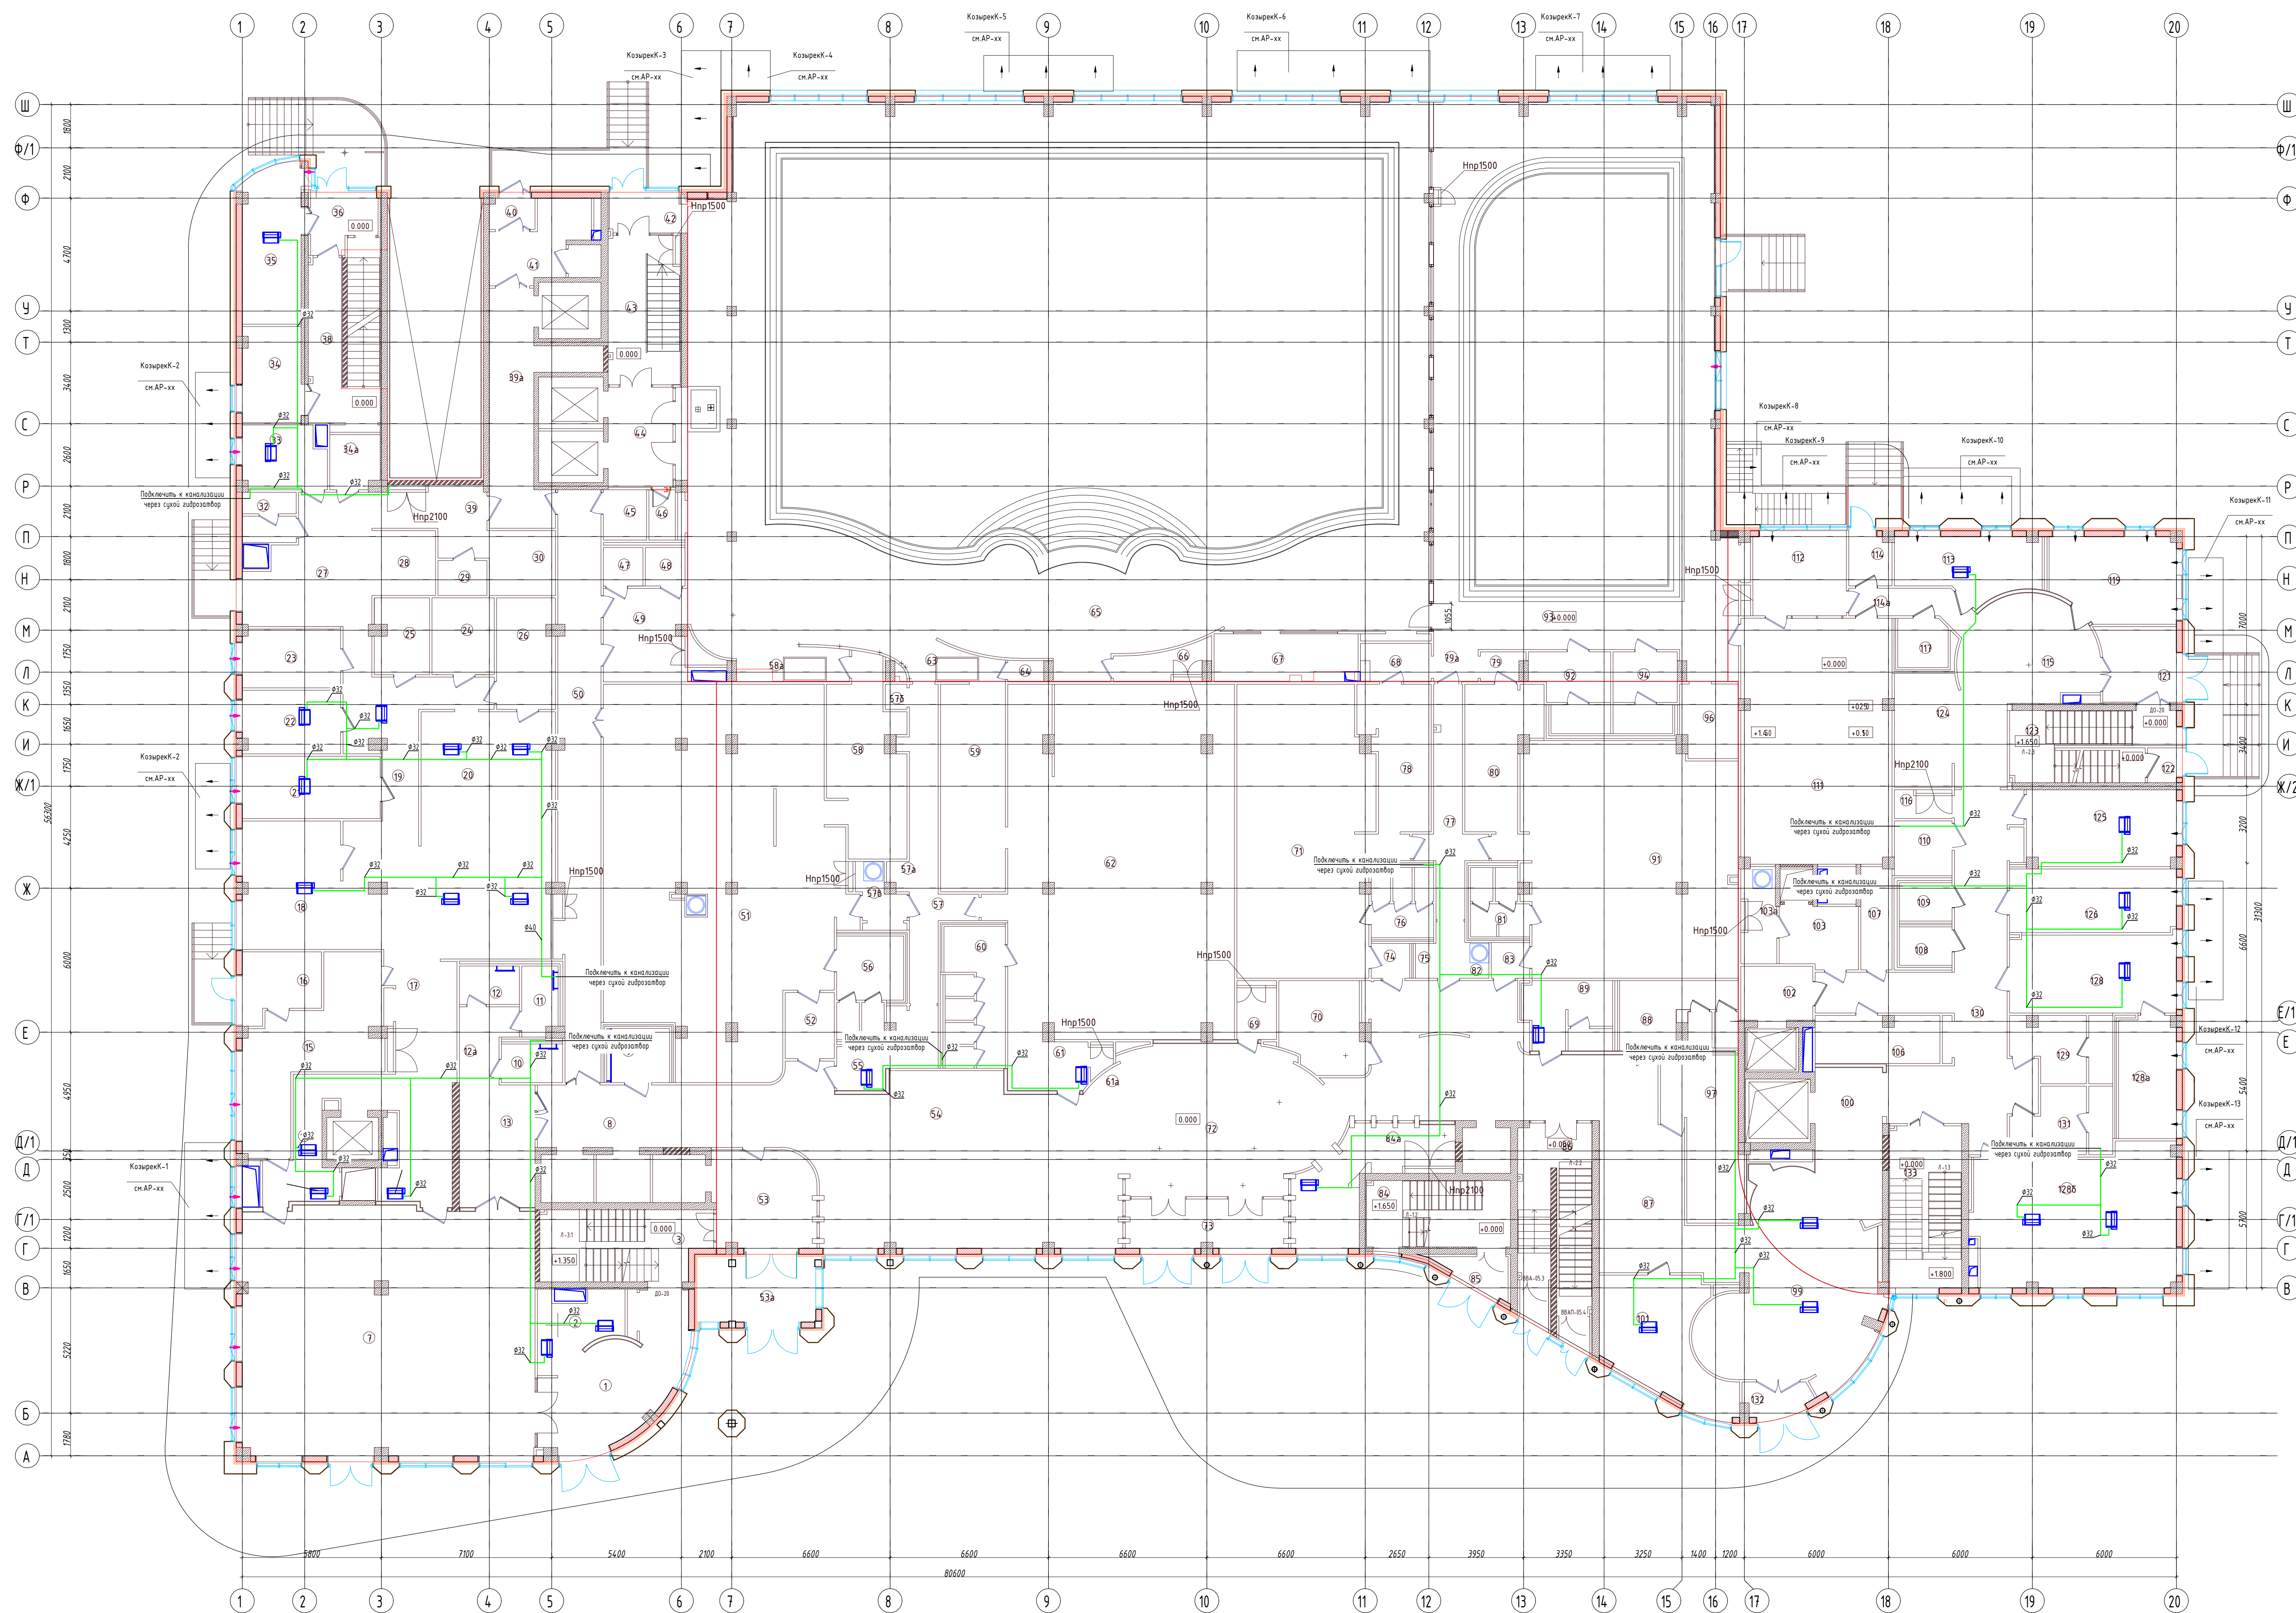


Экспликация помещений (начало)			Экспликация помещений (окончание)				
Поз	Наименование	площадь	Кат. помещ-ния	Поз	Наименование	площадь	Кат. помещ-ния
1	Ресторан	26,0	60	Санузел		15,1	
2	Гардероб	8,9	61	Тамбур		7,5	
3	Лестница	20,3	61а	Подсобное помещение		12	
7	Общедный зал	129,2	62	Раздевалка женская		141,4	
8	Холл	18,8	63	Тамбур		3,9	
9	Санузел МЖ	5,9	64	Тех.помещение		15	
10	Санузел	4,10	65	Восстем		694,3	
11	Санузел	4,2	66	Тех.помещение		5,0	
12	Санузел	4,0	67	Ваня физка		9,3	
13а	Тамбур	6,4	68	Тамбур		4,4	
13	Холл	9,1	69	Подсобное помещение		4,0	
14	Коридор	9,8	70	Охрана		12,7	
15	Помещение столовой посуды	28,0	71	Раздевалка веб.		68,9	
16	Тамбур	8,9	72	Холл		195,9	
17	Раздевалочная	31,7	73	Тамбур		15,0	
18	Холодный цех	22,8	74	Тамбур		2,2	
19	Коридор	20,6	75	Холл		14	
20	Горячий цех	14,4	76	Санузел		7,3	
21	Мясной цех	15,5	78	Тех.помещение		12,1	
22	Рыбный цех	11,1	79	Душевые		15,6	
23	Кладовая	10,4	79а	Тамбур		2,1	
24	Общедный цех	8,2	80	Душевые		2,5	
25	Кладовая одежды	7,1	81	Душевые		16,5	
26	Помещение кураторной посуды	16,1	81	Санузел		6,7	
27	Застывочная	11,2	82	Пом. Бельеяробота		4,1	
28	Холодильная камера	7,2	83	Тамбур		24	
29	Кладовая	10,3	84	Лестница		86,6	
30	Холодильная камера	15	84а	Отдел продаж		19,1	
31	Санузел	4,4	85	Тамбур		19,1	
32	Защ.производством	9,2	86	Лестница		21,1	
33	Гардероб персонала	9,9	87	Коридор		27,5	
34а	Кладовая	4,6	88	Санузел женский		13,4	
35	Помещение охраны	16,0	89	Санузел мужской		10,2	
36	Тамбур	6,3	91	Раздевалка для мальчиков		87,0	
38	Лестница	20,1	92	Тренерская жен.		9,7	
39	Коридор	6,9	93	Восстем детскими		275,4	
39а	Коридор	23,1	94	Тех.помещение муж.		8,7	
40	Тамбур	2,4	96	Ваня Детская		7,3	
41	Застывочная	10,2	97	Гардероб		19,0	
42	Тамбур	5,5	100	Холл		50,8	
43	Лестница	18,4	100	Вестебель		16,2	
44	Ледовый зал	11,3	101	Отдел продаж		22,5	
45	Лобби-холл	3,8	102	Лифтовой холл		6,8	
46	КМ	2,3	103	КМ		8,4	
47	Санузел	2,6	103а	Бельеяробот		5,9	
48	Санузел	2,6	106	Помещение стерилизации мед.инвентаря и промывки, высушивания		10,1	
49	Фитобокс	15,4	107	Тех.помещение		5,5	
50	Коридор	42,9	108	Санузел		3,5	
51	Раздевалка мужская	16,0	109	Санузел		3,5	
52	Тамбур	5,6	110	Санузел МЖМ		6,1	
53	VP Box	115	111	Восстем		54,1	
53а	Тамбур	10,7	112	Раздевалка для эрудирован.		13,9	
54	Бокс	10,7	113	Кабинет врача остеопата		14,6	
55	Коридор	5,5	114	Тамбур		11,0	
55а	КМ	1,8	114а	Тамбур		12,5	
56	Санузел	10,5	115	Холл		22,5	
57	Коридор	15,1	116	КМ		2,9	
57а	КМ	1,0	117	Кабинета матери и ребенка		4,2	
57б	КМ	0,9	118	Пок.эрудированного массажа и гимнастики		18,9	
57с	Пом. Бельеяробота	4,3	121	Тамбур		10,6	
57d	Душевые	20,2	122	Тамбур		2,2	
58а	Тамбур	16,1	123	Лестница		18,6	
59	Душевые	23,4	124	Гардероб		19,9	
			125	Кабинет врача остеопата		20,2	
			126	Кабинет врача переломта		18,7	
			128	Кабинет врача хиатереломта/Резб.лимолаза		23,1	
			128а	Помещение массажа		23,1	
			128б	Помещение электро-физиотерапии		48,9	
			129	Развэд. Мужская с душевой		10,3	
			130	Коридор		55,3	
			131	Развэд. Женская с душевой		10,1	
			132	Тамбур		4,4	
			133	Лестница		20,7	

СХЕМА БЛОКИРОВКИ

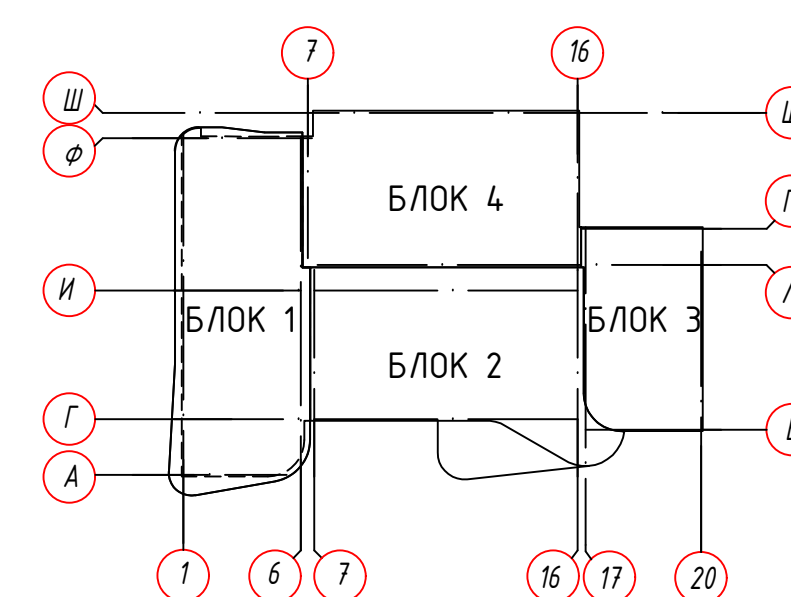


					02/09/ФСК-ХС				
					Корректировка рабочего проекта "Реализационно-диагностический центр с эстетичной (Физкультурно-оздоровительный комплекс с эстетичной) город Астана, район Сельма Хуцетин в/а Тала, аз № 25"				
Изм.	Кол.	№	Действ.	Подпись	Дата	Физкультурно-оздоровительный комплекс			
Гип			Гальмашев		02.26	(Вклады 1, 2, 3, 4)			
Проверил					02.26	РП	15	•	
Разработчик					02.26				
План системы дренажа кондиционирования						ТОО "Vitality Group"			
1-го этажа на сумму 0,000									

План системы дренажа кондиционирование тех. этажа на отм. +4,200

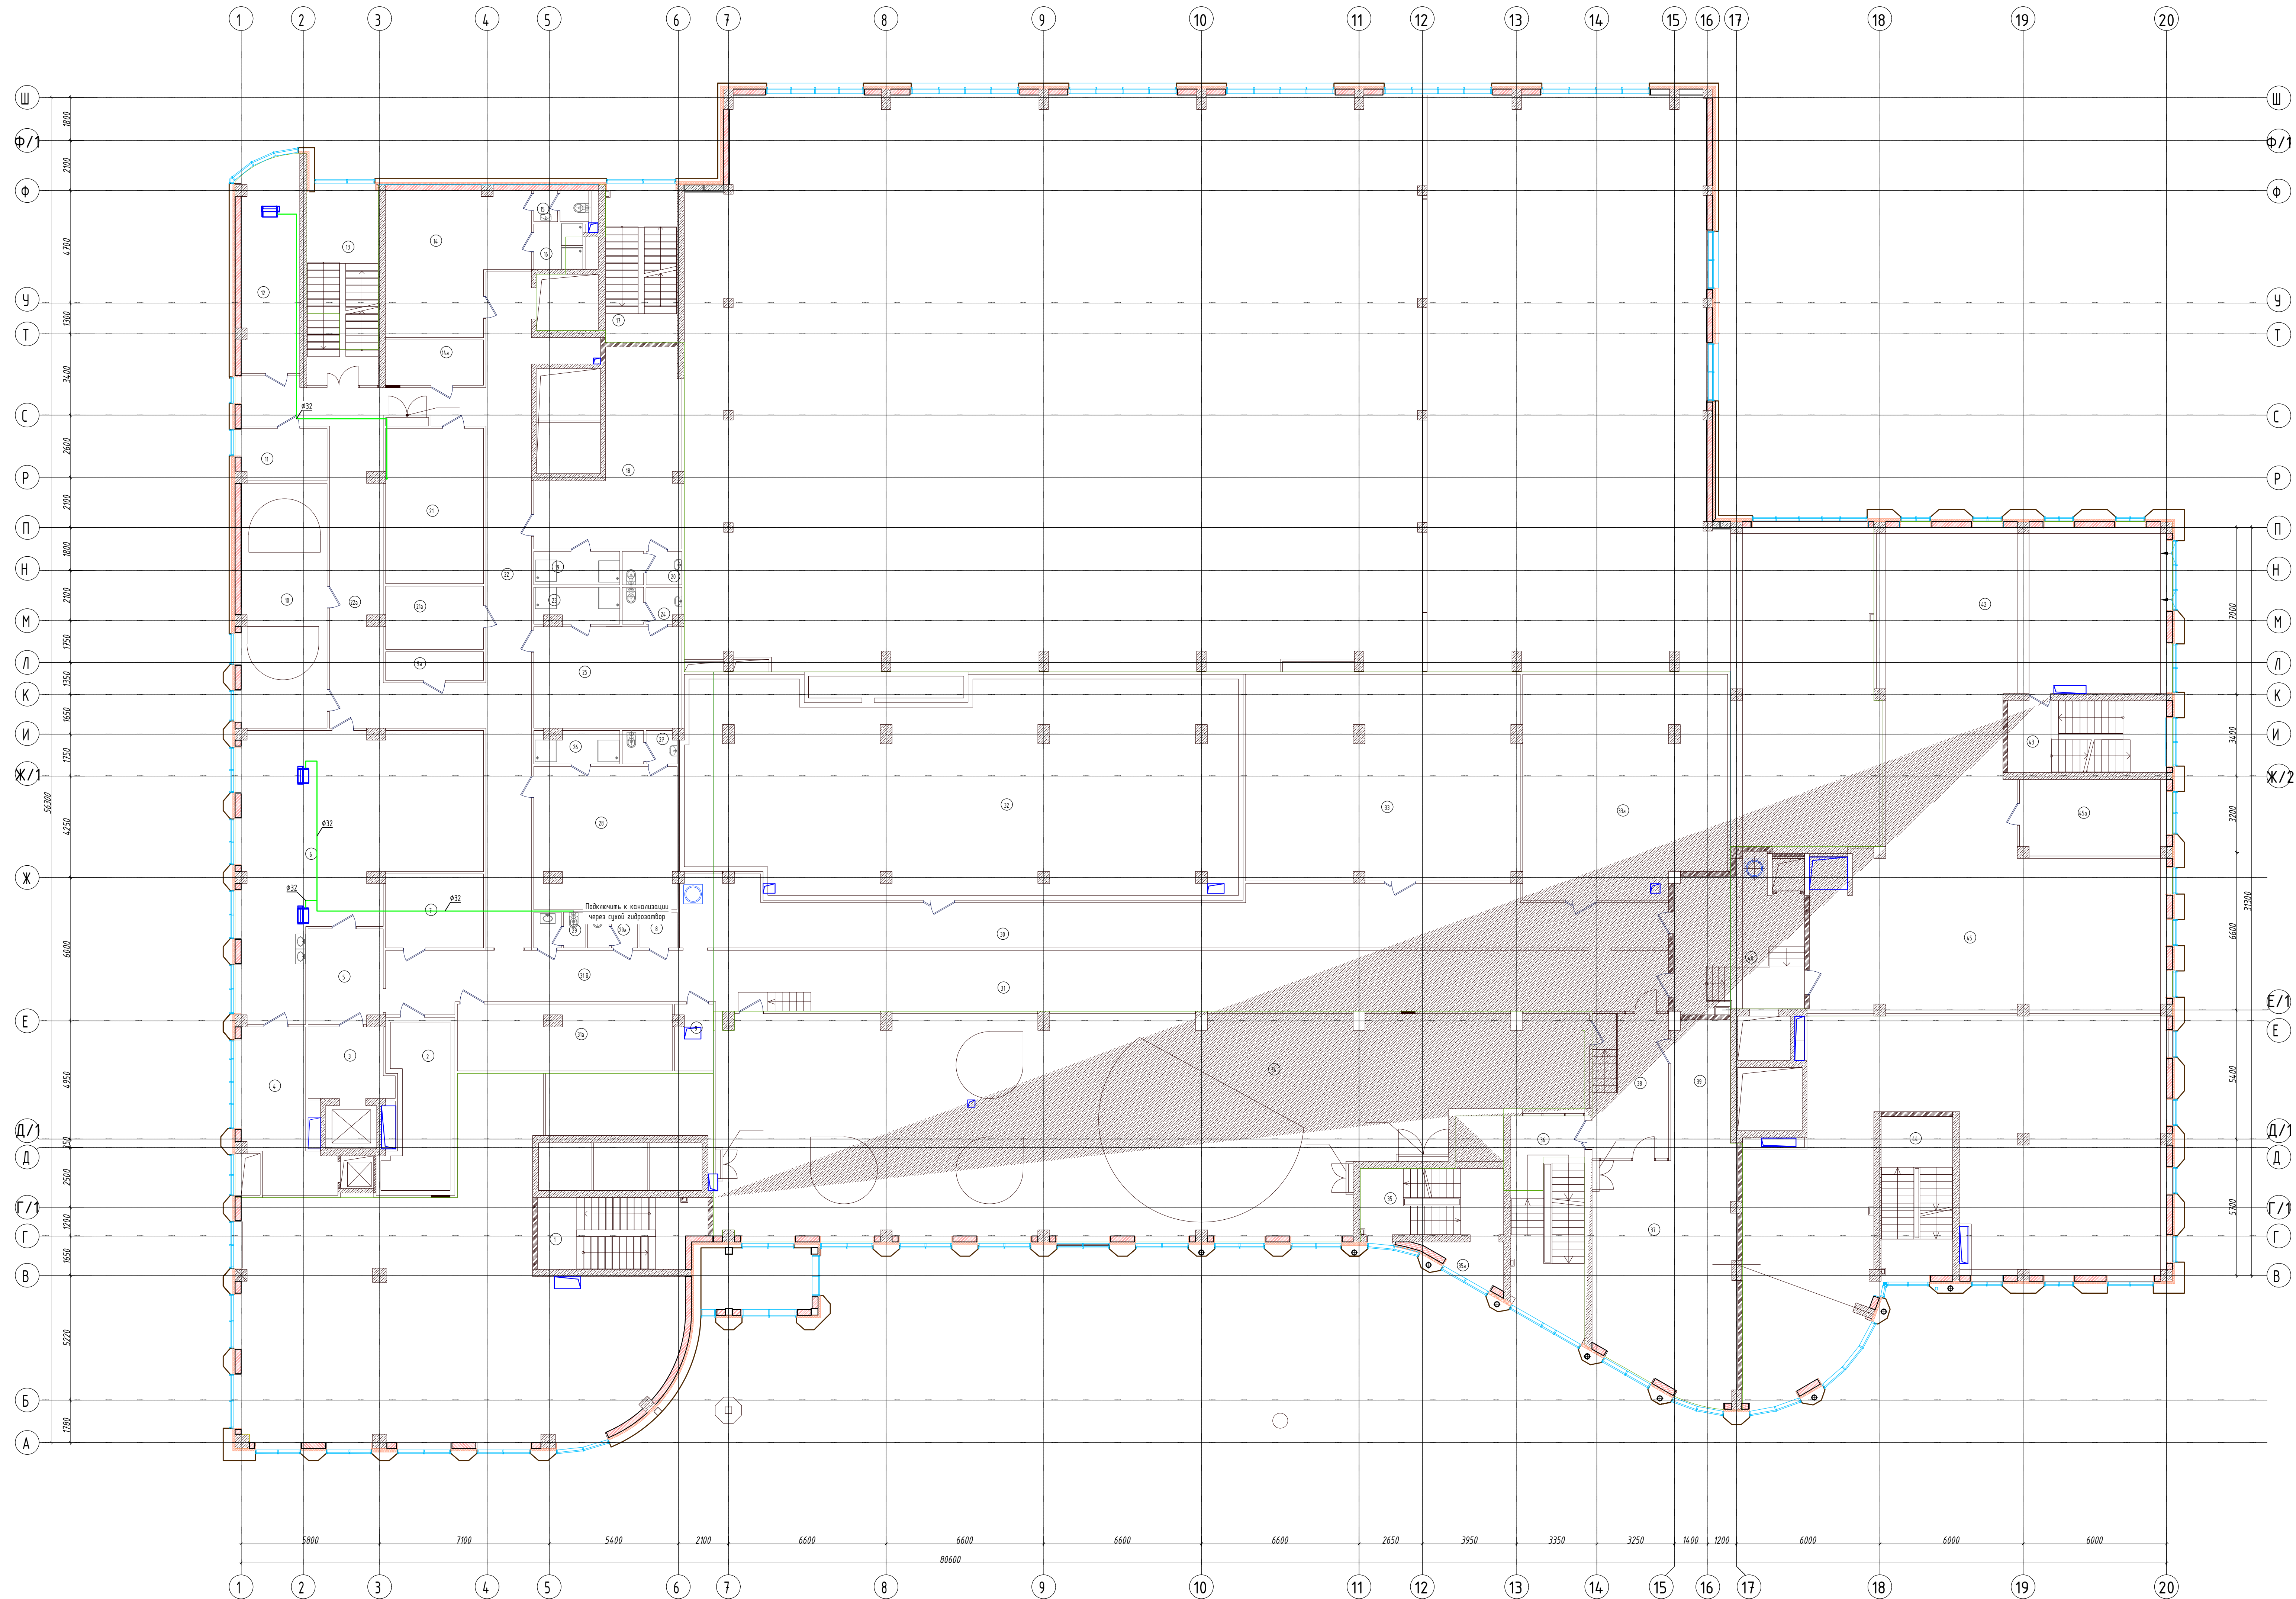


Экспликация помещений			
Поз	Наименование	площадь	Кат. помеще-ния
1	Лестничная клетка	20.1	
2	Ванная	20.6	
3	Сервировочная	9.9	
4	Моечная	20.9	
5	Сервировочная	12.3	
6	Столовая персонала	86.1	
7	Пан. Официантов	12.70	
8	Тех. помещение	2.3	
9	Кухня	4.30	
9а	Тех. помещение	4.9	
10	Тех. помещение	37.60	
11	Тех. помещение	8.20	
12	Диспетчерская	21.7	
13	Лестничная клетка	25.2	
14	Гардеробная	31.70	
14а	Курительная	7.80	
15	Санузел	2.9	
16	Душевая	3.80	
17	Лестничная клетка	19.9	
18	Гардеробная	35.1	
19	Душевая	19.9	
20	Санузел	3.4	
21	Капота тренинга персонала	56.0	
22	Коридор	53.8	
22а	Коридор	52.70	
23	Душевая	53	
24	Санузел	3.6	
25	Гардеробная	26.40	
26	Душевая	24.00	
27	Санузел	3.1	
28	Гардеробная	35.9	
29	Санузел	3.2	
29а	Санузел	3.1	
30	Коридор	91.7	
31	Коридор	91.9	
31а	Цех бытового	25.20	
31б	Коридор	31.1	
32	Ванная	210.4	
33	Тех. помещение	98.9	
33а	Тех. помещение	78.20	
34	Тех. помещение	299.70	
35	Лестничная клетка	16.60	
35а	Лоджия	4.5	
36	Лестничная клетка	27.1	
37	Тех. помещение	55.1	
38	Коридор	19.4	
39	Тех. помещение	14.8	
40	Лоджия холл	31.20	
42	Тех. помещение	98.7	
43	Лестничная клетка	19.56	
44	Лестничная клетка	19.51	
45	Тех. помещение	112.4	
45а	Кроссовая	19.90	

СХЕМА БЛОКИРОВКИ

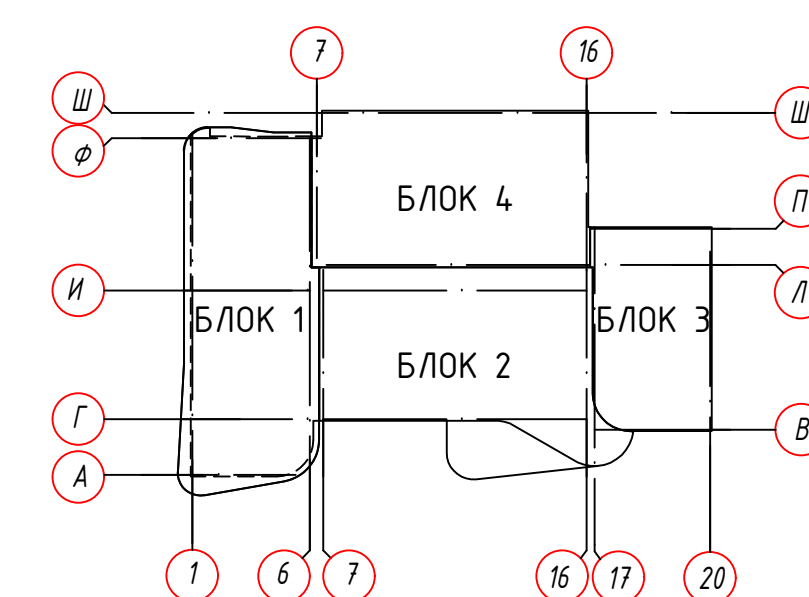


--	--	

План системы дренажа кондиционирование 2-го этажа на отм. +7,350

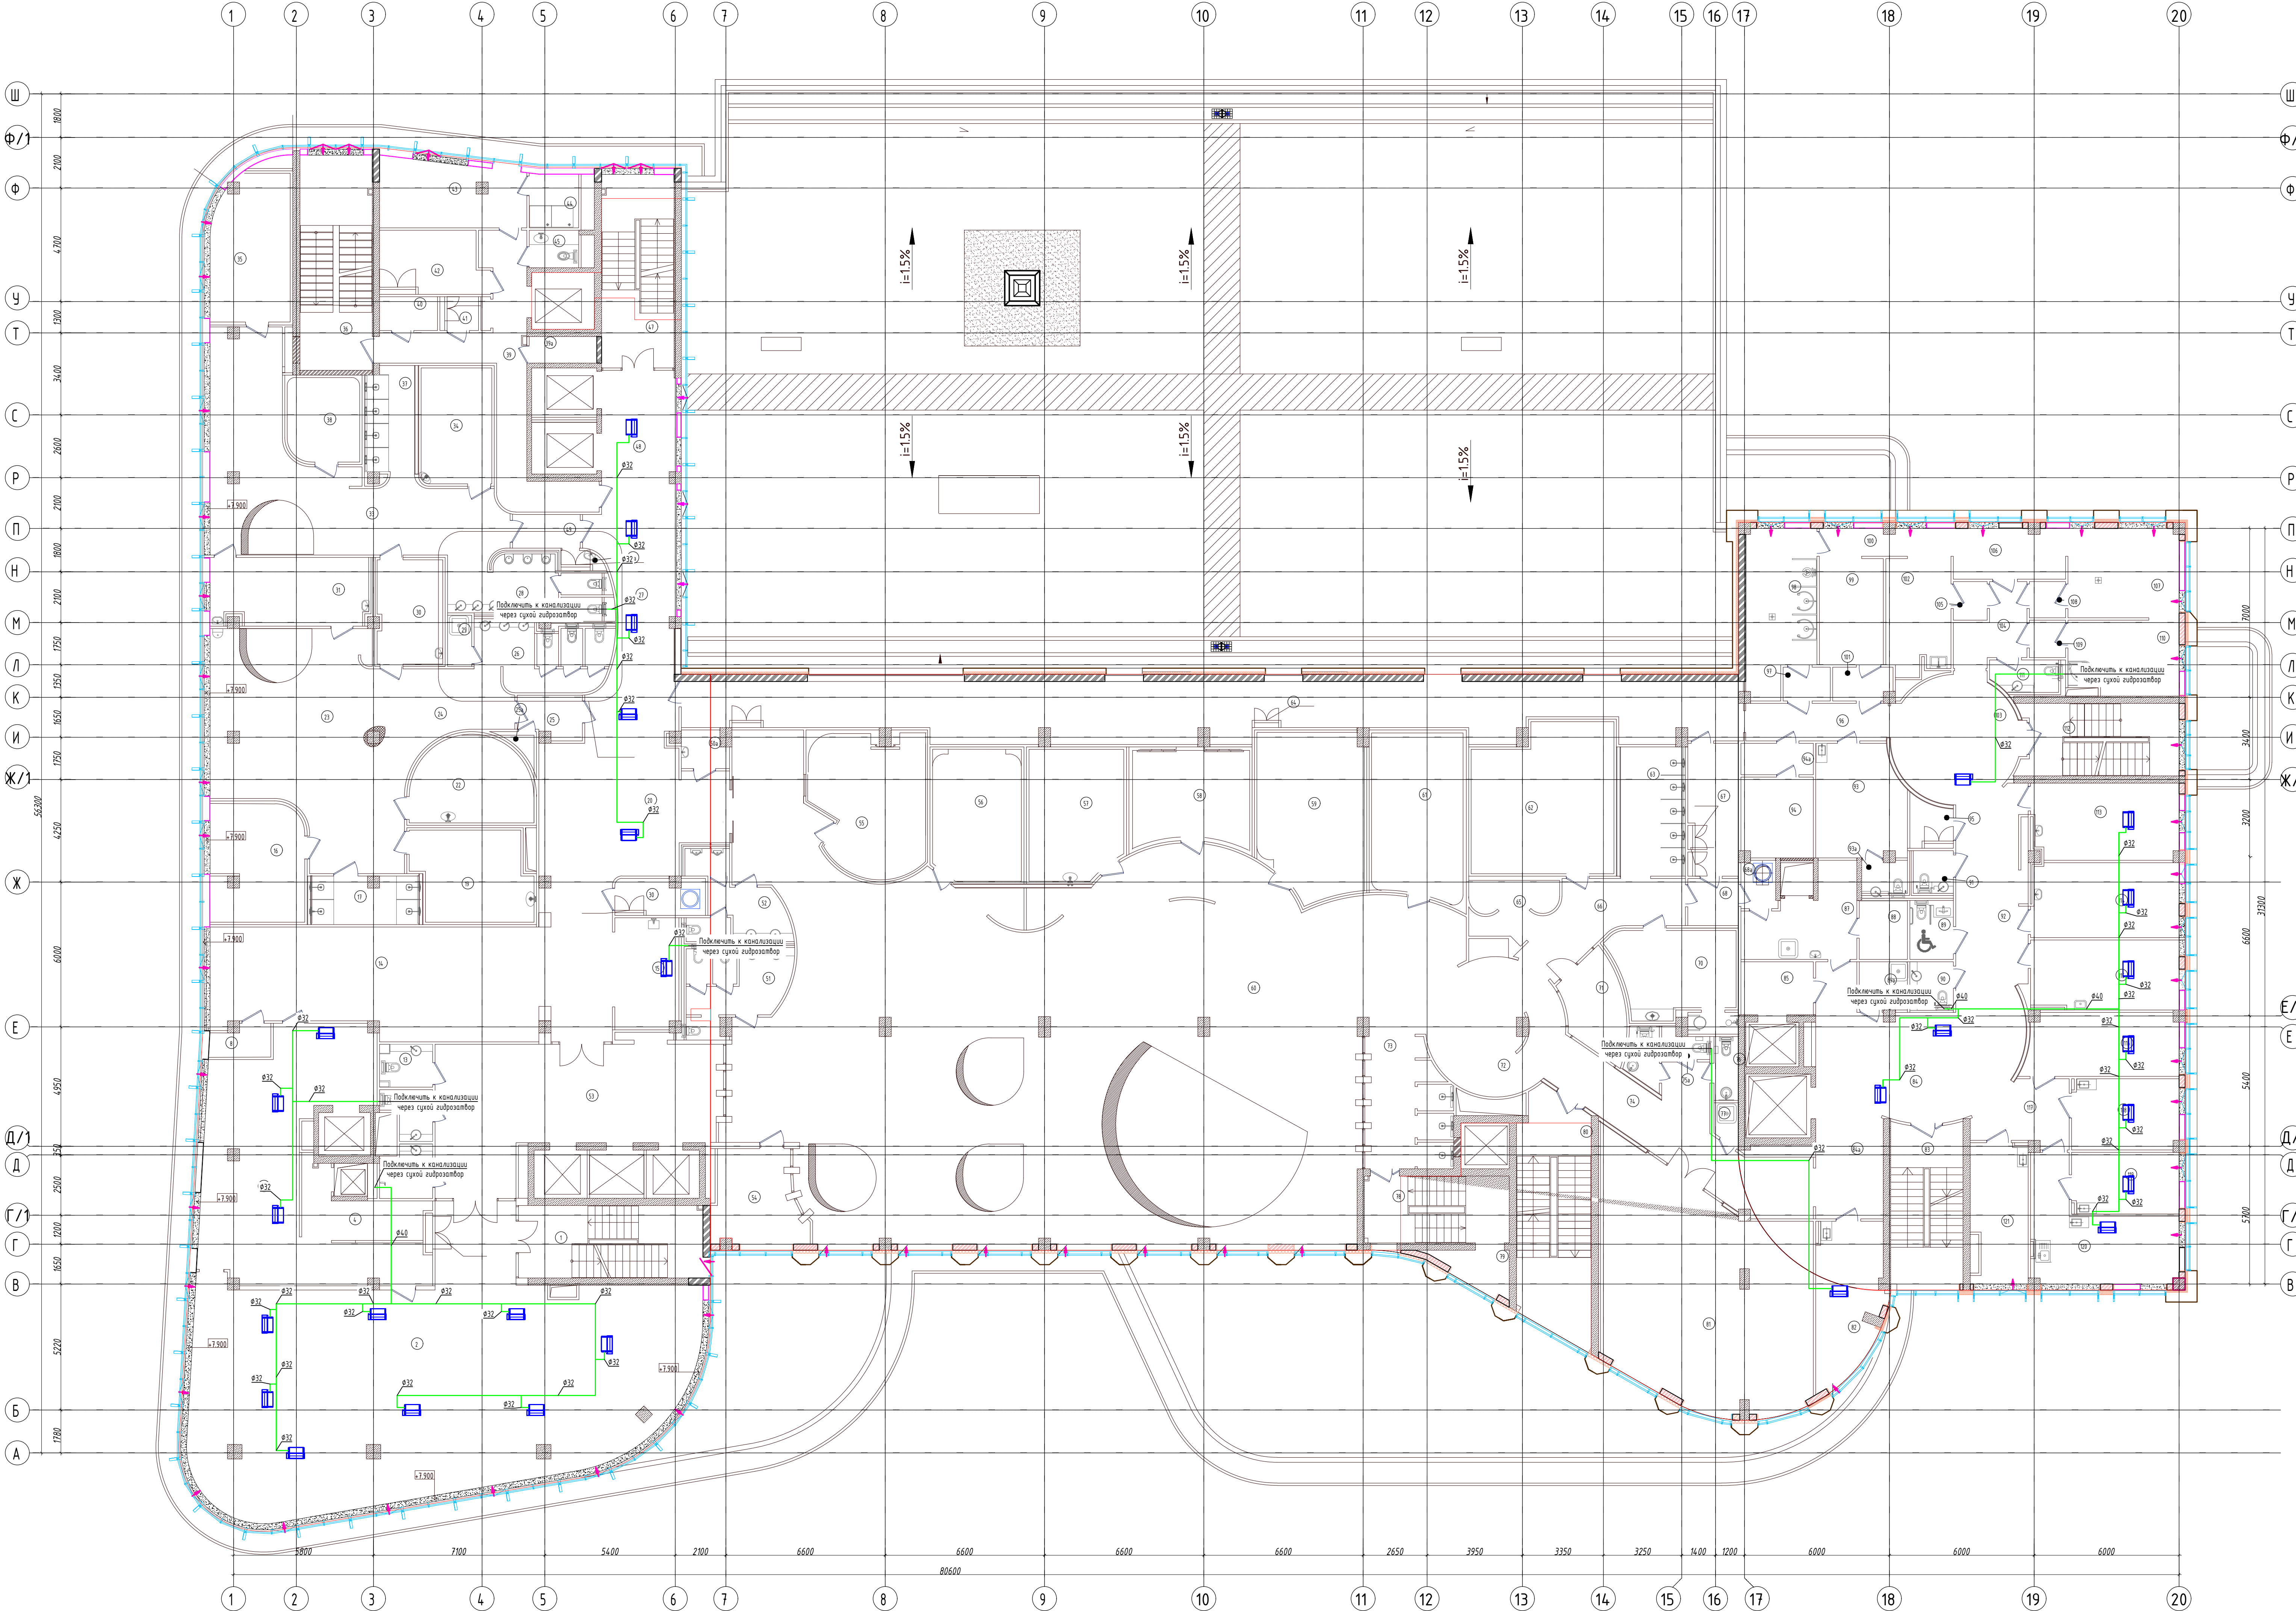


Поз	Экспликация помещений (начало)			Экспликация помещений (окончание)			
	Наименование	площадь	Код, помеще-ния	Поз	Наименование	Площадь	Код, помеще-ния
1	Лестничная клетка	22.5		83	Лестница	19.4	
2	Ресторан	183.25		84	Холл	6.7	
4	Центр гравировальной, чистки и сортировки посуды	10.32		84а	Коридор	11.81	
7	Договорная-сервировочная бара	51.93		85	Лифтовой холл	6.39	
8	Капота для курения	2.94		87	К/И	41.32	
11	Санузел	4.3		88	Холл. Камеры временного хранения отбойки	4.7	
12	Санузел	3.49		89	Санузел ММ Г Н	4.22	
13	Санузел	3.76		89а	К/И	13.42	
14	Зона фито бара	59.96		90	Санузел	3.12	
15	Што бар	12.35		91	Санузел	2.8	
16	Русская баня	18.4		92	Коридор	22.3	
17	Душевая	8.44		93	Процедурный кабинет гидрокопроктологии с гигиеническим душем	16.44	
19	Персон. Хатан-палаточная	17.26		93а	Санузел	2.42	
20	Рестепан	55.21		94	Тех помещение	9.68	
22	Хатан	16.14		94а	К/И	3.73	
23	Женское отделение	63.37		95	Кладовая хранения чистого белья	2.81	
24	Коридор	16.66		96	Коридор	9.32	
25	Коридор	3.65		97	Раздевальня посетелей	3.19	
25а	К/И	1.09		99	Душ ваши	10.31	
26	Санузел	13.52		99	Душ ваши	11.62	
27	Холл	32.6		100	Коридор	5.87	
28	Санузел	12.7		101	Раздевальня посетелей	3.19	
29	К/И	2		102	Таласотерапия	12.36	
30	Индивидуальное парение	11.61		103	Холл	22.94	
31	Пилана	9.04		104	Коридор	7.42	
32	Пилана	8.25		105	Раздевальня посетелей	2.12	
33	Мужское отделение	56.87		106	Помещение обслуживающего персонала	9.67	
34	Персон. Хатан-палаточная	14.03		107	Кабинет гидромассажа	16.8	
35	Сауна	19.09		108	Раздевальня посетелей	2.13	
36	Лестница	26.26		109	Раздевальня посетелей	2.2	
37	Душевые	9.49		110	Кабинет гидромассажа	13.57	
38	Хатан	10.24		111	Санузел	3.47	
39	Коридор	25.05		112	Лестница	18.82	
39а	Тех. Помещение	2.92		113	Кабинет врача проктолога	18.65	
40	Капота складов мойки	3.21		114	Процедурный кабинет аппаратной пералейческой коррекции (вспуркция)	18.39	
41	Оборуд. Хатан	1.31		115	Процедурный кабинет косметологии лица и депиция волос	17.17	
42	Тех. Помещение	10.45		116	Процедурный кабинет аппаратной пералейческой коррекции (криолитолия)	16	
43	Помещение персонала	15.76		117	Коридор	9.37	
44	Душевая	4.37		118	Кабинет врачей-косметологов	12.62	
45	Санузел	3.04		119	Процедурный кабинет массажа	10.96	
47	Лестница	23.6		120	Процедурный кабинет обертывания/уменьшения	20.67	
48	Холл	14.26		121	Криосауна	12.75	
49	Коридор	3.76					
49а	К/И	0.94					
50	К/И	5.02					
50а	К/И	2.78					
51	Санузел X	12.17					
52	Санузел M	10.15					
53	Холл	15.18					
54	Баня парная	13.03					
55	Баня хамам	25.68					
56	Баня аромо-фруктовая	19.73					
57	Хатан	20.56					
58	Баня каменная	18.2					
59	Баня русская можжевеловая	28.35					
60	Зал	410.35					
61	Баня финская	25.58					
62	Баня общая	34.43					
63	Душ	14.23					
64	Коридор	92.33					
65	Душ	7.51					
66	Коридор	15.45					
67	Тех. Помещение ваши	10.59					
68	Танцзал	3.94					
69а	Помещение бельгюродова	2.73					
70	Индивиду. парение (2 стола)	18.51					
71	снежная комната	8.86					
72	Холл	27.48					
73	Душевые	15.98					
74	Коридор	29.93					
75	Санузел	2.98					
75а	Санузел	2.02					
76	Санузел	2.55					
77	К/И	1.53					
78	Лестница	16.25					
79	Танцзал	3.61					
80	Лестница	28.83					
81	Снежная комната-Танцзалище	76.28					
81	Кабинет фито- и ароматерапии	16.28					

СХЕМА БЛОКИРОВКИ

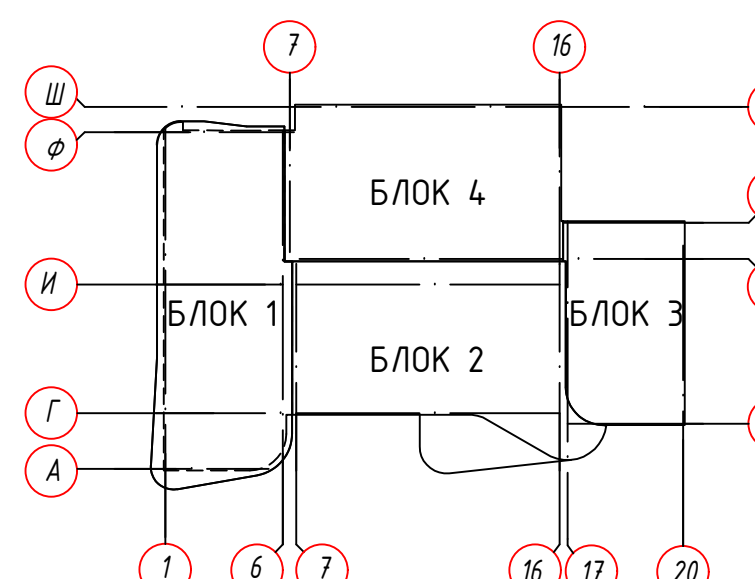


					02/09/ФПК-ХС				
					Корректировка рабочего проекта "Реабилитационно-диагностический центр с эскапией (физкультурно-оздоровительный комплекс с эскапией) город Астана, район Есильби Хусейн бен Талат, д/м 25"				
Изм.	Кол.	Изм.	Лист	Подпись	Дата	Физкультурно-оздоровительный комплекс			
ГП			Галимжанов		02.26	Эскапий			
Проверил					02.26	Склад	Листов		
Разработал					02.26	РП	17	•	
План системы дренажа кондиционирования 2-го этажа на опм. +7,350						ТОО "Vitality Group"			

План системы дренажа кондиционирование 3-го этажа на отм. +12.000

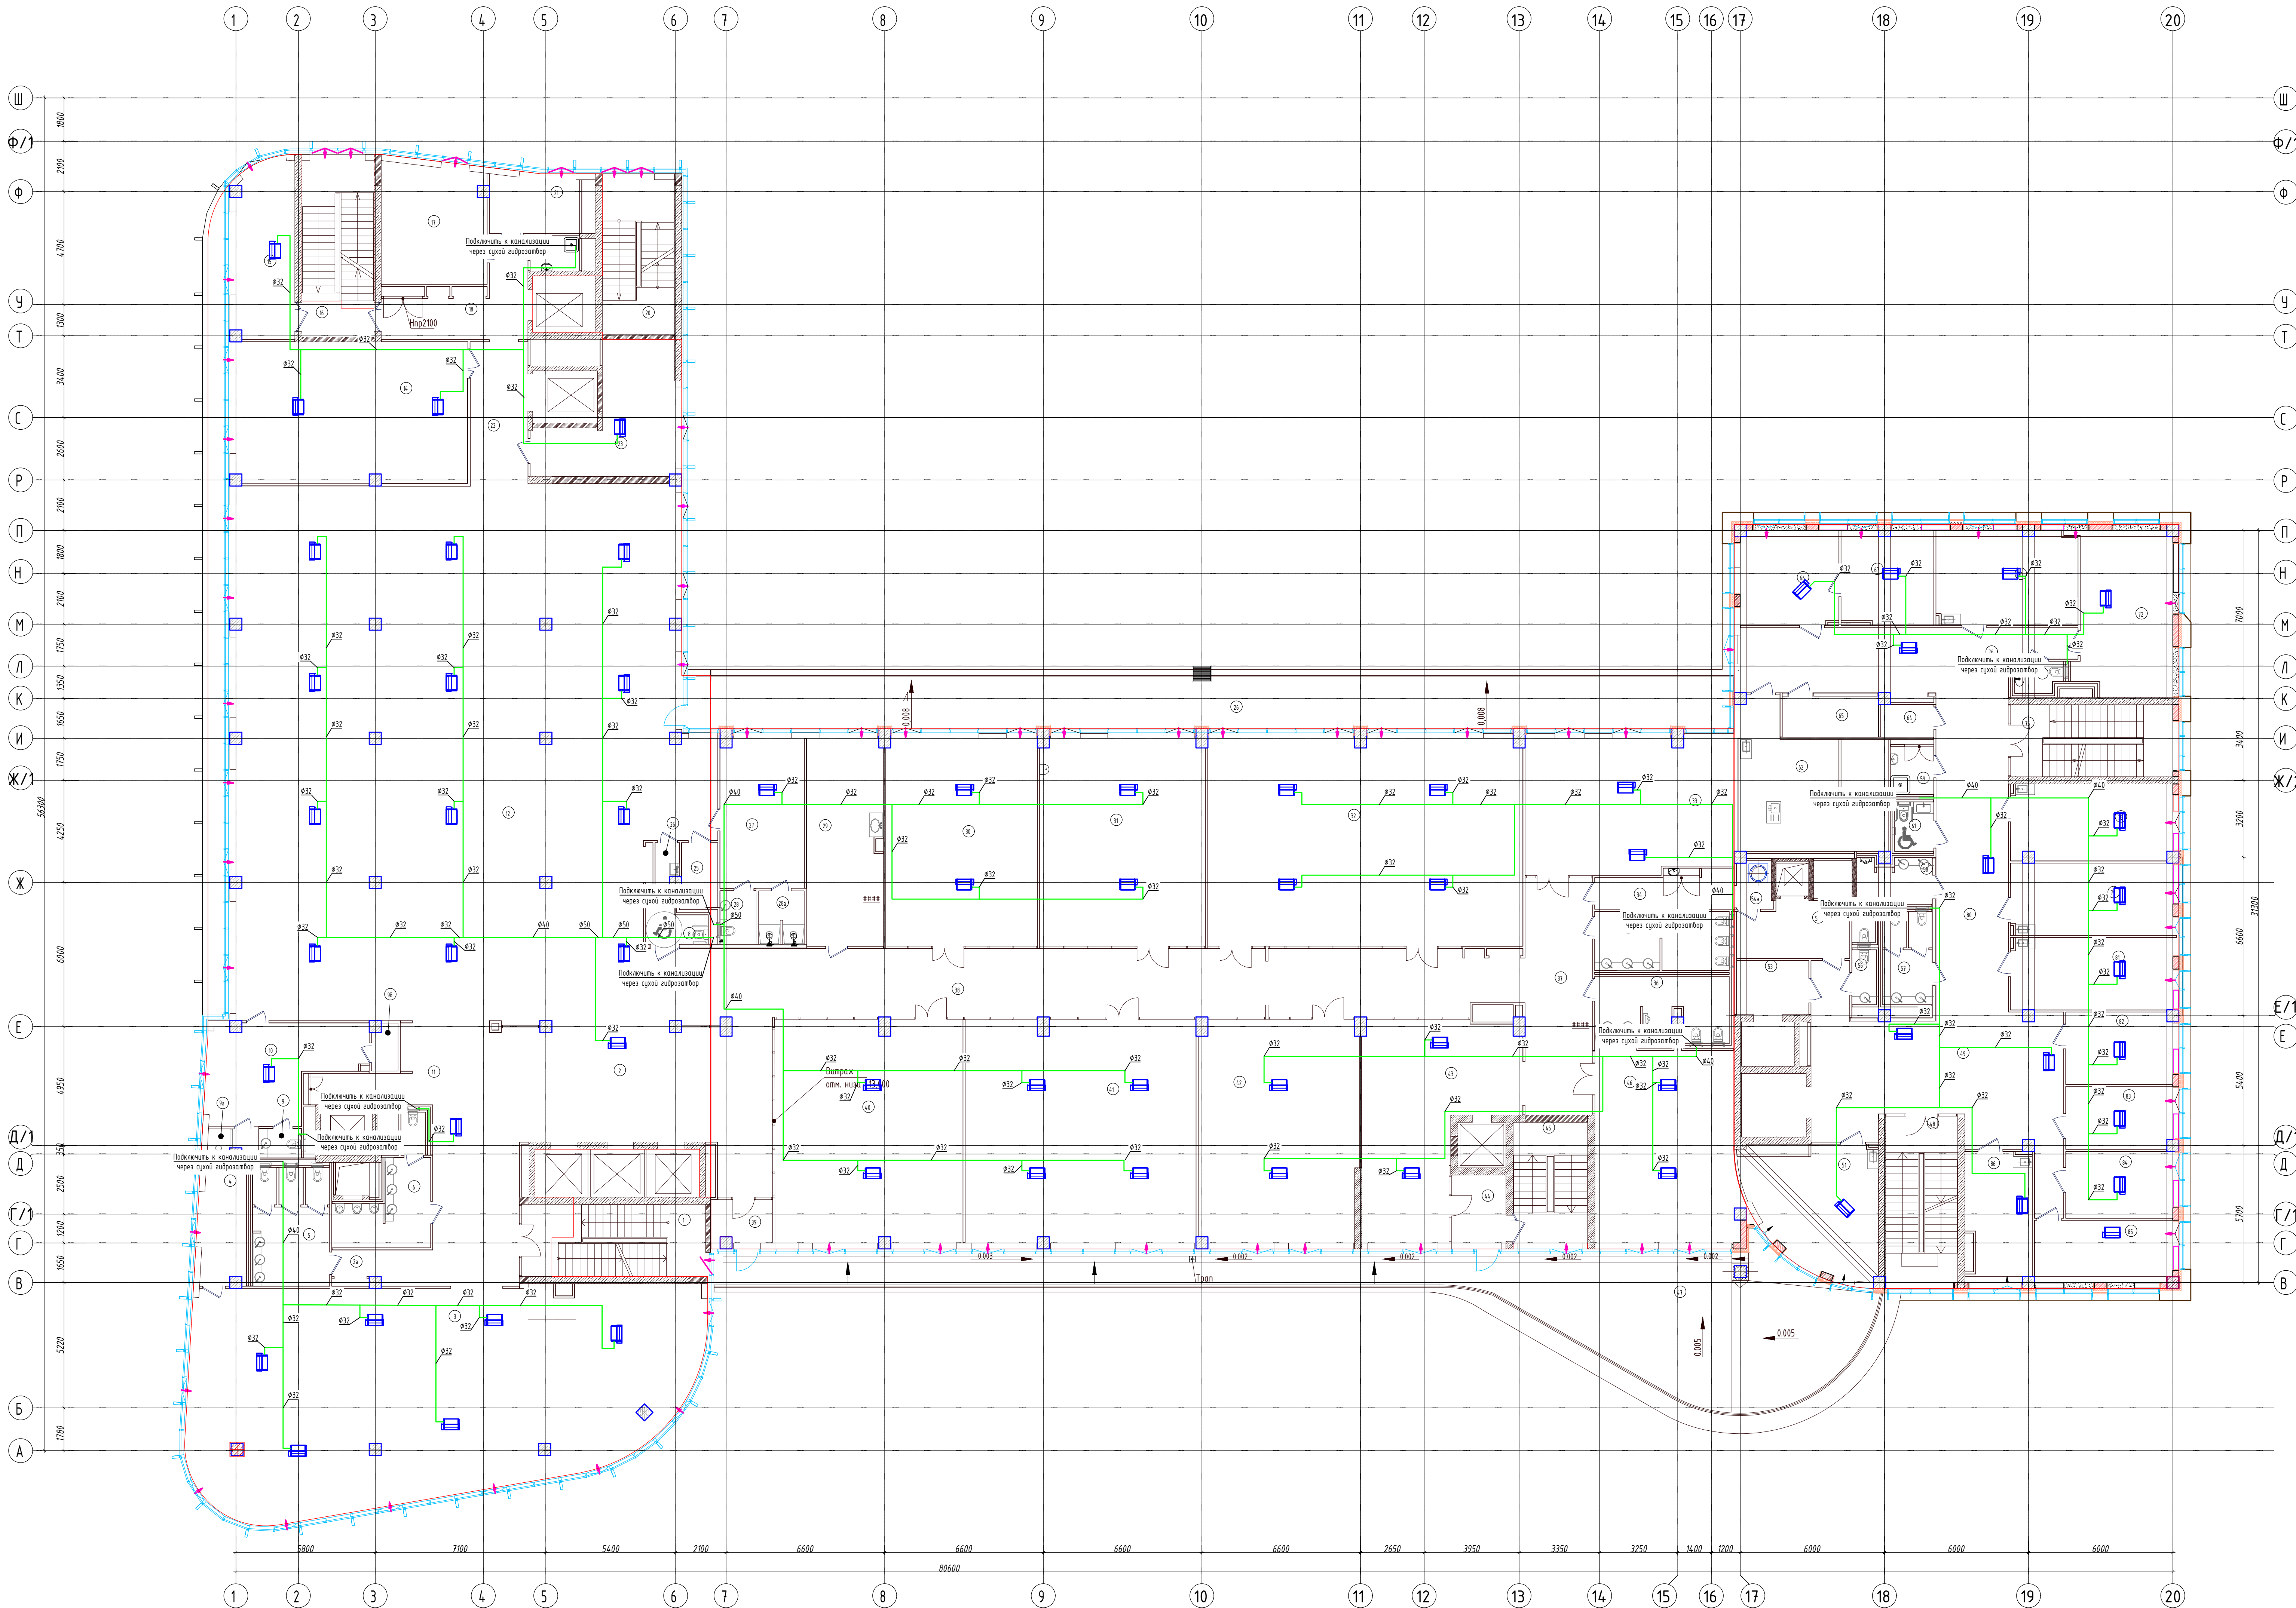


Паз.	Экспликация помещений		Кат. номерация
	Наименование	площадь	
1	Лестничная и клетка	231	
2	Холл	68,6	
2а	Коридор	271	
3	Зона кардио-тренировок	178,6	
4	Зал персонального тренера	9,80	
5	Санузлы X	14,92	
6	Санузлы М	12,61	
8	Санузел	4,2	
9	Санузел	2,2	
9а	Душевая	2,2	
9б	Душевая	2,2	
10	Тренерская М	22,1	
11	Фитобар	13,4	
12	Тренажерный зал	426,4	
14	Сейл студия	51,9	
15	Кабинет менеджера	11,7	
16	Лестница	16,28	
17	Тех. помещение	21,6	
18	Коридор	16,6	
19	КУИ	3,00	
20	Лестница	19,9	
21	Инвентарная	9,4	
22	Коридор	14,1	
23	Кабинет персонального тренера	24,3	
25	Тех. помещение	4,0	
26	Кухня	16	
26а	Лоббия	91,8	
27	Тренерская X	22,2	
28	Санузел	2,2	
28а	Душевые	4,1	
29	Кабинет менеджера	28,2	
30	Студия пилатес/Йоги. Занятия пилатес	55,5	
31	Студия боевых искусств	60,7	
32	Воскресная и детская студия групповых и танцевальных занятий	115,4	
33	Детская и юниор	4,0	
34	Коридор	8,9	
35	Санузел	13,5	
36	Санузел	13,52	
37	Коридор	56,6	
38	Коридор	72,8	
39	Танцбар	7,8	
40	Студия Body & Mind, Йога, Аэробик	43,8	
41	Воскресная студия групповых и танцев. занятий	90,8	
42	Студия спортивно-игровых студия	62,5	
43	Ресепшен	45,36	
44	Танцбар	6,55	
45	Лестница	16,2	
46	Детская студия функциональной тренировки	49,2	
47	Лестница	11,71	
48	Лестница	21,4	
49	Холл	57,3	
51	Кабинет УЗИ	25,8	
53	Лифтовой холл	6,70	
54а	Холодильник	2,15	
55	Холод. Камеры временного хранения отходов	10,7	
56	Лестница	7,3	
57	Санузел	7,1	
58	Санузел	7,2	
59	Кухня	3,3	
61	Санузел ММГМ	3,42	
62	Лаборатория – заборы крови и материала	21,3	
64	Корсвая	21,0	
65	Каюта хранения чистого белья	16,3	
66	Кабинет врача дерматолога-венеролога	6,7	
67	Процедурный кабинет дерматолога	11,9	
70	Кабинет врача гинеколога	22,8	
71	Санузел посетителя	2,6	
72	Процедурный кабинет гинеколога	25,5	
75	Лестница	20,2	
76	Коридор	35,2	
78	Кабинет врача онколога	21,4	
79	Кабинет врача эндокринолога	20,3	
80	Коридор	40,8	
81	Кабинет врача кардиолога	20,5	
82	Кабинет / Лоббиное врач	13,50	
83	Кабинет Зам.гл. врач.	11,70	
84	Кабинет бухгалтерии	12,6	
85	Переоборудован	15,0	
86	Кабинет врача диетолога-нутрициониста	14,8	

СХЕМА БЛОКИРОВКИ

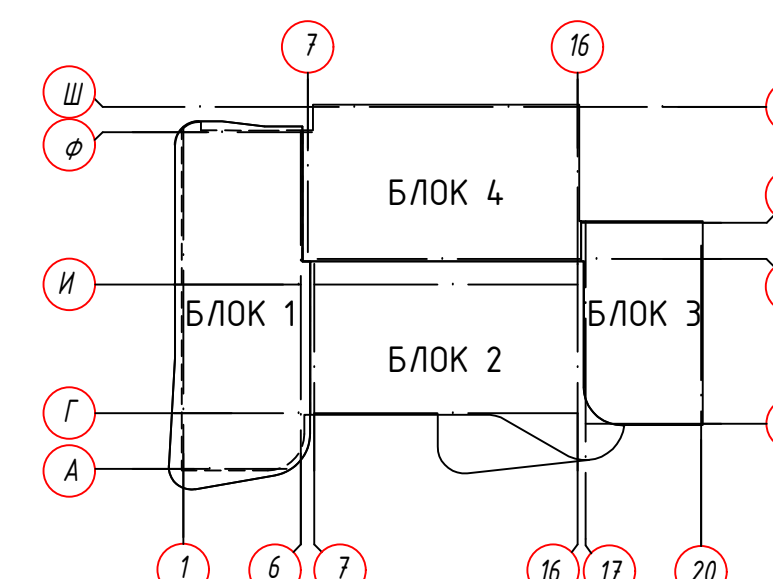


					02/09/ФПК-ХС				
					Корректировка рабочего проекта "Реабилитационно-диагностический центр с госпитальной (Физкультурно-оздоровительный комплекс с госпитальной) горой Алатау, район Селькуп Худейн вем Талар, адм МЗ 25".				
ИП	Кол	№ док	Листы	Подпись	Дата	Физкультурно-оздоровительный комплекс			
Гиз		Галимжанов С			02.26	(Листы 1, 2, 3, 4)			
Проверил					02.26	РП	18	•	
Разработал						План системы дренажа кондиционирования 3-го этажа на опм. +12,000			
						T00 "Vitality Group"			

План системы дренажа кондиционирование 4-го этажа на отм. +16,800

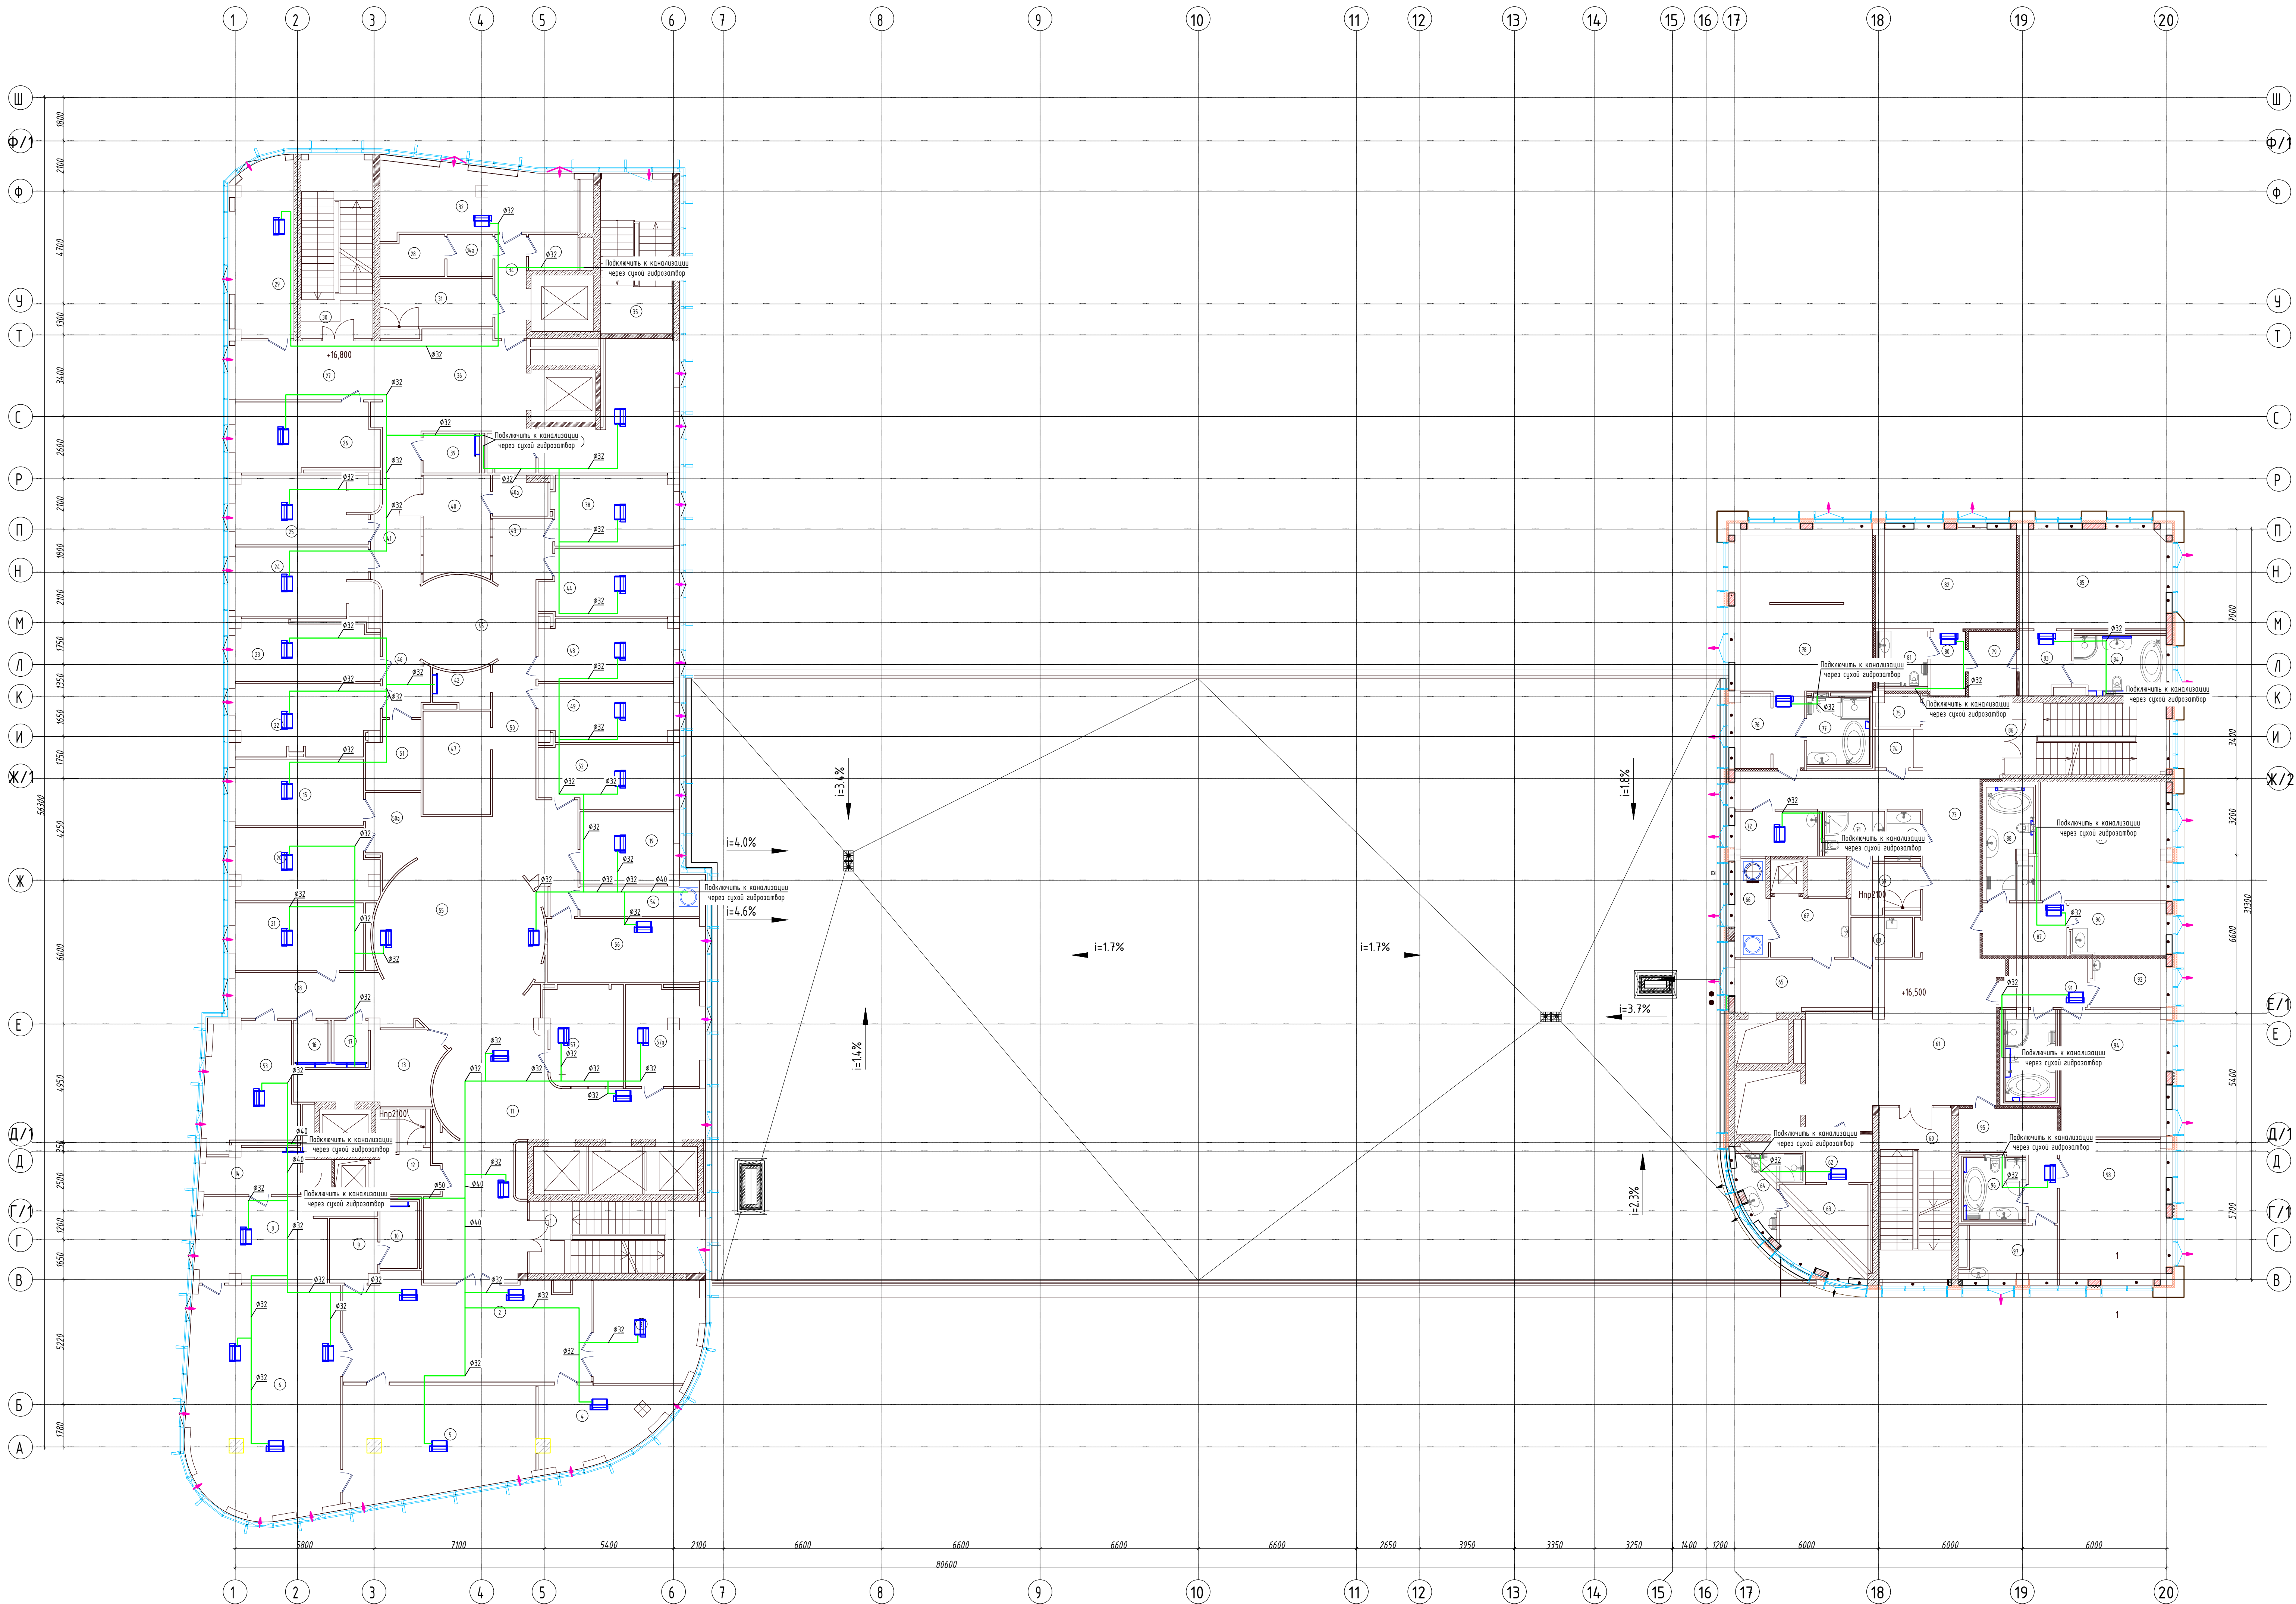


Экспликация помещений				Экспликация помещений			
Поз	Наименование	площадь	Кат. поме- ния	Поз	Наименование	площадь	Кат. поме- ния
Блок 1				Блок 3			
1	Лестничная клетка	21.8		60	Лестничная клетка	21.8	
2	Ресепшен	42.7		61	Лифтовый холл	44.50	
3	Кабинет	19.0			Номер 1		
4	Кабинет	15.7		NK1	в том числе		
5	Переоборная	35.9		62	Холл	5.60	
6	Кабинет ген.директора	58.9		63	Спальня	13.5	
7	Помещение	2.2		64	Санузел	5.8	
8	Комната отдыха	18.7		65	Лифтовый холл	13.3	
9	Мансарка	5.2		66	Тех.помещение	5.8	
10	Санузел	2.5		67	К/М	8.1	
11	Холл	61.6		68	Кухня	4.2	
12	К/М	7.0		69	Помещение персонала	6.4	
13	Барбер ресепшен	2.5		70	Санузел	2.6	
14	Санузел	7.5		71	Санузел	4.5	
15	Каб. маникюра и педикюра	30.6		72	Комнат. мед.сестры	6.7	
16	Санузел	2.5		73	Коридор	42.30	
17	Санузел	2.5		74	Бельевая	2.4	
18	Коридор	13.5		75	Красовая	2.5	
19	Барбер	11.9			Номер 2		
20	Парикмахерская	17.4		NK2	в том числе		
21	Парикмахерская	15.2		76	Холл	5.3	
22	Кабинет	17.6		77	Санузел	7.2	
23	Кабинет	14.8		78	Спальня	41.3	
24	Кабинет	17.2		79	Коридор	5.4	
25	Кабинет	16.7			Номер 3		
26	Кабинет Вит. косметолога	16.9		NK3	в том числе		
27	Коридор	15.6		80	Холл	3.9	
28	Электромонтажная и красовая	4.4		81	Санузел	4.7	
29	Персональный мастер	18.6		82	Спальня	25.0	
30	Лестница	22.9			Номер 4		
31	Специализационная	10.2		NK4	в том числе		
32	Помещение персонала	22.0		83	Холл	5.5	
33	Санузел	3.1		84	Спальня	10.0	
34	Коридор	5.7		85	Санузел	26.7	
34а	К/М	3.3		86	Лестница	20.8	
35	Лестница	19.9			Номер 5		
36	Холл	31.6		NK5	в том числе		
37	В/П маникюр и педикюр	22.1		87	Холл	7.7	
38	Кабинет	15.2		88	Спальня	25.45	
39	Санузел	3.9		89	Санузел	26.8	
40	Парк. аппаратов	11.7		90	Массажная	8.8	
40а	Красовая	3.6			Номер 6		
41	Коридор	7.0		NK6	в том числе		
42	Санузел	3.3		91	Холл	7.1	
43	Коридор	6.8		92	Массажная	6.7	
44	Кабинет	15.3		93	Санузел	7.8	
45	Холл	14.0		94	Спальня	24.0	
46	Коридор	9.1			Номер 7		
47	Кабинет	12.0			в том числе		
48	Кабинет	14.6		95	Холл	10.7	
49	Кабинет	13.6		96	Санузел	6.8	
50	Коридор	14.2		97	Массажная	8.9	
50а	Коридор	23.3		98	Спальня	27.6	
51	Склад бельевая	6.1				462.28	
52	Каб. маникюра и педикюра	14.6					
53	Кабинет	18.5					
54	К/М	6.4					
55	Ресепшен	44.9					
56	Кабинет директора салона	17.4					
57	Воздушист	13.2					
57а	Укладоч. сушка	13.3					

СХЕМА БЛОКИРОВКИ

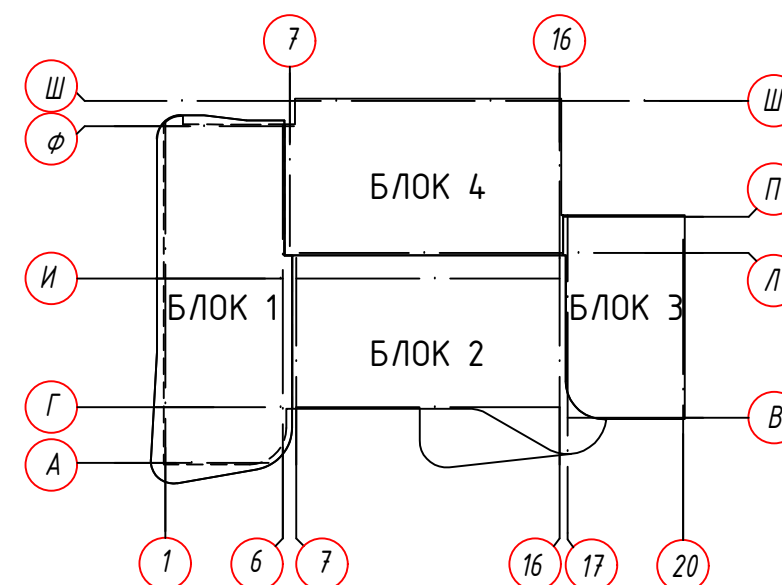


				02/09/ФОК-ХЛ			
				Корректировка рабочего проекта "Реабилитационно-диагностический центр с историческим (рекреационно-образовательным) комплексом с историческим ядром. Аллея, район Сельм.у.Хорош.Вит.Талин, 40/М 25"			
Изм.	Кол.	И.В.м.Лит.	Подпись	Дата	С. 02.26	Лист 19	Лист 25
Г.И.П.	Г.И.П.	Г.И.П.	Г.И.П.	Г.И.П.	Г.И.П.	Г.И.П.	Г.И.П.
Проектирование	Разработка	Разработка	Разработка	Разработка	Разработка	Разработка	Разработка
				План системы дренажа кондиционирования 4-го этажа на отм. +16,800			
				100 "Vitality Group"			

План системы дренажа кондиционирование 5-го этажа на отм. +21,600

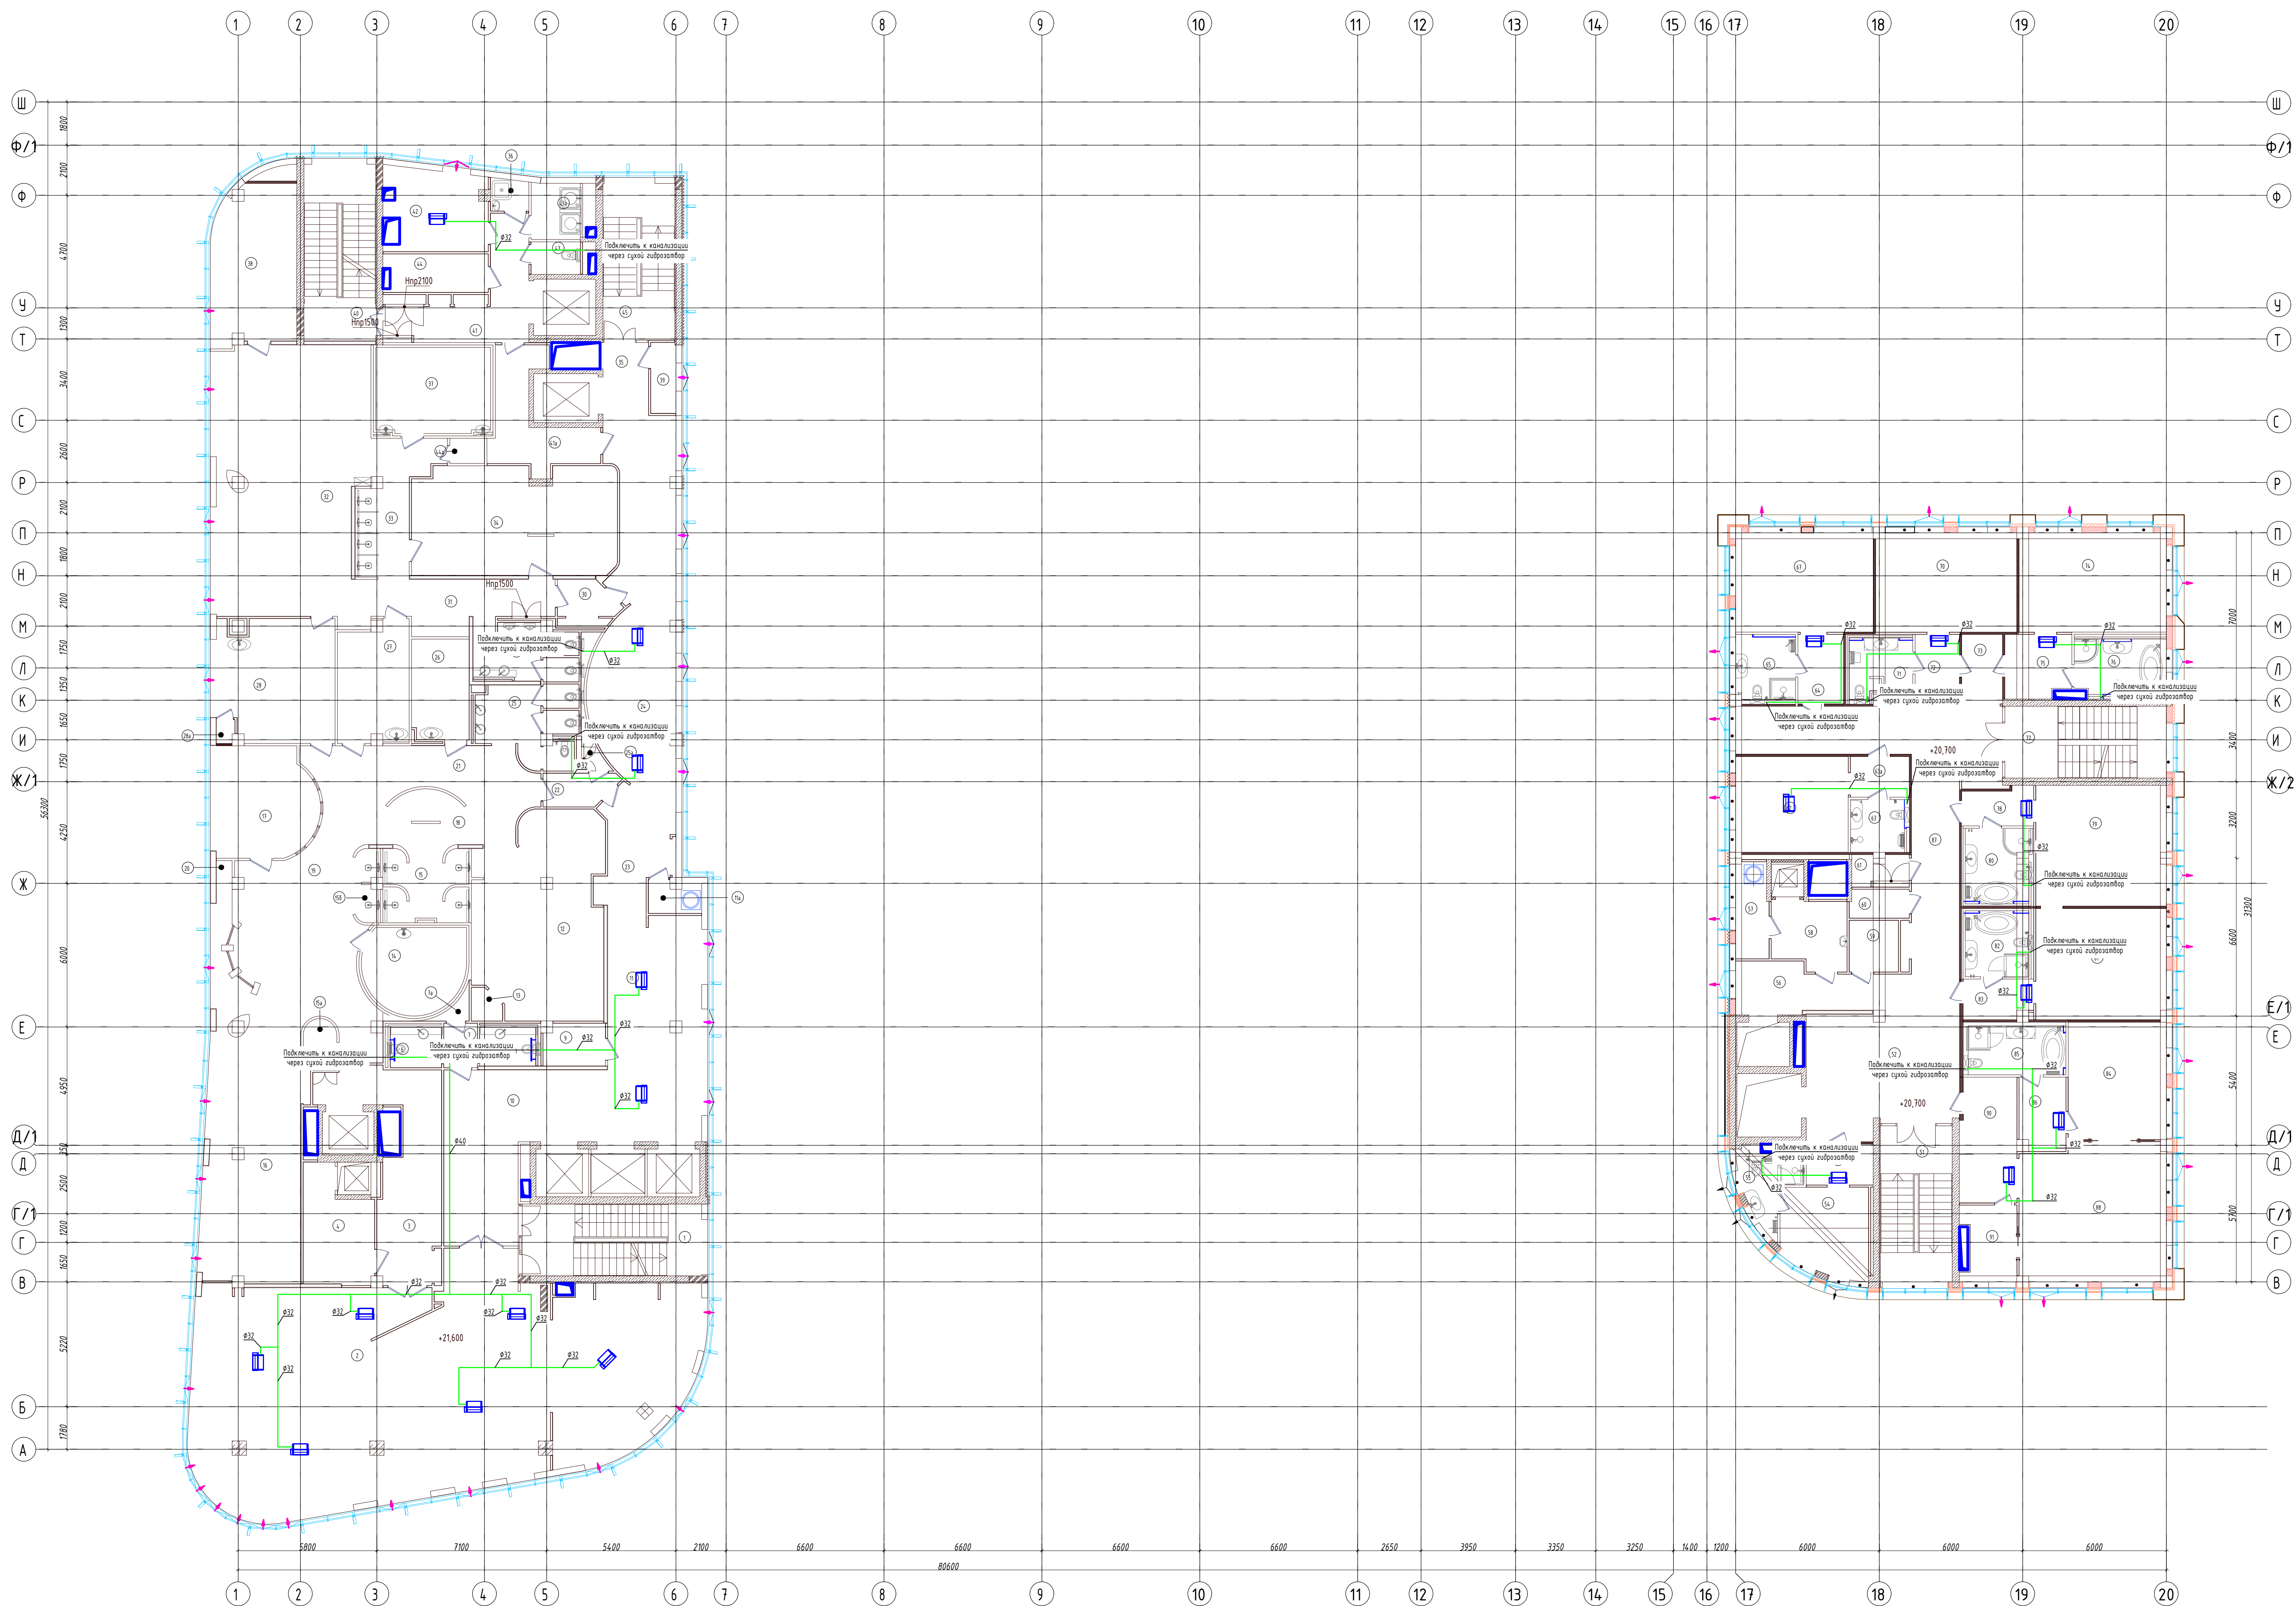


Экспликация помещений (начало)				Экспликация помещений (окончание)			
Поз	Наименование	площадь	Кат. помещ.	Поз	Наименование	площадь	Кат. помещ.
Блок 3							
1	Лестничная клетка Лм-3.1	23.2		51	Лестница Лм-13	19.60	
2	Помещение	180.0		52	Холл	315	
3	Раздаточная	25.4			Номер 1		
4	Очистка, сортировка посуды	12.60			В том числе		
6	Санузел	3.60	53	Холл	5.4		
7	Танбур	2.60	54	Спальня	12.8		
14	Оборудованное хранилище	1.0	55	Санузел	5.4		
8	Санузел	3.8	56	Лифтовый холл	16.2		
9	Гардероб	4.5	57	Подсобное помещение	5.4		
10	Холл	45.4	58	ЛТМ	8.6		
11	Ресторан	25.7	59	Кухня	4.4		
11а	Пом. Вельтерроба	2.8	60	Кроссовая	3.0		
12	Пом. Вельтерроба	4.31	61	Вельевая	2.9		
13	Комната переобедания	1.5		Номер 2			
14	Хаммам	15.30		В том числе			
15	Душевые	10.9	62	Спальня	18.8		
15а	Душевые	2.4	63	Санузел	5.0		
15b	Душевые	2.9	63а	Холл	4.2		
16	Зона отдыха	85.2		Номер 3			
17	Сауна	19.4		В том числе			
18	Фены	7.0	64	Холл	5.5		
19	Холл	54.0	65	Санузел	6.7		
20	Тех.помещение	1.2	67	Спальня	24.4		
21	Коридор	18.4		Номер 4			
22	Танбур	3.9		В том числе			
23	Холл	15.6	70	Спальня	24.4		
24	Холл	32.4	71	Санузел	6.5		
25	Санузел	12.1	72	Холл	5.4		
25а	Санузел	1.4	73	Танбур	4.9		
26	Массажная	10.0		Номер 5			
27	Индивидуальное парение	13.85		В том числе			
28	Массажная	24.63	74	Спальня	25.4		
28а	Тех.помещение	0.35	75	Холл	7.2		
29	Санузел	9.9	76	Санузел	9.1		
30	Танбур	4.3	77	Лестница Лм- 2.3	20.2		
31	Коридор	15.9		Номер 6			
32	Зона отдыха	75.44		В том числе			
33	Душевые	8.30	78	Холл	4.6		
34	Вил разведчика	37.90	79	Санузел	27.4		
35	Лифтовый холл	21.3	80	Санузел	8.2		
36	Клм	2.1		Номер 7			
37	Хаммам	18.8		В том числе			
38	Сауна	22.6	81	Спальня	25.2		
39	Комната для курения	3.4	82	Санузел	7.4		
40	Лестница Лм-2.1	22.8	83	Холл	4.7		
41	Коридор	13.2		Номер 8			
41а	Коридор	12.72		В том числе			
42	Комната персонала	15.0	84	Спальня	20.1		
43	Санузел	2.3	85	Санузел	8.4		
43а	Душевые	4.80	86	Гардероб	5.8		
44	Тех.помещение	7.0	87	Коридор	5.64		
44а	Душе	1.5	88	Спальня	34.7		
45	Лестница Лм-11	20.9	90	Холл	12.3		
			91	Кухня	6.8		

СХЕМА БЛОКИРОВКИ

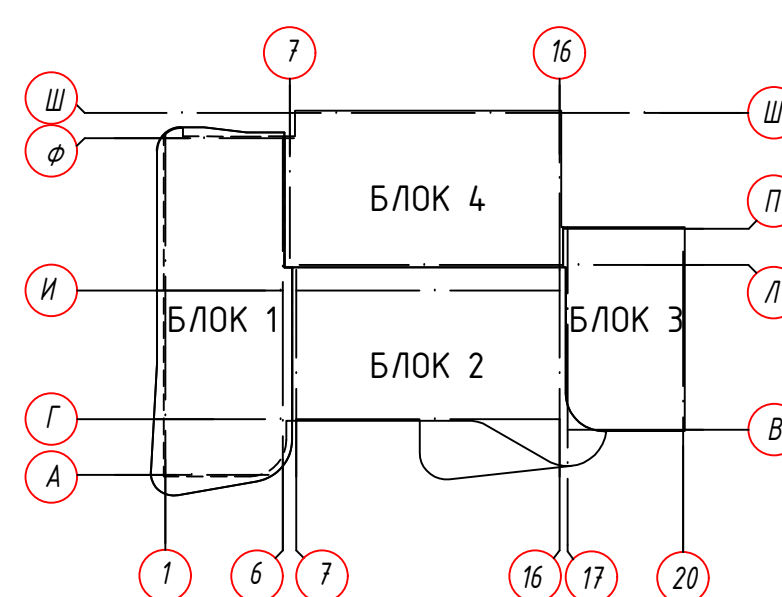




						02/09/ФСК-КС		
						Корректировка рабочего проекта "Реабилитационно-диагностический центр с гостиницей (Физкультурно-оздоровительный комплекс с гостиницей) город Астана, район Саяхан, Район Жетысай, м/р 25"		
Изм.	Кол.	N док.	Лист	Подпись	Дата			
ГМП		Галижанов	С		02.26	Слово	Листов	
Проверил					02.26			
Разработал						РП	20	*
План системы дренажа кондиционирования 5-го этажа на опп. «21.600						100 "Utility Group"		

Схема системы кондиционирования (начало)

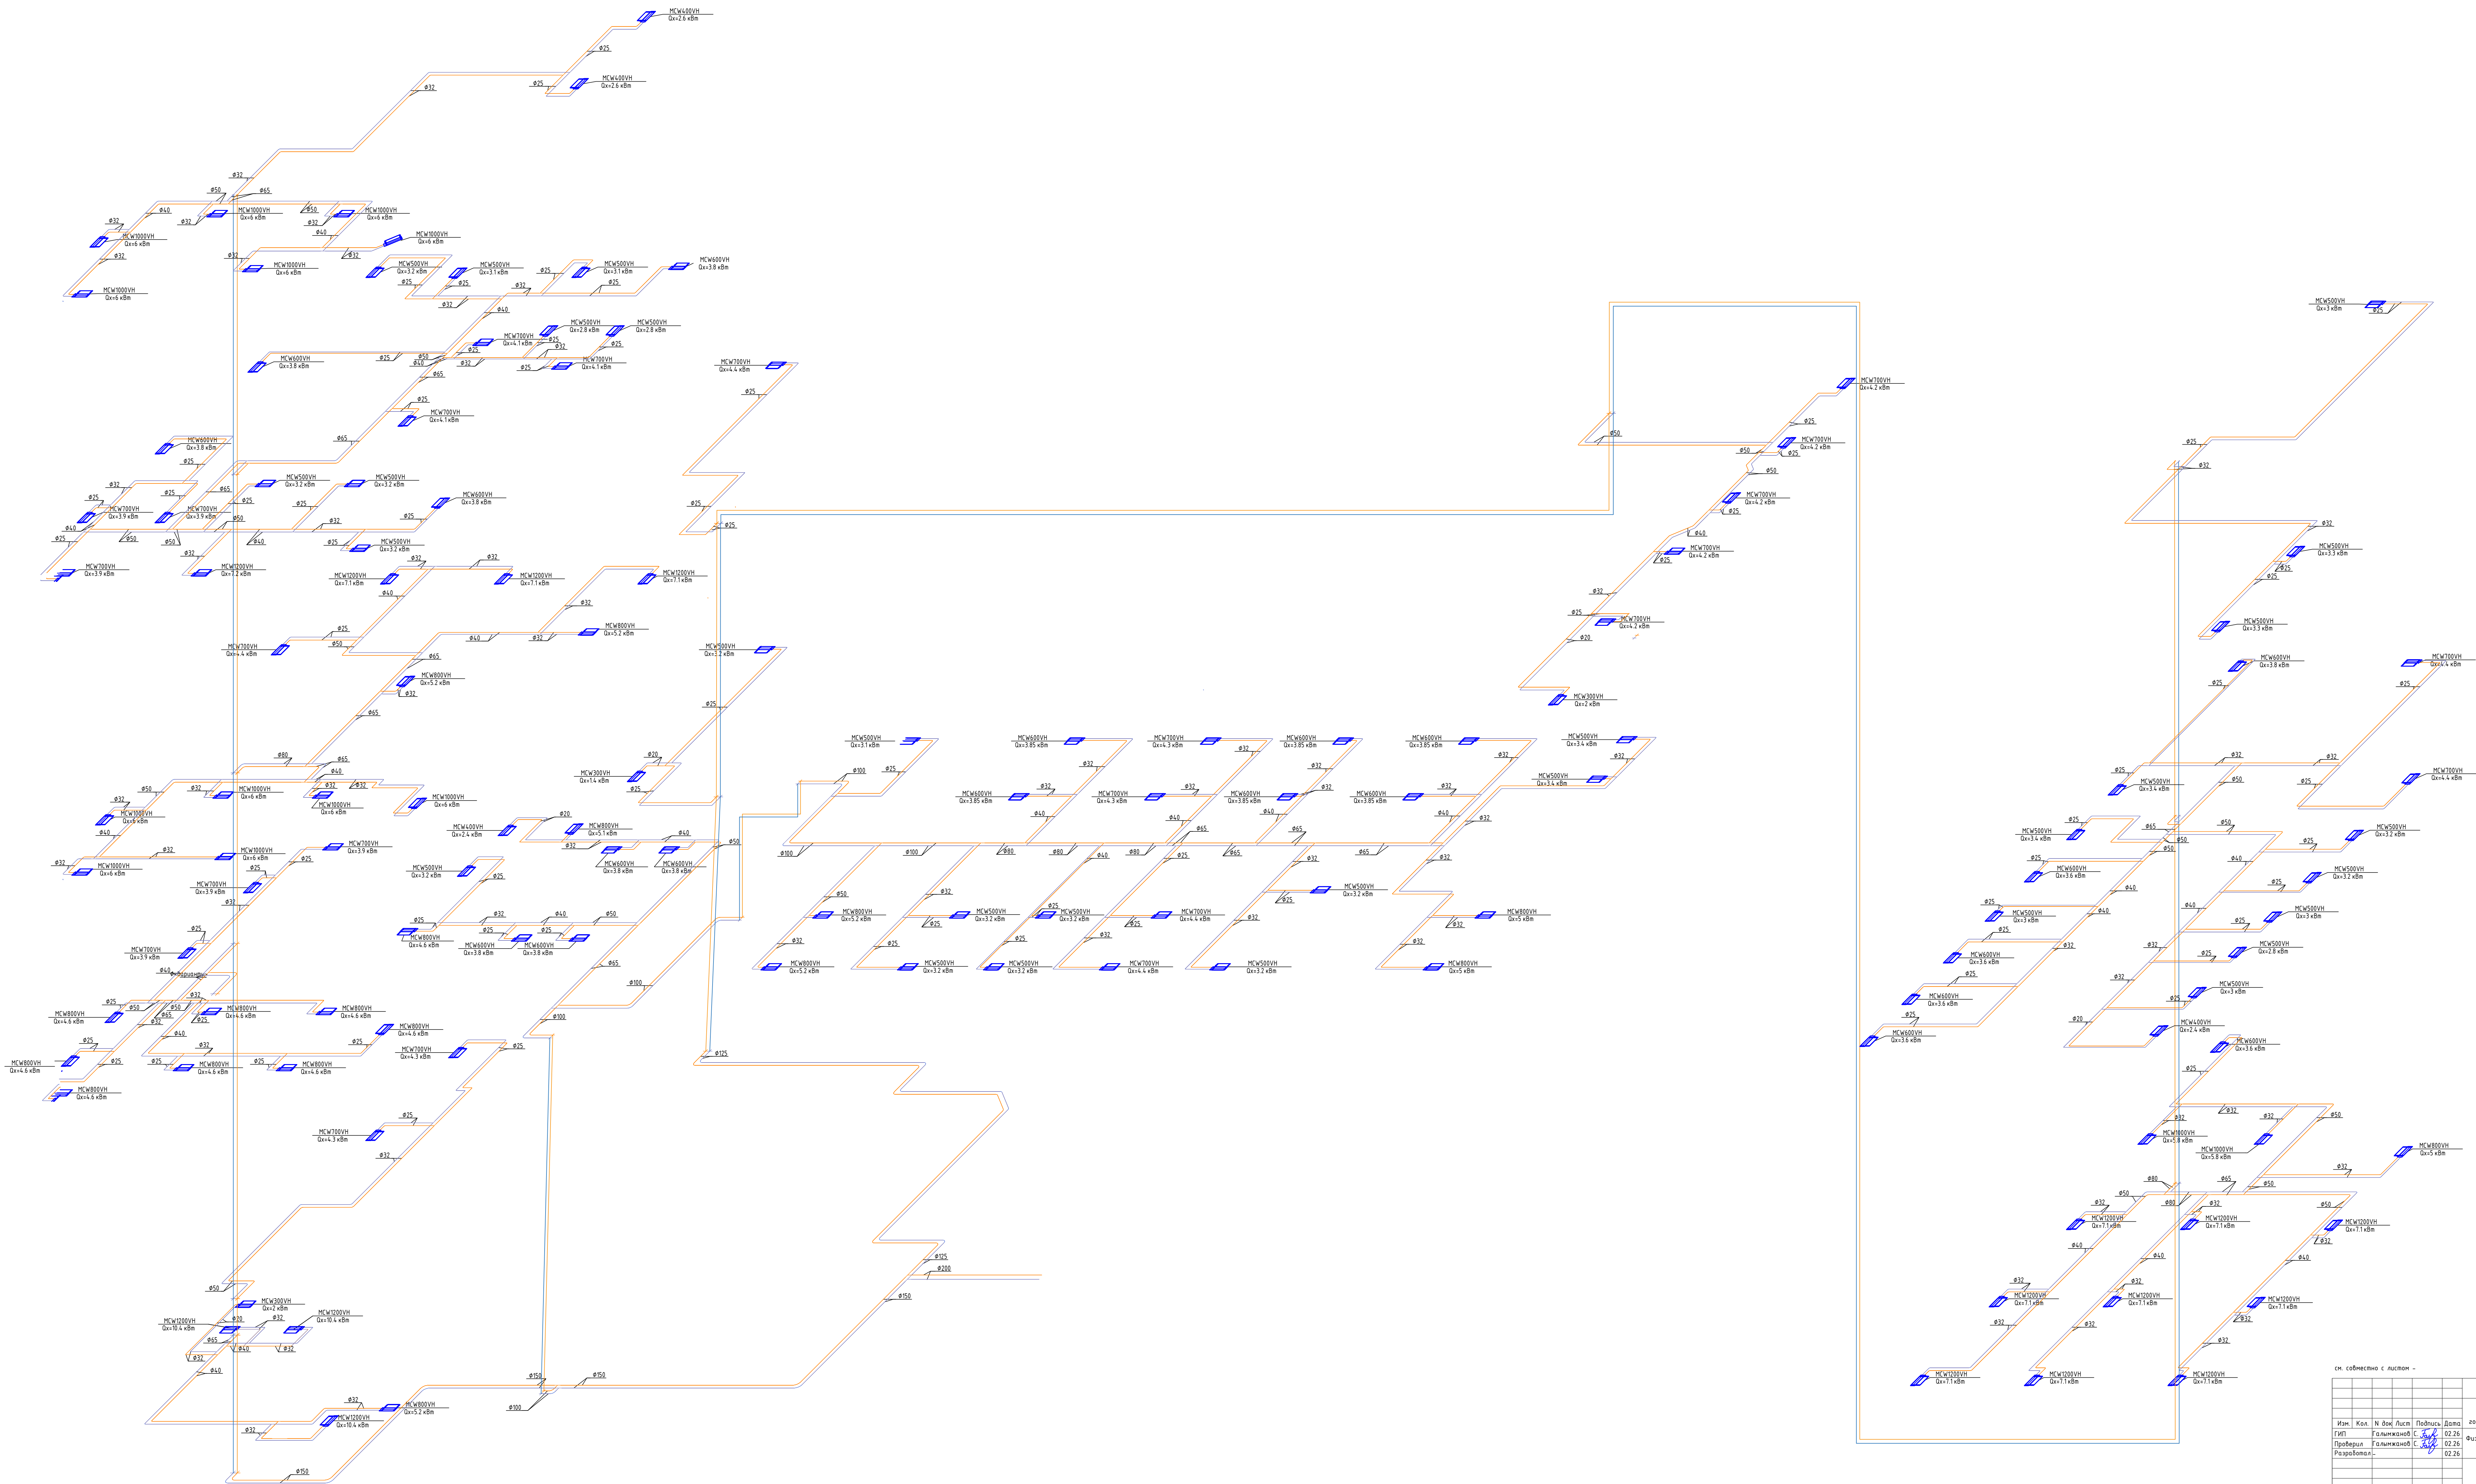

см. совместно с листом -


										02/09/ФОР-ХС	
										Корректировка рабочего проекта/Реализационно-диагностический центр с системой (Физкультурно-оздоровительный комплекс с системой) 1-й этаж, район Сосновый Бор, Таллин, 00000	
Изм.	Кол.	И. И. И.	Подпись	Дата	Изм.	Кол.	И. И. И.	Подпись	Дата	Физкультурно-оздоровительный комплекс (Этажи 1, 2, 3, 4)	
Проверка	Разработка	Разработка	Разработка	Разработка	Разработка	Разработка	Разработка	Разработка	Разработка	РП	21
Схема системы кондиционирования (начало)										ООО "Виталь Групп"	

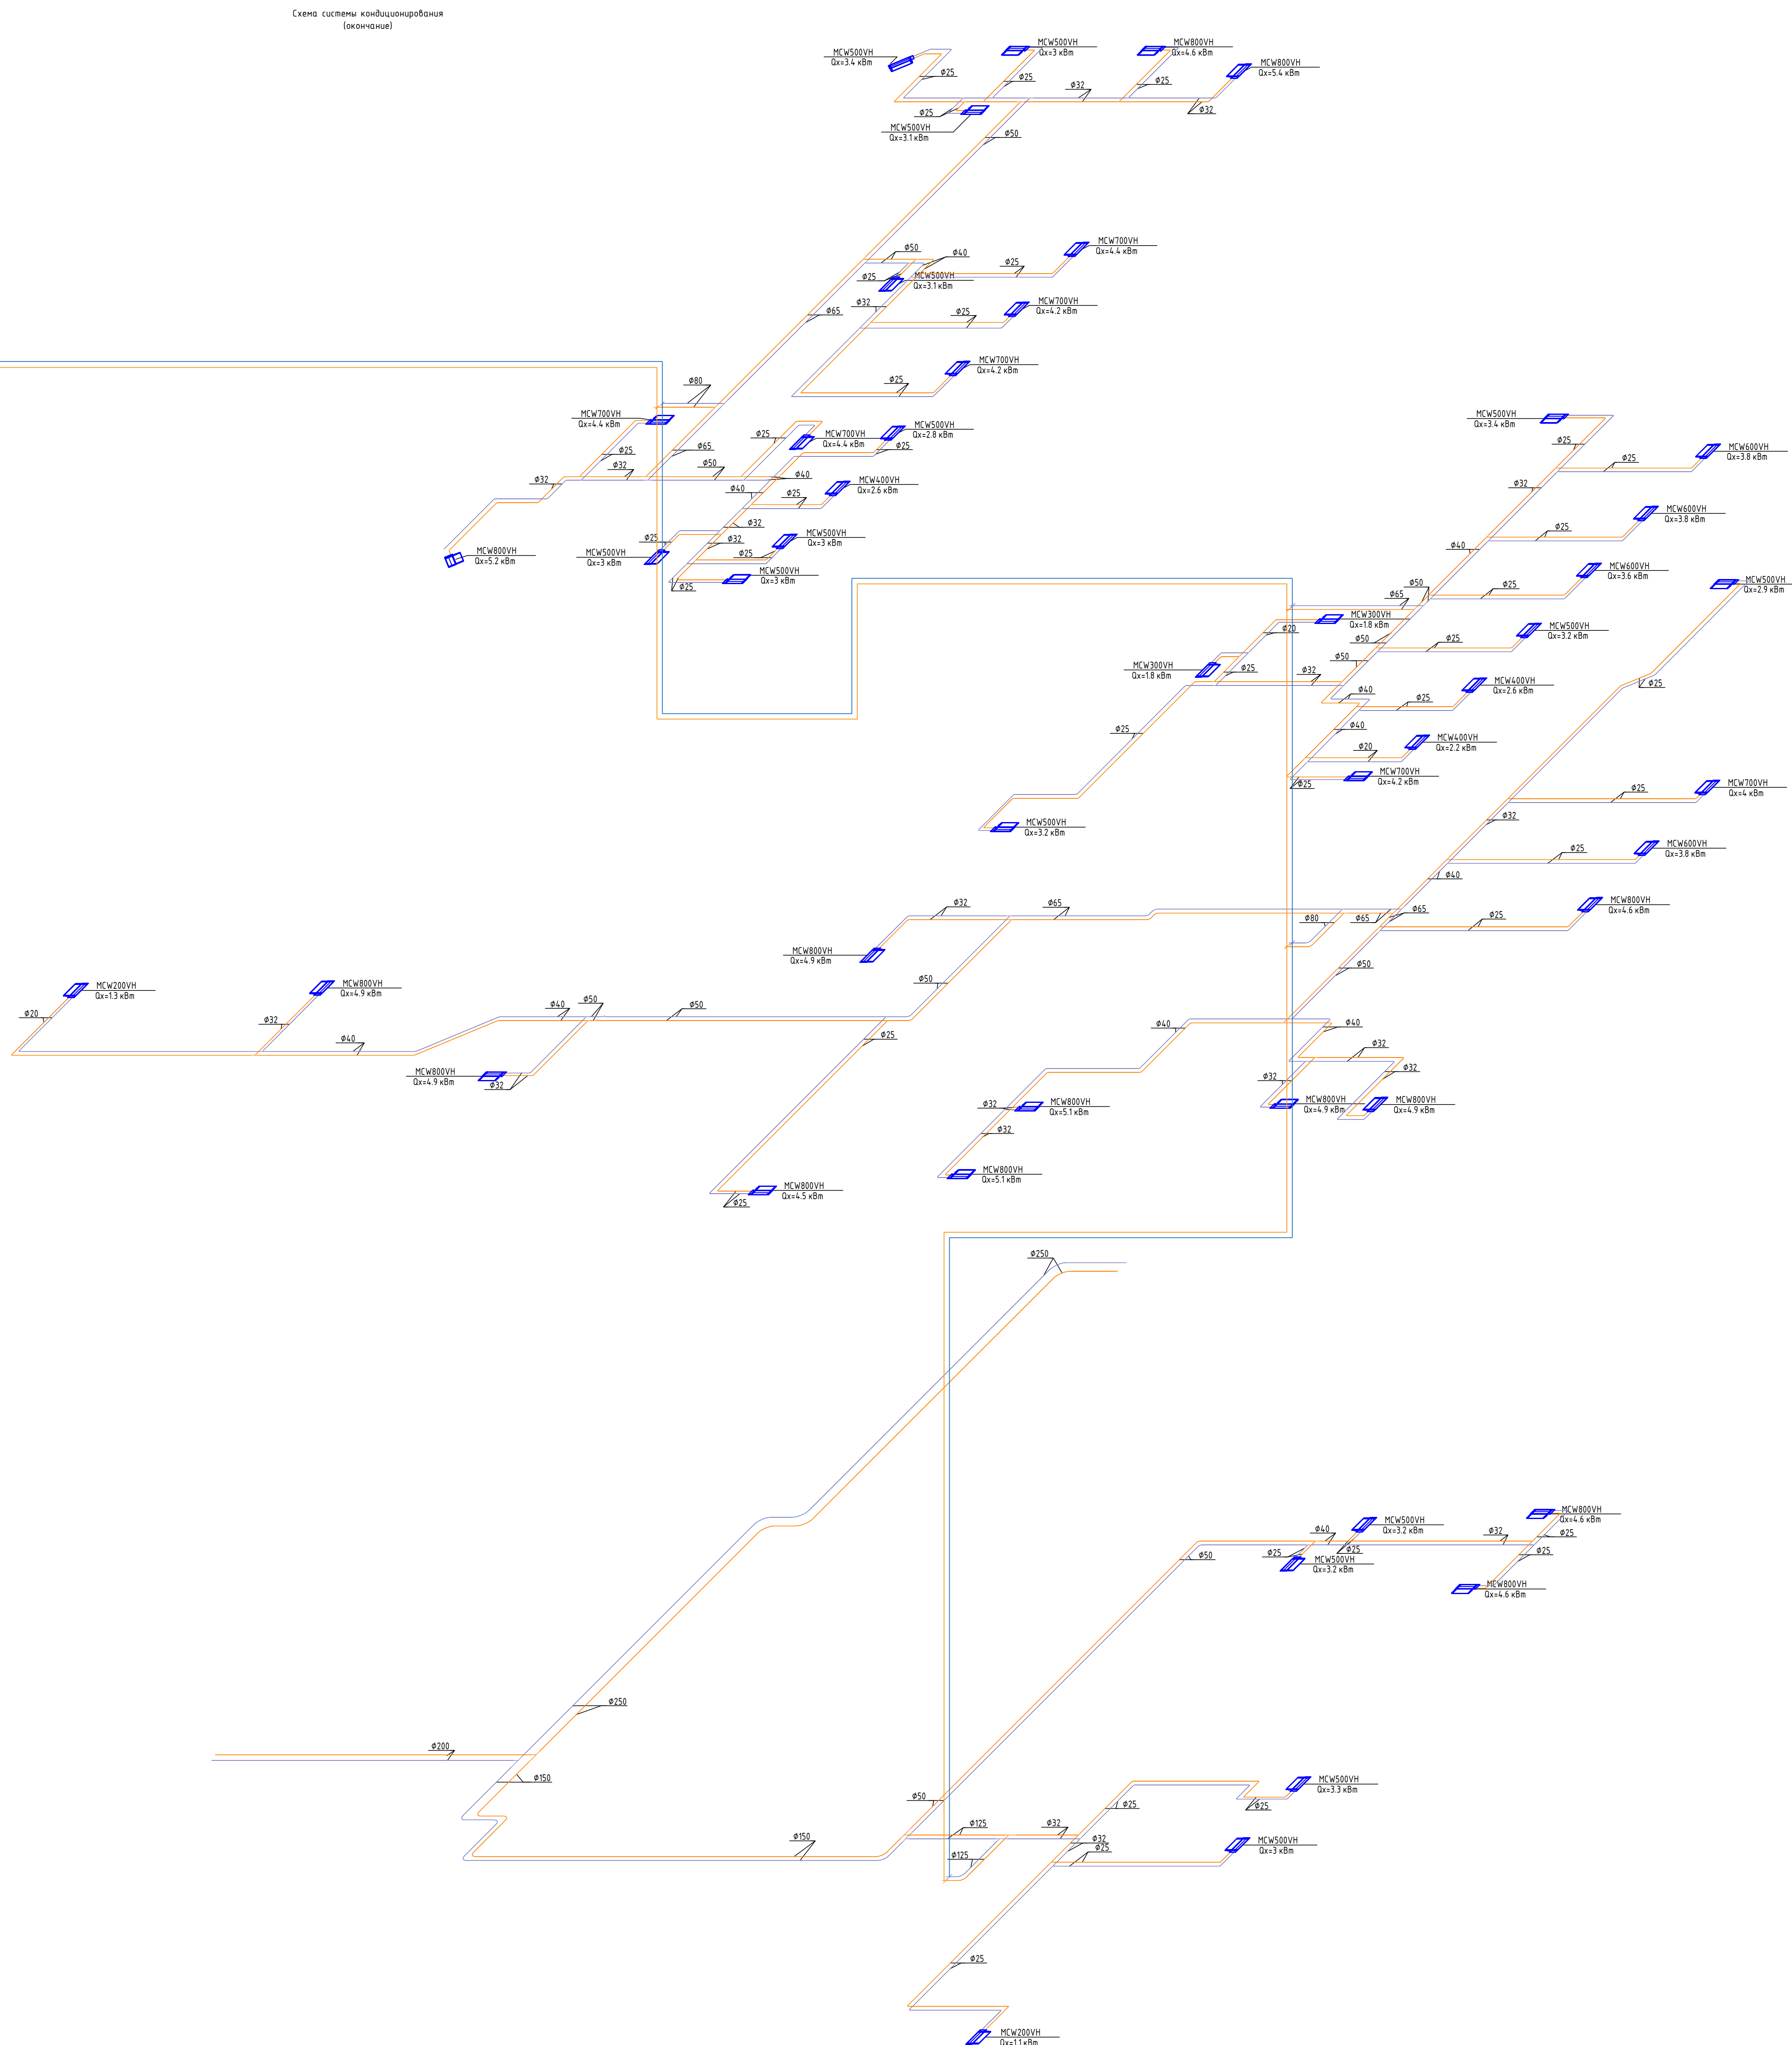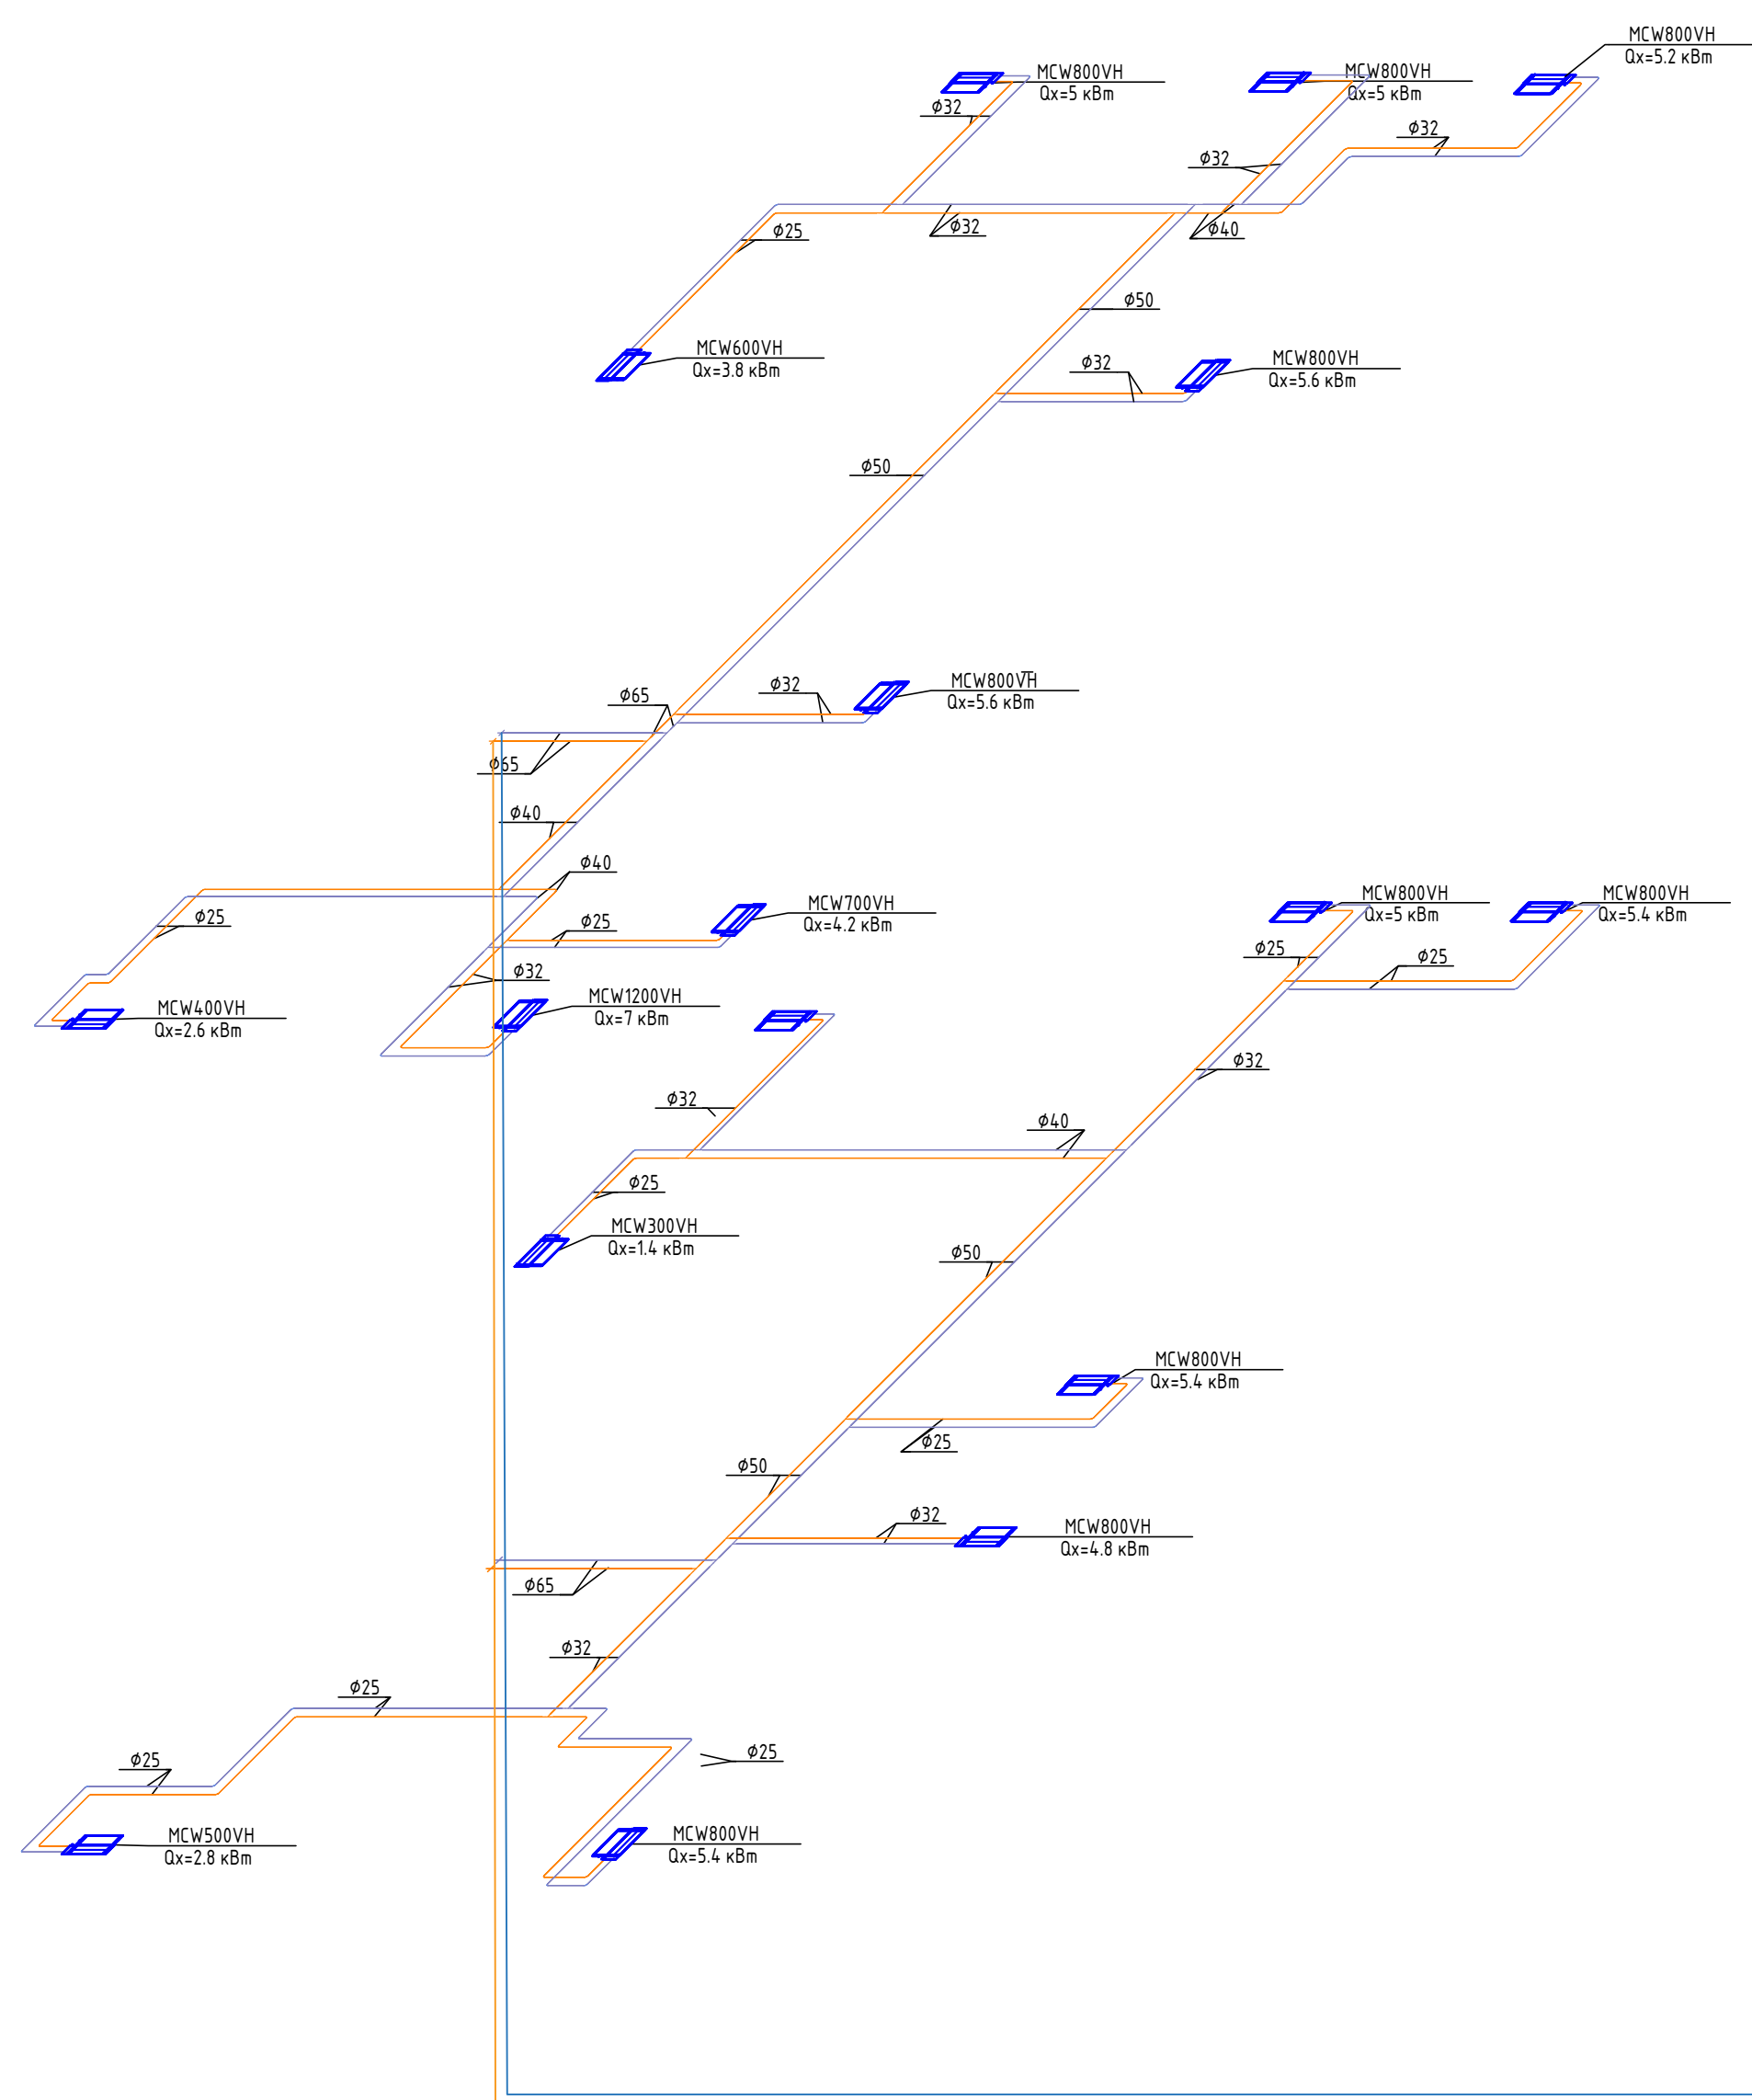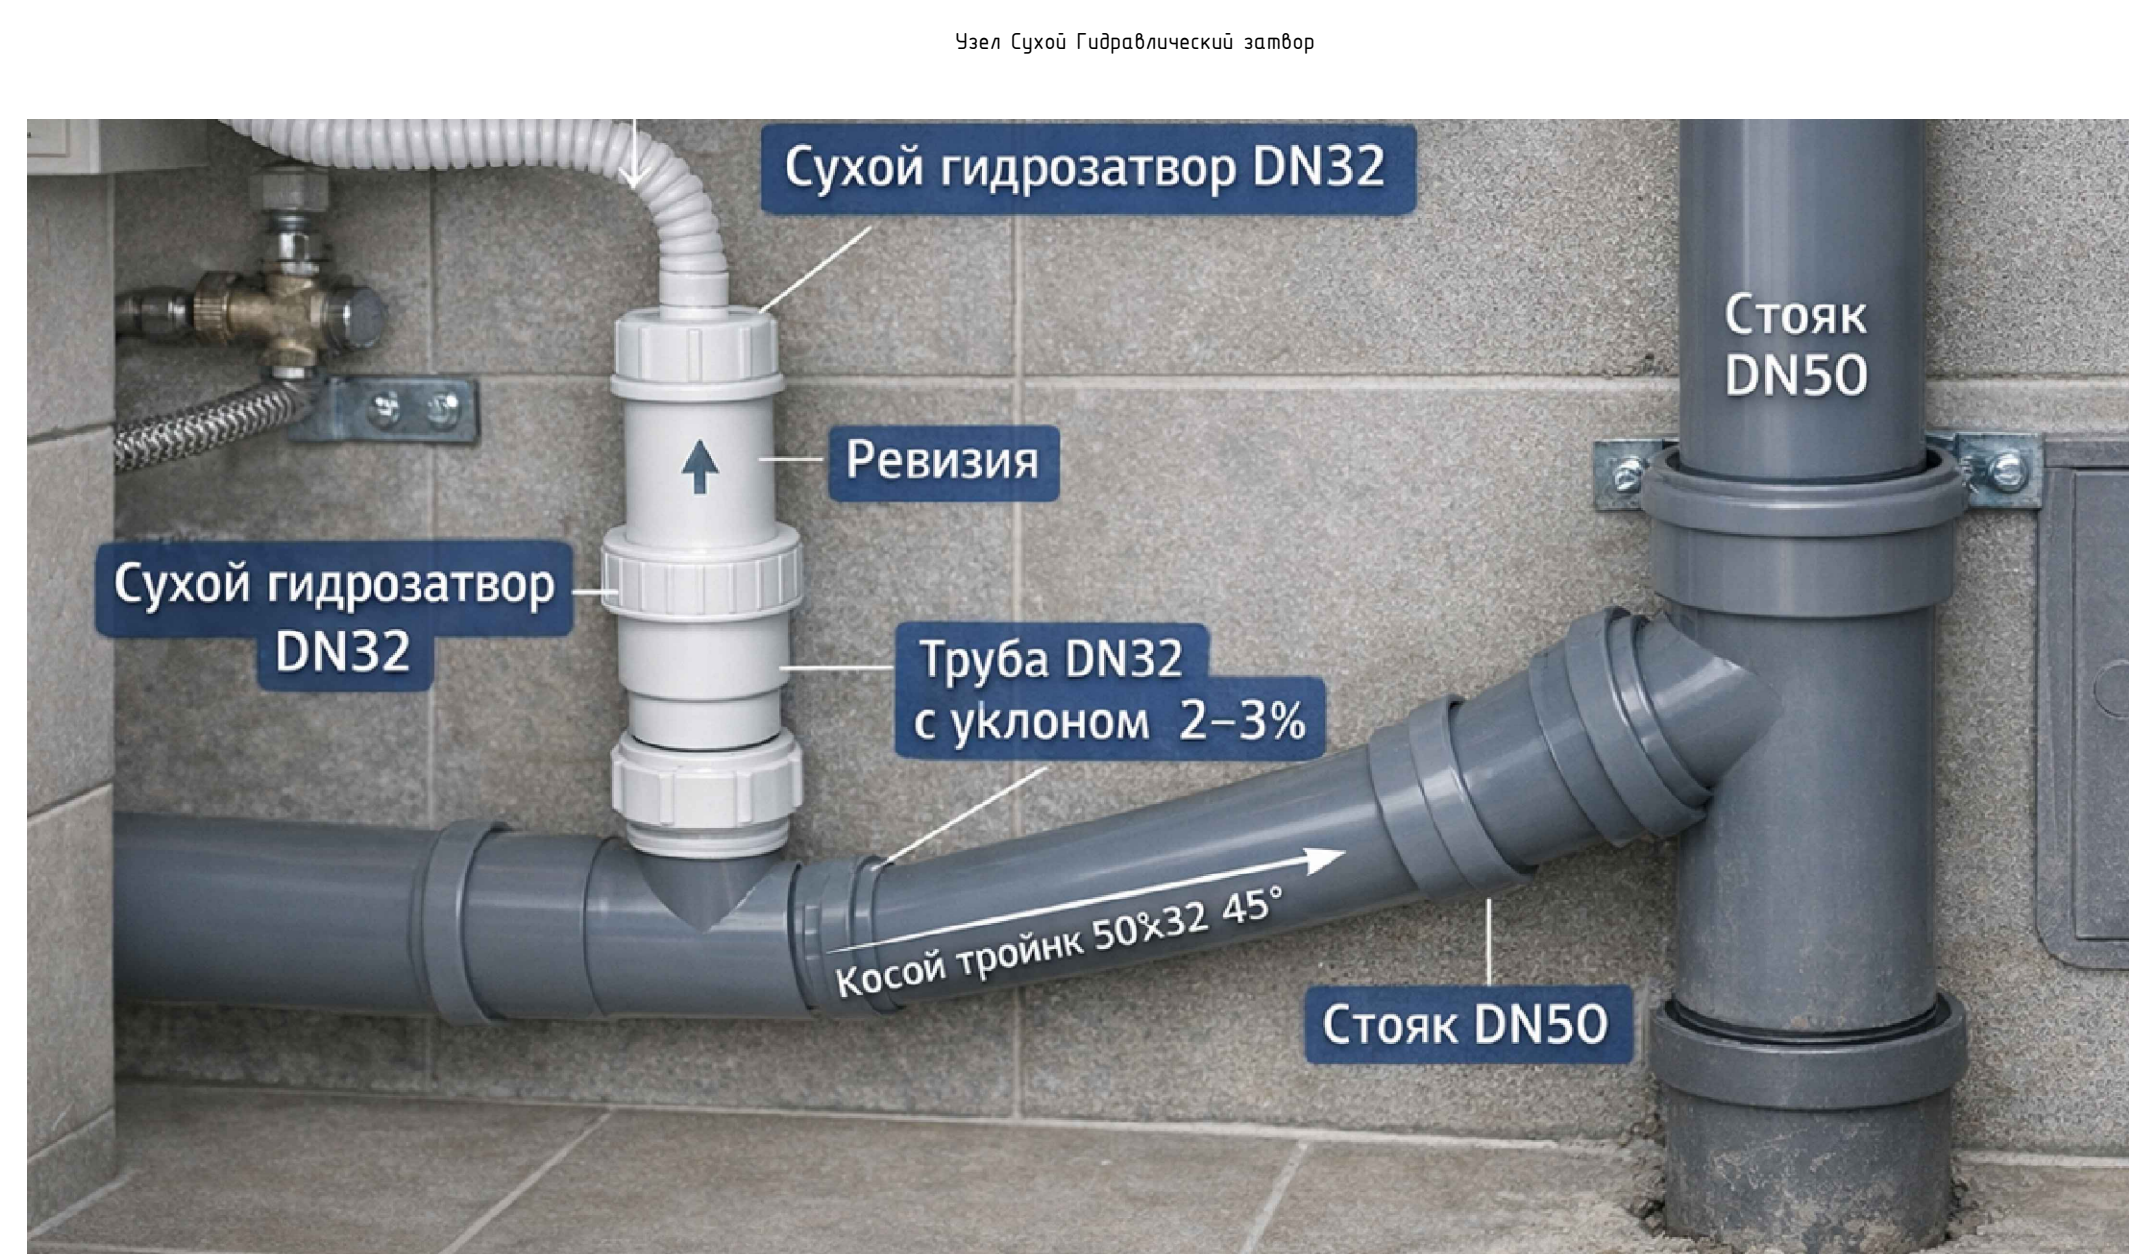

см. совместно с листом -20

[illegible]


Принципиальная схема

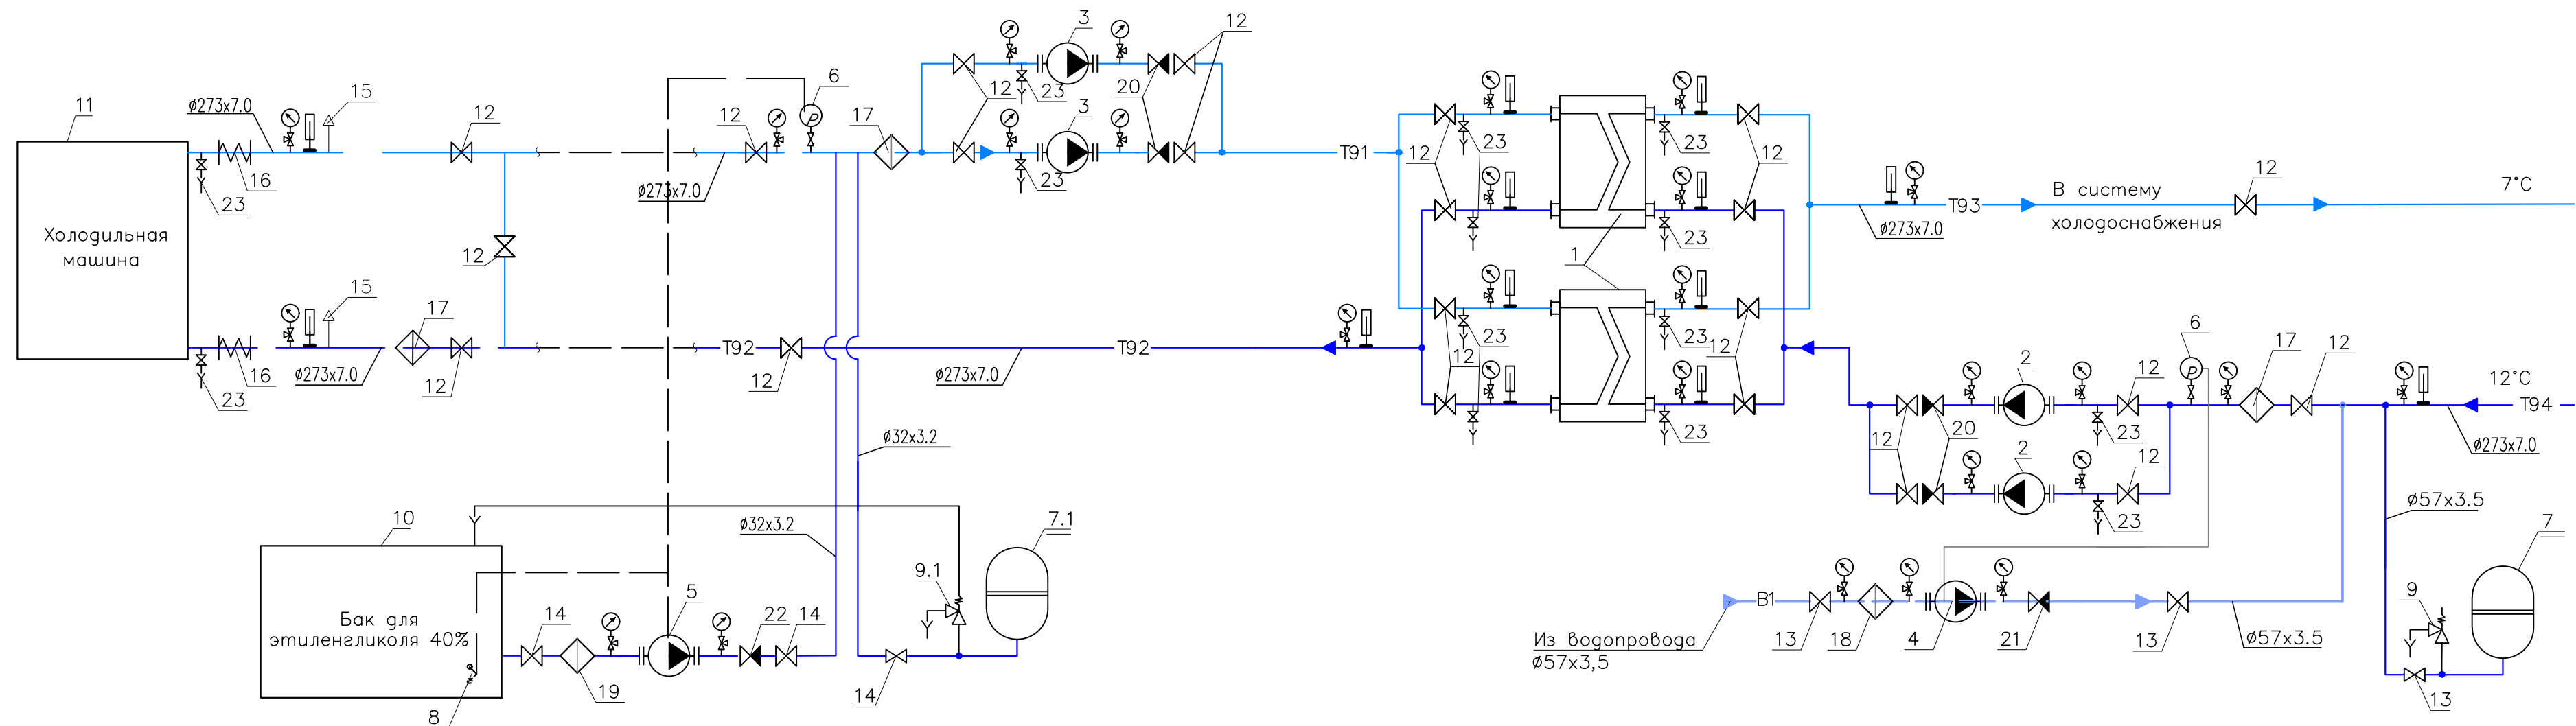

Позиция	Обозначение	Наименование	Кол-во	Примечание
1	Danfoss XGF 100-IS10-172-TMTL37 #1934-241216162504	Аппарат теплообменный пластинчатый разборный мощностью N=1194,38кВт	2	1 рабочий 1 резерв.
2	TPE 125-400/4 NC-A-F-A-BAQE-RW3	Циркуляционный насос с частотным перекачиваемая среда вода регулированием G=205.26м3/ч, H=35,0м,	2	1 рабочий 1 резерв.
3	TPE 150-220/4 A-F-A-BQQE-PWA	Циркуляционный насос с частотным перекачиваемая среда этиленгликоль 40% регулированием G=234.47м3/ч, H=20,0м,	2	1 рабочий 1 резерв.
4	CM 5-4 A-R-A-E-AVBE F-A-A-N	Насос погпиточный G=4.0м3/ч, H=32м,	1	
5	CM 1-2 A-R-A-E-AQQE F-A-A-N	Насос погпиточный G=1.0м3/ч, H=10м,	1	
6	Danfoss KPI 35	Прессостат с однополюсным переключателем, G 1/4"А диапазон настройки -0,2-8 бар	2	
7	Wester WRV-750	Бак расширительный мембранный 10бар,V=750л	1	
7.1	Wester WRV-500	Бак расширительный мембранный 10бар,V=500л	1	
8	IGD 10/S (Speroni)	Поллабковый выключатель	1	
9	O.R. (Италия)	Предохранительный регулируемый клапан Ду=50мм., 0.5-16 бар	1	
9.1	O.R. (Италия)	Предохранительный регулируемый клапан Ду=32мм., 0.5-16 бар	1	
10		Бак полиэтилен, V=1000л	1	

Позиция	Обозначение	Наименование	Кол-во	Примечание
11		Холодильная машина (чиллер) N=000.00кВт темпратура 5-10 °C этиленгликоль 40%	1	
12	Danfoss JIP Premium WW	Кран шаровой приварной Ø250	23	
13	Danfoss JIP Premium WW	Кран шаровой приварной Ø50	3	
14	Danfoss JIP Premium WW	Кран шаровой приварной Ø32	3	
15	O.R. (Италия)	Автоматический воздухоотводчик Ду15	2	
16		Гибкая вставка Ø250	2	
17	Danfoss FVF	Фильтр сетчатый Ду250 Ру=16бар	3	
18	Danfoss FVF	Фильтр сетчатый Ду50 Ру=16бар	1	
19	IVR (Италия)	Фильтр сетчатый Ду32 Ру=16бар	1	
20	Danfoss NVD 402	Клапан обратный Ду250, Ру=16бар	4	
21	Danfoss NVD 402	Клапан обратный Ду50, Ру=16бар	1	
22	IVR (Италия)	Клапан обратный Ду32, Ру=16бар	1	
23	IVR (Италия)	Кран шаровый муфтовый Ду25, Ру=25бар	14	
		Манометр показывающий Ру=1.6МПа с	28	
		Закладная деталь для установки манометра	28	
		Термометр, d=100, T=50°C	13	
		Закладная деталь для установки термометра	13	
		Этиленгликоль 100% (для разбавления с водой)	1700	лмтр

УСЛОВНЫЕ ОБОЗНАЧЕНИЯ:

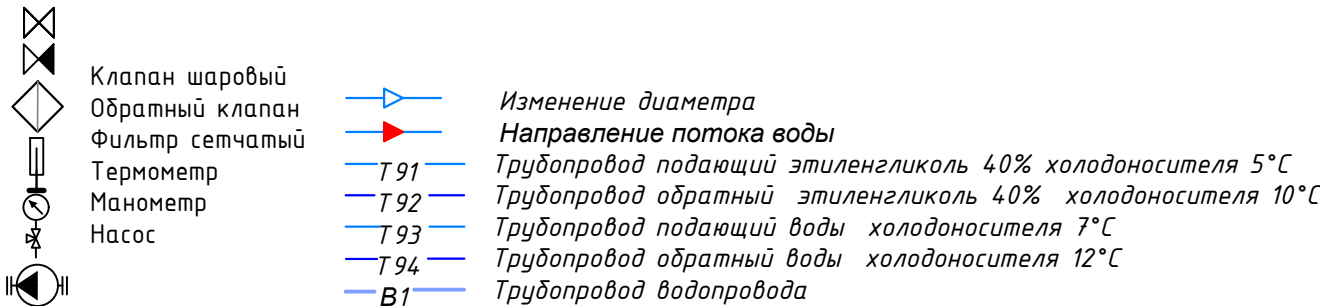

						2/09/ФОК-ХС			
						Корректировка рабочего проекта "Реабилитационно-диагностический центр с гостиницей (Физкультурно-оздоровительный комплекс с гостиницей) город Астана, район Есиль, ул.Хусейн бен Талал, зд.№ 25"			
Изм.	Кол.	N док	Лист	Подпись	Дата	Блоки 1, 2, 3, 4	Стадия	Лист	Листов
							РП	24	
ГИП		Галымжанов	С.Б.		12.25	Индивидуальный холодильный центр. Управление холодоснабжением	ОО "VITALITY GROUP"		
Проверил		Галымжанов	С.Б.		12.25				
Разработал		*****			12.25				

Согласовано Взам. инв. № Подп. и дата Инв. № подл.	Поз.	Наименование и техническая характеристика	Тип, марка, обозначение документа, опросного листа	Код изделия	Поставщик	Ед. изме-ре-ния	Кол-во	Масса 1 ед., кг.	Примечание	
		Холодоснабжение фанкоілов								
		Канальный фанкоіл	МСW200VH			шт	2			
		Канальный фанкоіл	МСW300VH			шт	6			
		Канальный фанкоіл	МСW400VH			шт	8			
		Канальный фанкоіл	МСW500VH			шт	47			
		Канальный фанкоіл	МСW600VH			шт	25			
		Канальный фанкоіл	МСW700VH			шт	33			
		Канальный фанкоіл	МСW800VH			шт	42			
		Канальный фанкоіл	МСW1000VH			шт	14			
		Канальный фанкоіл	МСW1200VH			шт	18			
		Труба стальная сварная водогазопроводная обыкновенная ø20x2,8	ГОСТ 3262-75			м	80.4			
		Труба стальная сварная водогазопроводная обыкновенная ø25x3,2	ГОСТ 3262-75			м	1126.9			
		Труба стальная сварная водогазопроводная обыкновенная ø32x3,2	ГОСТ 3262-75			м	872.3			
		Труба стальная сварная водогазопроводная обыкновенная ø40x3,5	ГОСТ 3262-75			м	290.8			
		Труба стальная электросварная прямошовная ø57x3,5 (ø50)	ГОСТ 10705-80			м	348.8			
		Труба стальная электросварная прямошовная ø76x3,5 (ø65)	ГОСТ 10705-80			м	250.3			
		Труба стальная электросварная прямошовная ø89x3,5 (ø80)	ГОСТ 10705-80			м	52.4			
		Труба стальная электросварная прямошовная ø108x4,5 (ø100)	ГОСТ 10705-80			м	110.3			
		Труба стальная электросварная прямошовная ø127x4,5 (ø125)	ГОСТ 10705-80			м	153.7			
		Труба стальная электросварная прямошовная ø159x4,5 (ø150)	ГОСТ 10705-80			м	121.4			
		Труба стальная электросварная прямошовная ø200x6	ГОСТ 10705-80			м	42.3			
		Труба стальная электросварная прямошовная ø250x7	ГОСТ 10705-80			м	53.7			
		Автоматический комбинированный балансировочный клапан ф15	РИД-AQT-R			шт	36			
		Автоматический комбинированный балансировочный клапан ф20	РИД-AQT-R			шт	155			
		Автоматический комбинированный балансировочный клапан ф25	РИД-AQT-R			шт	17			
								02/09/ФОК-ХС.С		
								Корректировка рабочего проекта“Реабилитационно-диагностический центр с гостиницей (Физкультурно-оздоровительный комплекс с гостиницей) город Астана, район Есиль,ул.Хусейн бен Талал, зд.№ 25”		
				Изм.	Кол.уч.	Лист	№док.	Подп.	Дата	

Согласовано		
Инв. № подл.		
Подп. и дата		
Взам. инв. №		

Поз.	Наименование и техническая характеристика	Тип, марка, обозначение документа, опросного листа	Код изделия	Поставщик	Ед. изме-ре-ния	Кол-во	Масса 1 ед., кг.	Примечание
	Фильтр сетчатый ф20	РИД-FVR-R			шт	11		
	Фильтр сетчатый ф25	РИД-FVR-R			шт	122		
	Фильтр сетчатый ф32	РИД-FVR-R			шт	75		
	Кран шаровый стальной приварной ф20	LD			шт	22		
	Кран шаровый стальной приварной ф25	LD			шт	251		
	Кран шаровый стальной приварной ф32	LD			шт	150		
	Гибкая трубчатая изоляция из вспененного каучука, b=13 мм для ф20				м	80.4		
	Гибкая трубчатая изоляция из вспененного каучука, b=13 мм для ф25				м	1126.9		
	Гибкая трубчатая изоляция из вспененного каучука, b=13 мм для ф32				м	872.3		
	Гибкая трубчатая изоляция из вспененного каучука, b=13 мм для ф40				м	290.8		
	Гибкая трубчатая изоляция из вспененного каучука, b=13 мм для ф50				м	348.8		
	Гибкая трубчатая изоляция из вспененного каучука, b=13 мм для ф65				м	250.3		
	Гибкая трубчатая изоляция из вспененного каучука, b=13 мм для ф80				м	52.4		
	Гибкая трубчатая изоляция из вспененного каучука, b=13 мм для ф100				м	110.3		
	Гибкая трубчатая изоляция из вспененного каучука, b=13 мм для ф125				м	153.7		
	Гибкая трубчатая изоляция из вспененного каучука, b=13 мм для ф150				м	121.4		
	Гибкая трубчатая изоляция из вспененного каучука, b=13 мм для ф200				м	42.3		
	Гибкая трубчатая изоляция из вспененного каучука, b=13 мм для ф250				м	53.7		
	Крепление труб				кг	1922.9		

						Спецификация оборудования, материалов и изделий.	ХС.СО	Лист
								2
Изм.	Кол.уч	Лист	Ндок.	Подп.	Дата			

Согласовано				
Инв. № подл.	Подп. и дата	Взам. инв. №		

Поз.	Наименование и техническая характеристика	Тип, марка, обозначение документа, опросного листа	Код изделия	Поставщик	Ед. изме-ре-ния	Кол-во	Масса 1 ед., кг.	Примечание
	Система слива дренажа							
	Труба дренажная пролипроленовая Ø32x4,4				м	1200		
	Труба дренажная пролипроленовая Ø40x5,5				м	110		
	Труба дренажная пролипроленовая Ø50x6,9				м	30		
	Сухой Гидравлический затвор DN32				шт	48		
	Сухой Гидравлический затвор DN40				шт	8		
	Сухой Гидравлический затвор DN50				шт	3		

						Спецификация оборудования, материалов и изделий.	ХС.СО	Лист
								3
Изм.	Кол.уч	Лист	Ндок.	Подп.	Дата			

		Поз.	Наименование и техническая характеристика	Тип, марка, обозначение документа, опросного листа	Код продукции	Поставщик	Единица измерения	Количество	Масса 1 ед., кг	Примечание
			Холодоснабжение приточных установок							
			Узел обвязки холодоснабжения приточной установки П1:							
			Автоматический балансировочный клапан Dn15	AB-QM		T00 "Danfoss"	шт.	1		
			Кран шаровый латунный муфтовый Dn20	VT.214.N.05		T00 "Valtec"	шт.	2		
			Косой сетчатый фильтр, Dn20; Pn=20бар; t=+5...+150°C	Y222		T00 "Danfoss"	шт.	1		
			Узел обвязки холодоснабжения приточной установки П2:							
			Автоматический балансировочный клапан Dn15	AB-QM		T00 "Danfoss"	шт.	1		
			Кран шаровый латунный муфтовый Dn25	VT.214.N.05		T00 "Valtec"	шт.	2		
			Косой сетчатый фильтр, Dn25; Pn=20бар; t=+5...+150°C	Y222		T00 "Danfoss"	шт.	1		
			Узел обвязки холодоснабжения приточной установки П3:							
			Автоматический балансировочный клапан Dn20	AB-QM		T00 "Danfoss"	шт.	1		
			Кран шаровый латунный муфтовый Dn32	VT.214.N.05		T00 "Valtec"	шт.	2		
			Косой сетчатый фильтр, Dn32; Pn=20бар; t=+5...+150°C	Y222		T00 "Danfoss"	шт.	1		
			Узел обвязки холодоснабжения приточной установки П4:							
			Автоматический балансировочный клапан Dn25	AB-QM		T00 "Danfoss"	шт.	1		
			Кран шаровый латунный муфтовый Dn32	VT.214.N.05		T00 "Valtec"	шт.	2		
			Косой сетчатый фильтр, Dn32; Pn=20бар; t=+5...+150°C	Y222		T00 "Danfoss"	шт.	1		
			Узел обвязки холодоснабжения приточной установки П5:							
			Автоматический балансировочный клапан Dn15	AB-QM		T00 "Danfoss"	шт.	1		
			Кран шаровый латунный муфтовый Dn25	VT.214.N.05		T00 "Valtec"	шт.	2		
			Косой сетчатый фильтр, Dn25; Pn=20бар; t=+5...+150°C	Y222		T00 "Danfoss"	шт.	1		
			Узел обвязки холодоснабжения приточной установки П6:							
Инв. подг.	Взам. инв.		Автоматический балансировочный клапан Dn15	AB-QM		T00 "Danfoss"	шт.	1		
			Кран шаровый латунный муфтовый Dn25	VT.214.N.05		T00 "Valtec"	шт.	2		
			Косой сетчатый фильтр, Dn25; Pn=20бар; t=+5...+150°C	Y222		T00 "Danfoss"	шт.	1		
	Погн. и дата		Узел обвязки холодоснабжения приточной установки П7:							
			Автоматический балансировочный клапан Dn15	AB-QM		T00 "Danfoss"	шт.	1		
			Кран шаровый латунный муфтовый Dn20	VT.214.N.05		T00 "Valtec"	шт.	2		
			Косой сетчатый фильтр, Dn20; Pn=20бар; t=+5...+150°C	Y222		T00 "Danfoss"	шт.	1		
						Рук.зр.				Лист
						Провер.				3
						Состав.				

Спецификация оборудования и материалов

ФОРМАТ А3

Поз.		Наименование и техническая характеристика	Тип, марка, обозначение документа, опросного листа	Код продукции	Поставщик	Единица измерения	Количество	Масса 1 ед., кг	Примечание
		Холодоснабжение приточных установок							
		Узел обвязки холодоснабжения приточной установки П8:							
		Автоматический балансировочный клапан Dn20	AB-QM		T00 "Danfoss"	шт.	1		
		Кран шаровый латунный муфтовый Dn32	VT.214.N.05		T00 "Valtec"	шт.	2		
		Косой сетчатый фильтр, Dn32; Pn=20бар; t=+5...+150°C	Y222		T00 "Danfoss"	шт.	1		
		Узел обвязки холодоснабжения приточной установки П9:							
		Автоматический балансировочный клапан Dn20	AB-QM		T00 "Danfoss"	шт.	1		
		Кран шаровый латунный муфтовый Dn25	VT.214.N.05		T00 "Valtec"	шт.	2		
		Косой сетчатый фильтр, Dn25; Pn=20бар; t=+5...+150°C	Y222		T00 "Danfoss"	шт.	1		
		Узел обвязки холодоснабжения приточной установки П10:							
		Автоматический балансировочный клапан Dn15	AB-QM		T00 "Danfoss"	шт.	1		
		Кран шаровый латунный муфтовый Dn20	VT.214.N.05		T00 "Valtec"	шт.	2		
		Косой сетчатый фильтр, Dn20; Pn=20бар; t=+5...+150°C	Y222		T00 "Danfoss"	шт.	1		
		Узел обвязки холодоснабжения приточной установки П11:							
		Автоматический балансировочный клапан Dn20	AB-QM		T00 "Danfoss"	шт.	1		
		Кран шаровый латунный муфтовый Dn25	VT.214.N.05		T00 "Valtec"	шт.	2		
		Косой сетчатый фильтр, Dn25; Pn=20бар; t=+5...+150°C	Y222		T00 "Danfoss"	шт.	1		
		Узел обвязки холодоснабжения приточной установки П12:							
		Автоматический балансировочный клапан Dn20	AB-QM		T00 "Danfoss"	шт.	1		
		Кран шаровый латунный муфтовый Dn25	VT.214.N.05		T00 "Valtec"	шт.	2		
		Косой сетчатый фильтр, Dn25; Pn=20бар; t=+5...+150°C	Y222		T00 "Danfoss"	шт.	1		
		Узел обвязки холодоснабжения приточной установки ПВ1:							
		Автоматический балансировочный клапан Dn20	AB-QM		T00 "Danfoss"	шт.	1		
		Кран шаровый латунный муфтовый Dn25	VT.214.N.05		T00 "Valtec"	шт.	2		
		Косой сетчатый фильтр, Dn25; Pn=20бар; t=+5...+150°C	Y222		T00 "Danfoss"	шт.	1		
		Узел обвязки холодоснабжения приточной установки ПВ2:							
		Автоматический балансировочный клапан Dn32	AB-QM		T00 "Danfoss"	шт.	1		
		Кран шаровый латунный муфтовый Dn40	VT.214.N.05		T00 "Valtec"	шт.	2		
		Косой сетчатый фильтр, Dn40; Pn=20бар; t=+5...+150°C	Y222		T00 "Danfoss"	шт.	1		
Инв. подг.	Погн. и дата	Взам. инв.							
			Рук.зр.				Спецификация оборудования и материалов		Лист
			Провер.						4
			Состав.						

Поз.		Наименование и техническая характеристика	Тип, марка, обозначение документа, опросного листа	Код продукции	Поставщик	Единица измерения	Количество	Масса 1 ед., кг	Примечание
		Холодоснабжение приточных установок							
		Узел обвязки холодоснабжения приточной установки ПВ3:							
		Автоматический балансировочный клапан Dn15	AB-QM		T00 "Danfoss"	шт.	1		
		Кран шаровый латунный муфтовый Dn20	VT.214.N.05		T00 "Valtec"	шт.	2		
		Косой сетчатый фильтр, Dn20; Pn=20бар; t=+5...+150°C	Y222		T00 "Danfoss"	шт.	1		
		Узел обвязки холодоснабжения приточной установки ПВ4:							
		Автоматический балансировочный клапан Dn15	AB-QM		T00 "Danfoss"	шт.	1		
		Кран шаровый латунный муфтовый Dn20	VT.214.N.05		T00 "Valtec"	шт.	2		
		Косой сетчатый фильтр, Dn20; Pn=20бар; t=+5...+150°C	Y222		T00 "Danfoss"	шт.	1		
		Узел обвязки холодоснабжения приточной установки ПВ7:							
		Автоматический балансировочный клапан Dn25	AB-QM		T00 "Danfoss"	шт.	1		
		Кран шаровый латунный муфтовый Dn32	VT.214.N.05		T00 "Valtec"	шт.	2		
		Косой сетчатый фильтр, Dn32; Pn=20бар; t=+5...+150°C	Y222		T00 "Danfoss"	шт.	1		
		Узел обвязки холодоснабжения приточной установки ПВ8:							
		Автоматический балансировочный клапан Dn20	AB-QM		T00 "Danfoss"	шт.	1		
		Кран шаровый латунный муфтовый Dn25	VT.214.N.05		T00 "Valtec"	шт.	2		
		Косой сетчатый фильтр, Dn25; Pn=20бар; t=+5...+150°C	Y222		T00 "Danfoss"	шт.	1		
		Узел обвязки холодоснабжения ОС1:							
		Автоматический балансировочный клапан Dn32	AB-QM		T00 "Danfoss"	шт.	1		
		Кран шаровый латунный муфтовый Dn40	VT.214.N.05		T00 "Valtec"	шт.	2		
		Косой сетчатый фильтр, Dn40; Pn=20бар; t=+5...+150°C	Y222		T00 "Danfoss"	шт.	1		
		Узел обвязки холодоснабжения ОС2:							
		Автоматический балансировочный клапан Dn32	AB-QM		T00 "Danfoss"	шт.	1		
		Кран шаровый латунный муфтовый Dn40	VT.214.N.05		T00 "Valtec"	шт.	2		
		Косой сетчатый фильтр, Dn40; Pn=20бар; t=+5...+150°C	Y222		T00 "Danfoss"	шт.	1		
		Узел обвязки холодоснабжения приточных установки П9,1:							
		Автоматический балансировочный клапан Dn25	AB-QM		T00 "Danfoss"	шт.	1		
		Кран шаровый латунный муфтовый Dn32	VT.214.N.05		T00 "Valtec"	шт.	2		
		Косой сетчатый фильтр, Dn32; Pn=20бар; t=+5...+150°C	Y222		T00 "Danfoss"	шт.	1		
Инв. подг.	Погн. и дата	Взам. инв.							
			Рук.зр.				Спецификация оборудования и материалов		Лист
			Провер.						5
			Состав.						

