

Товарищество с ограниченной ответственностью «Vitallity Group»

Рабочий проект

“Физкультурно-оздоровительный комплекс, город Нур-Султан,
район Есиль, ул. Хусейн бен Талал, зд. №25. (корректировка)”

Шифр – ХС

Том *

Альбом *

Директор



Темралинов Д.А.

Главный инженер проекта



Галымжанов С.Н.

г. Астана – 2026 год

Товарищество с ограниченной ответственностью «Vitallity Group»

Рабочий проект

“Физкультурно-оздоровительный комплекс, город Нур-Султан,
район Есиль, ул. Хусейн бен Талал, зд. №25. (корректировка)”

Шифр – ХС

Том *

Альбом *

г. Астана – 2026 год

Кондиционирование
Проектные решения по кондиционированию приняты с целью обеспечения нормативных параметров микроклимата в помещениях в тёплый период года и межсезонье, в соответствии с функциональным назначением помещений.

В качестве хладагента применяется фреон марки R410A. Внутренние блоки системы – кассетного типа.

Фреоноводы выполнены из медных труб марки EN 12735-1.

Сброс дренажа в канализацию предусмотреть через гидрозатвор (сифон).

Системами кондиционирования воздуха оснащаются помещения с постоянным и периодическим пребыванием людей, а также помещения с повышенными тепловыделениями, в том числе:

- Размещение внутренних блоков выполнено:
в подвесных потолках;
в технических зонах с возможностью сервисного доступа.

Принятые системы кондиционирования характеризуются:


- высоким коэффициентом энергоэффективности;
- возможностью поэтапного включения оборудования;
- автоматическим поддержанием заданных параметров температуры;
- надёжной и безопасной эксплуатацией.

Главный инженер проекта

Галымжанов С.


							-ХС		
							Физкультурно –оздоровительный комплекс с гостиницей город Астана , район Есиль , ул . Хусейн бен Талал , зд . №25		
Изм.	Кол.	№ док	Лист	Подпись	Дата				
ГИП		Галымжанов	С.		02.26	Физкультурно-оздоровительный комплекс (блоки 1, 2, 3, 4)	Стадия	Лист	Листов
Проверил		Галымжанов	С.		02.26		РП	*	
Разработал		-			02.26				
						Общие данные	T00 "Vitality Group"		

План подвала

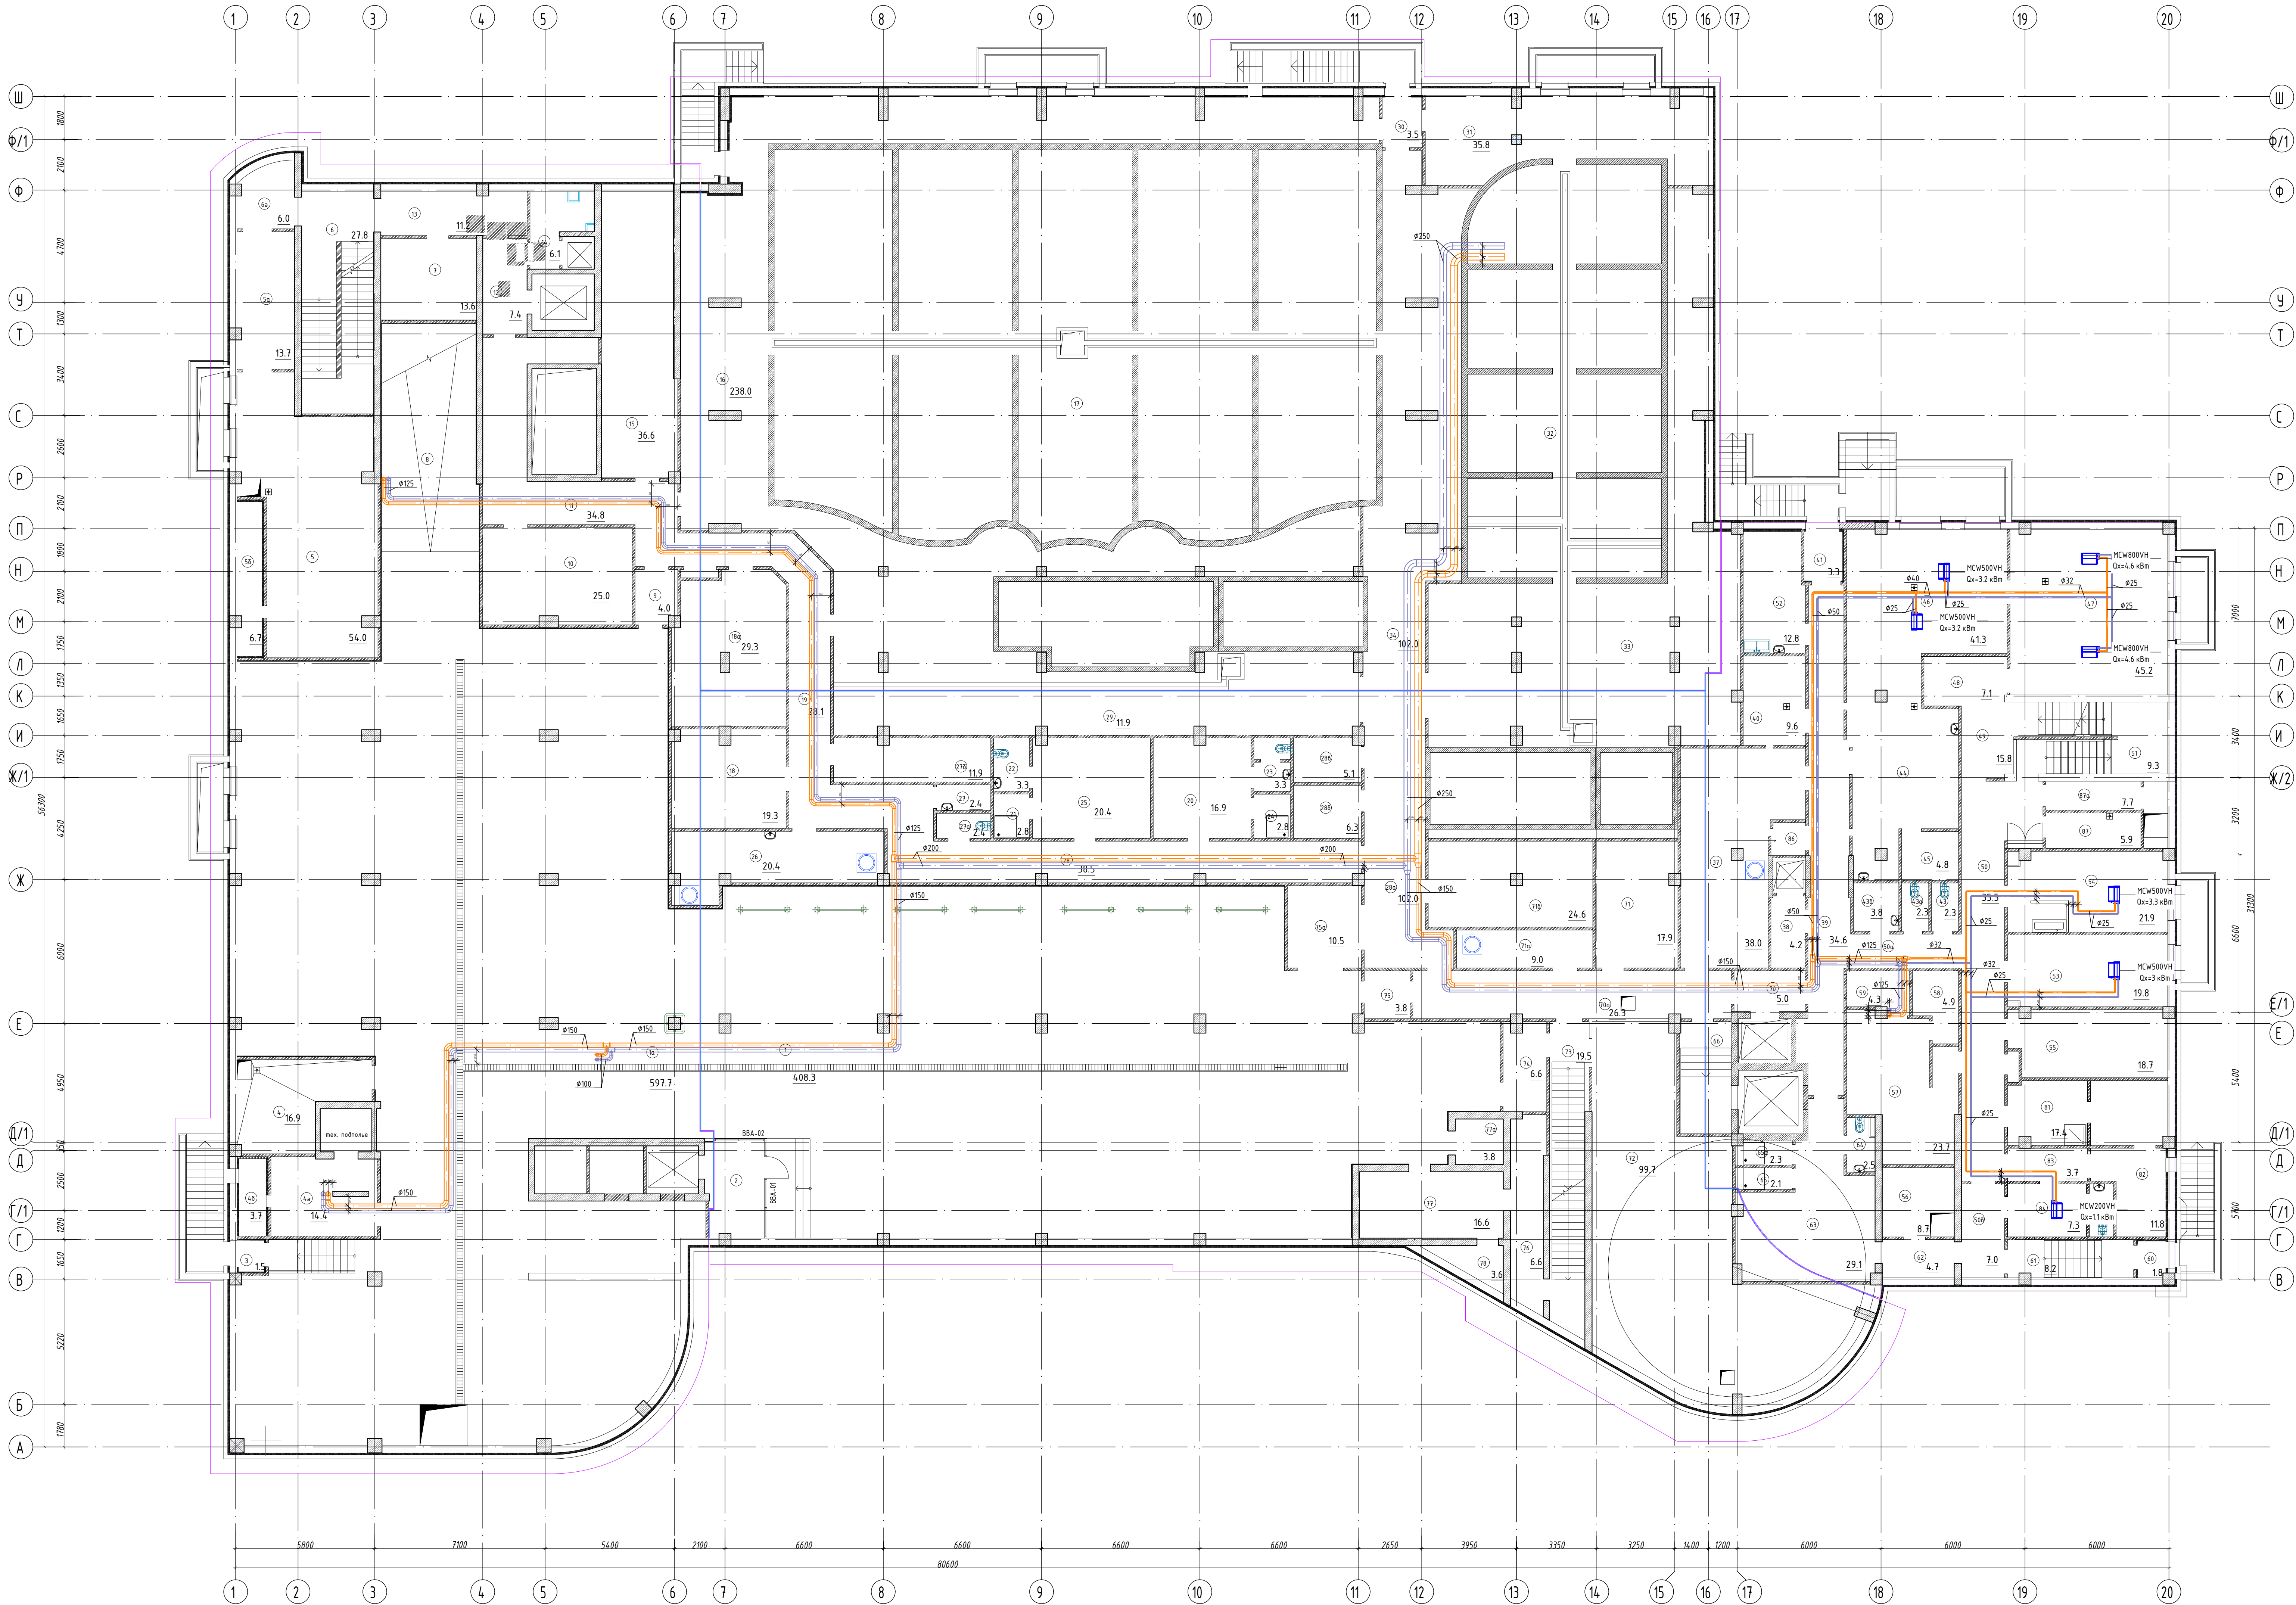


Экспликация помещений (начало)				Экспликация помещений (окончание)			
Поз.	Наименование	Площа- дь м2	Кол. поме- ний	Поз.	Наименование	Площа- дь м2	Кол. поме- ний
1	Паркинг	408.3		44	Пом. приема и разбора грязного белья	26.3	
1а	Паркинг	597.7		45	Пом. уборочного инвентаря	4.8	
2	Танбур с подпором воздуха	9.7		46	Помещение постирочной	41.3	
3	Танбур	15		47	Гладильная	45.2	
4	Тех. помещение	16.9		48	Помещение разборки, упаковки чистого белья	7.1	
4а	Венткамера	3.7		49	Выбоч. чистого белья	35.8	
4б	Вентшахта	14.4		50	Коридор	35.5	
5	Венткамера	54.0		50а	Коридор	6.5	
5а	Тех. помещение	6.7		50б	Коридор	7.0	
5б	Вентшахта	13.7		51	Лестничная клетка	9.3	
6	Лестничная клетка	27.8		52	Холод. камера хранения мед. отходов	12.9	
6а	Кладовая	6.0		53	Комн. отдыха и приема пищи	19.8	
7	Кладовая	13.6		54	Намаз хана	21.9	
8	Танбур с подпором воздуха	50.9		55	Кладовая запаса чистого йодированной белья	18.7	
9	Танбур с подпором воздуха	4.0		56	Гардероб верхней одежды медперсонала	8.7	
10	Серверная	25.0		57	Раздевальня медперсонала (Мужской)	23.7	
11	Коридор	34.8		58	Душевая	4.9	
12	Танбур с подпором воздуха	7.4		59	Сан.узел	4.3	
13	Коридор	11.2		60	Танбур	1.8	
14	Загрузочная	6.1		61	Лестница	8.2	
15	Архив	36.6		62	Коридор	4.7	
16	Тех. подполье	238.0		63	Раздевальня медперсонала (Женский)	29.1	
17	Тех. подполье	378.5		64	Сан.узел	2.5	
18	Кладовая	19.3		65	Душевая	2.1	
18а	Электрощитовая	29.3		65а	Душевая холл	2.3	
19	Коридор	28.1		66	Лифтовой холл	10.0	
20	Гардеробная	16.9		70	Танбур с подпором	5.0	
21	Душевая	2.1		70а	Коридор	26.3	
22	Сан.узел	3.3		71	Насосная АПТ	17.9	
23	Сан.узел	3.3		71а	Пом. сбора грязного белья	9.0	
24	Душевая	2.8		71б	Насосная АПТ	24.6	
25	Гардеробная	20.4		72	Насосная, тепловой узел	99.7	
26	Пом. сбора грязного белья	20.4		73	Лестничная клетка	19.5	
27	Пом. уборочного инвентаря	2.4		74	Танбур с подпором воздуха	6.6	
27а	Сан.узел	2.4		75	Танбур с подпором воздуха	3.8	
27б	Гардеробная	11.9		75а	Танбур с подпором воздуха	10.5	
28	Коридор	38.5		76	Тех. подполье	6.6	
28а	Коридор	102.0		77	Тех. подполье	16.6	
28б	Хранение реагентов	6.3		77а	Тех. подполье	3.8	
28в	Хранение реагентов	5.1		78	Тех. подполье	3.6	
29	Узел управления бассейном	11.9		81	Пом. приема и дезинфекции и стерилизации	17.4	
30	Танбур	3.5		82	Пом. хранения мед.инвент.	11.8	
31	Техническое помещение	35.8		83	Сан.узел. Душевая.	3.7	
32	Техническое помещение	109.1		84	Охрана	7.3	
33	Узел управления бассейном	112.7		86	Помещен. хранения тележек	1.9	
34	Коридор	102.0		87	Пом. стерилизации и хранения мед.инвент.	5.9	
37	Пом. временного хранения грязного белья	38.0		87а	Помещение выбоч. чистого белья (Ветское)	7.7	
38	Танбур с подпором	4.2					
39	Коридор	34.6					
40	Холод. камера хранения ТБО	9.6					
41	Танбур	3.3					
43	Сан.узел	2.3					
43а	Сан.узел	2.3					
43б	Комната убороч. инвентаря	3.8					

СХЕМА БЛОКИРОВКИ

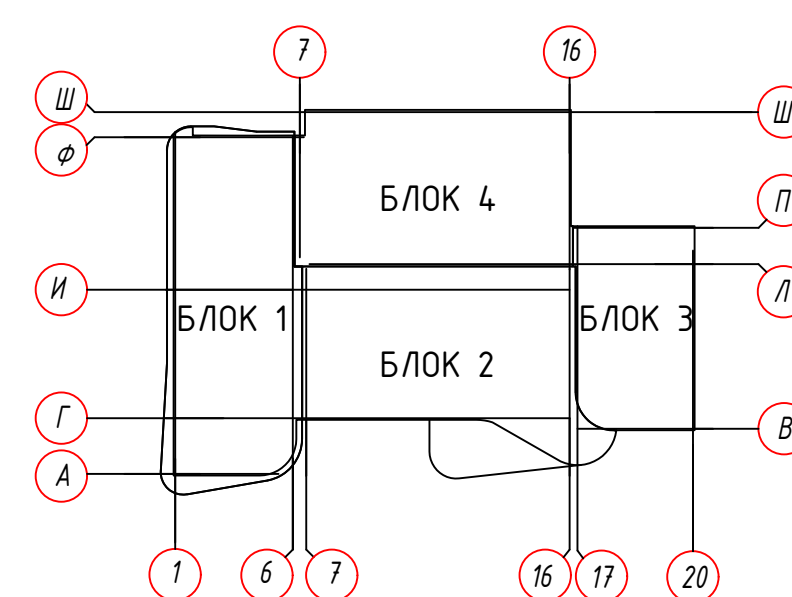


				-ХС			
				Физкультурно-оздоровительный комплекс с гостиницей город Астана, район Есиль, ул. Хусейн Ван Талая, зд. №25			
Изм.	Кол.	И. Дир.	Лист	Подпись	Дата	Специальность	Лист
ГМП	Галижанов	С.	02.26	02.26	02.26	Физкультурно-оздоровительный комплекс (Блоки 1, 2, 3, 4)	РП
Проверил							
Разработчик							
				Одобрено: план подвала на оп. -4,050			
				100 "Vitality Group"			

План 1 этажа

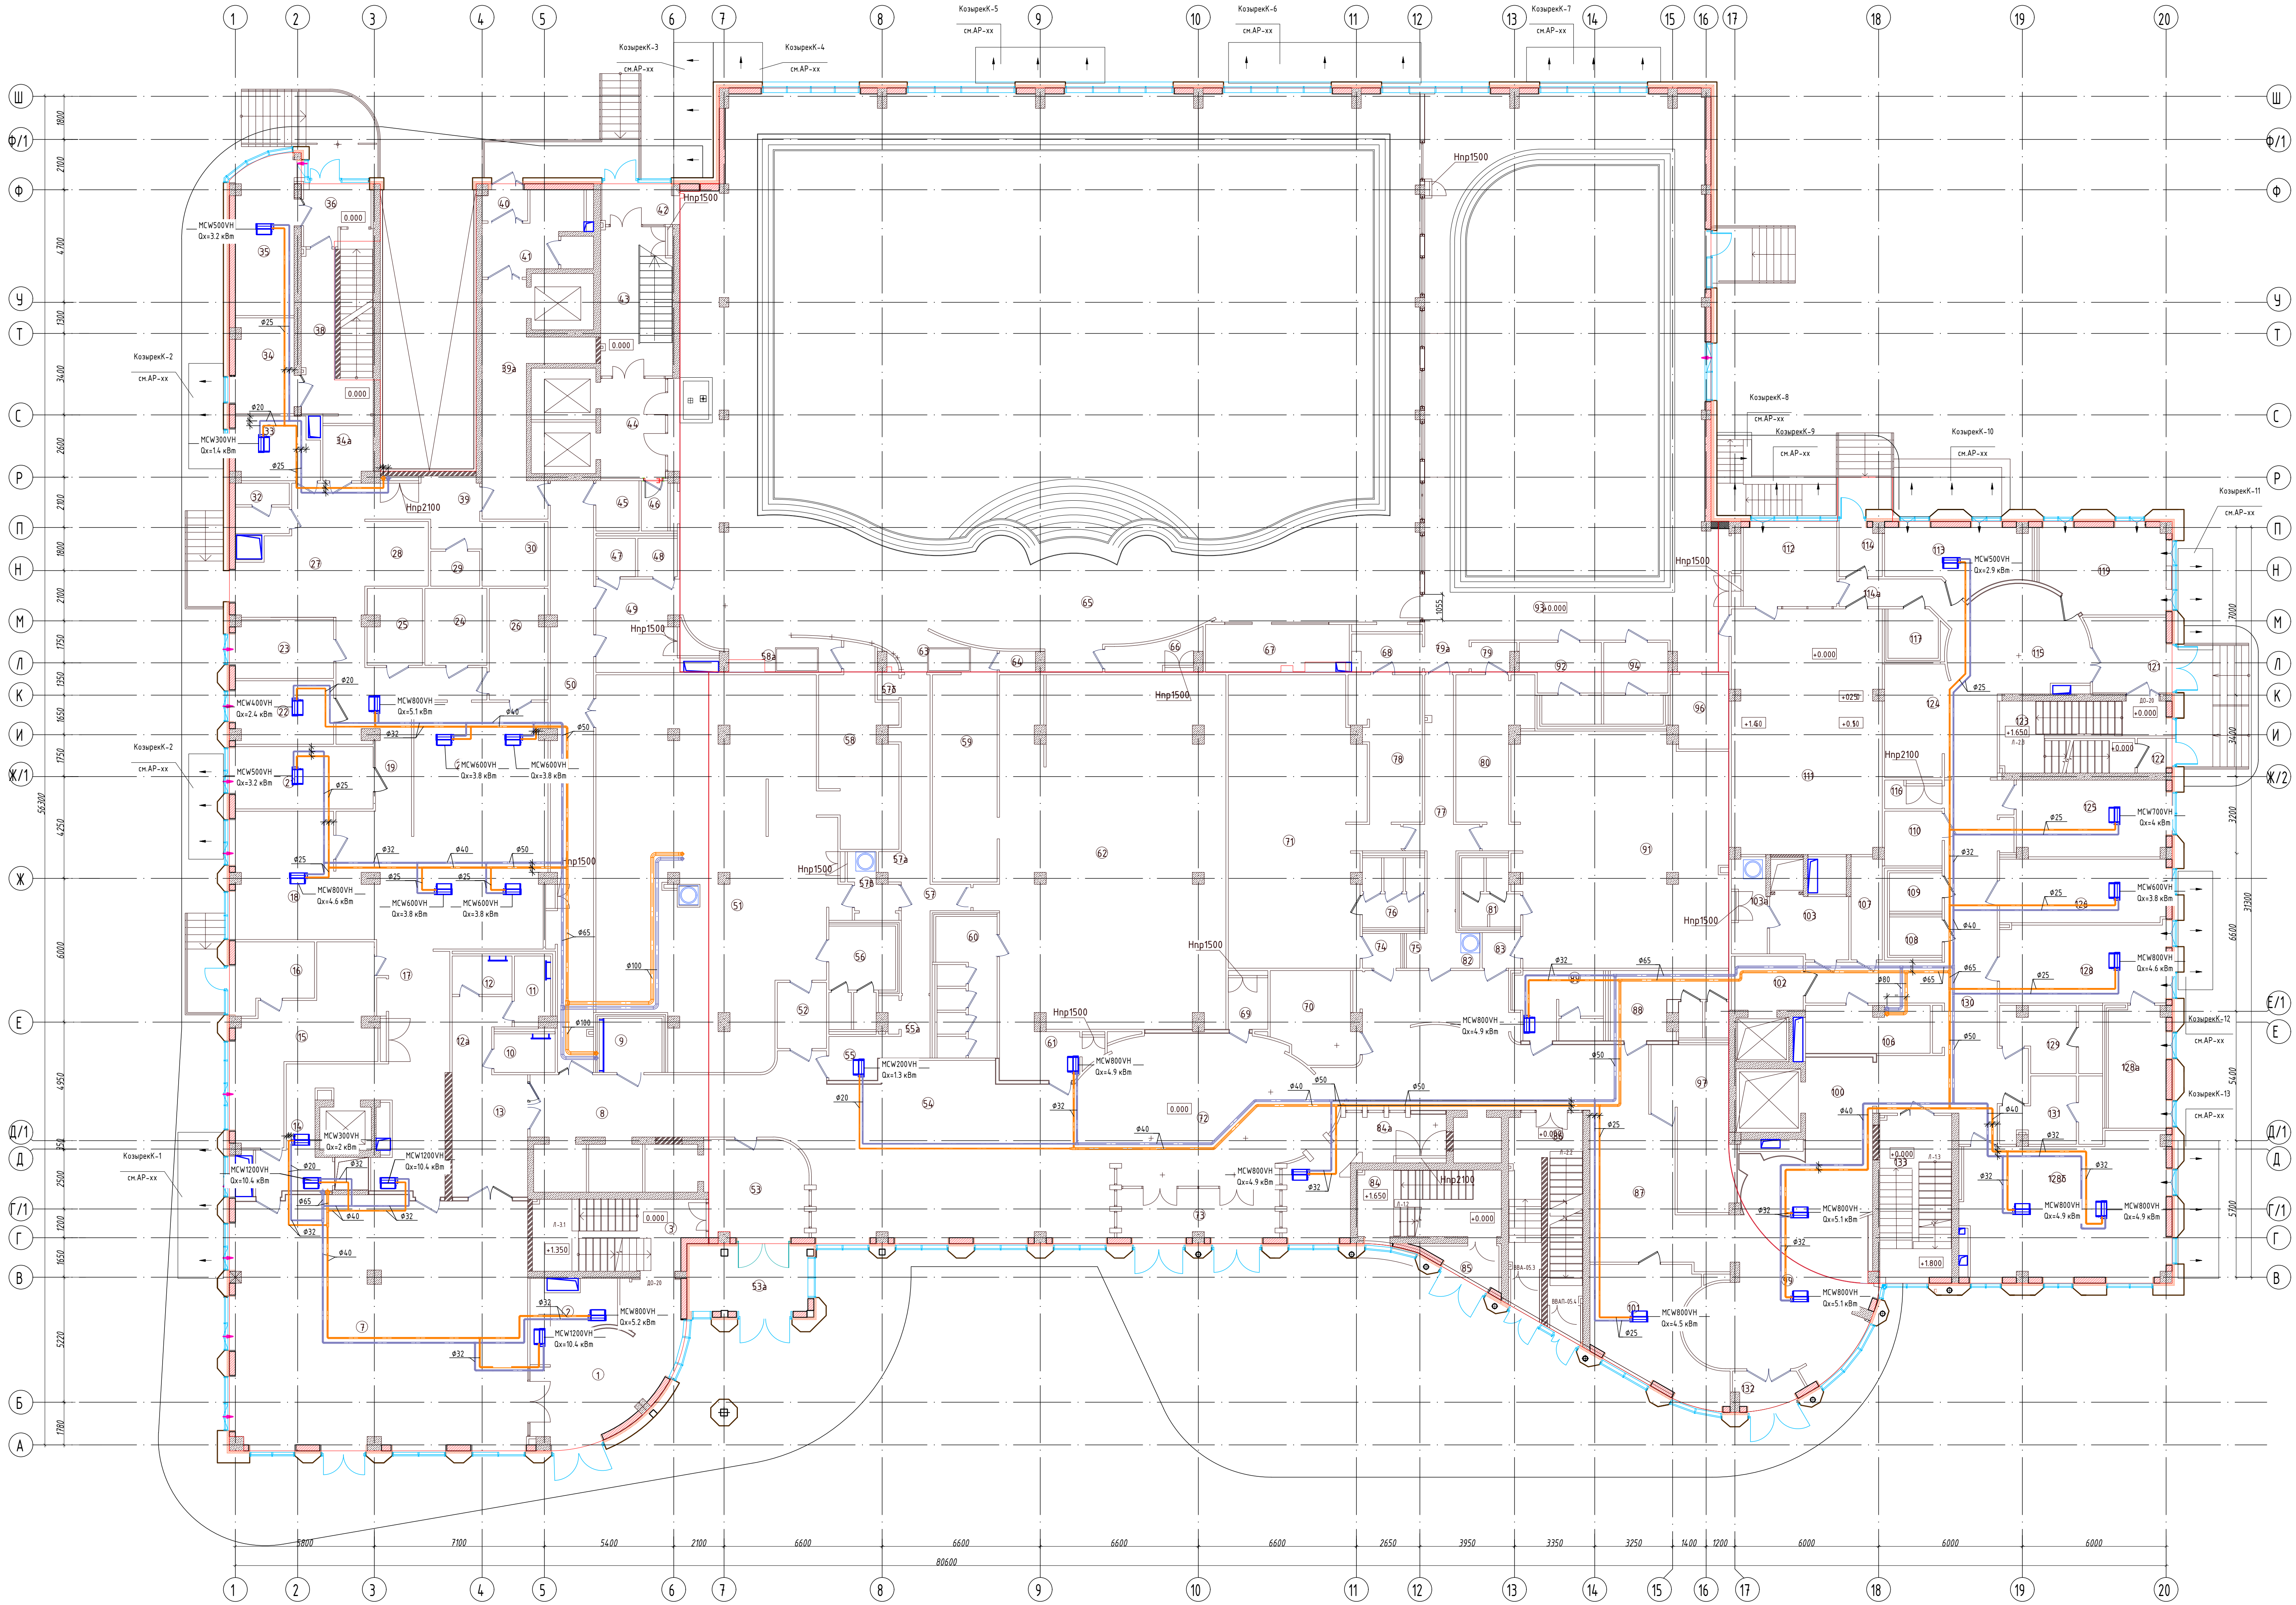


Экспликация помещений (начало)				Экспликация помещений (окончание)			
Поз	Наименование	площадь	Кат. помещ.	Поз	Наименование	площадь	Кат. помещ.
1	Ресепшен	26.0		60	Санузел	15.1	
2	Гардероб	8.9		61	Тамбур	7.5	
3	Лестница	20.3		61а	Посадочное помещение	1.2	
7	Обеденный зал	129.2		62	Раздевалка женская	14.4	
8	Холл	18.8		63	Тамбур	3.9	
9	Санузел МГН	5.9		64	Тех.помещение	1.5	
10	Санузел	4.10		65	Бассейн	694.3	
11	Санузел	4.2		66	Тех.помещение	5.0	
12	Санузел	4.0		67	Баня финская	9.3	
12а	Тамбур	6.4		68	Тамбур	4.4	
13	Холл	16.1		69	Посадочное помещение	4.0	
14	Коридор	9.8		70	Окна	12.7	
15	Мясная столовая посуды	28.0		71	Раздевалка дев.	68.9	
16	Тамбур	8.9		72	Холл	195.9	
17	Раздаточная	31.7		73	Тамбур	15.0	
18	Холодный цех	22.8		74	Тамбур	2.2	
19	Коридор	20.6		75	К/И	1.4	
20	Горячий цех	74.6		76	Санузел	7.3	
21	Мясной цех	15.5		77	Тех.помещение	12.1	
22	Рыбный цех	11.1		78	Душевые	15.6	
23	Кладовая	10.4		79а	Тамбур	2.5	
24	Общедоступный цех	8.2		80	Душевые	16.5	
25	Кладовая общей	7.1		81	Санузел	6.7	
26	Мясная кухонная посуды	16.1		82	Пом. Бельевого	4.1	
27	Загрузочная	11.2		83	Тамбур	2.4	
28	Холодильная камера	7.2		84	Лестница	16.6	
29	Кладовая	3.0		84а	Отдел продаж	19.1	
30	Холодильная камера	7.5		85	Тамбур	19.1	
32	Санузел	4.6		86	Лестница	21.1	
33	Заб. производством	9.2		87	Коридор	27.5	
34	Гардероб персонала	9.9		88	Санузел женский	13.4	
34а	Кладовая	4.6		89	Санузел мужской	10.2	
35	Помещение охраны	16.0		91	Раздевалка для мальчиков	87.0	
36	Тамбур	6.3		92	Тренировочная ж.	9.7	
38	Лестница	20.1		93	Бассейн детский	275.4	
39	Коридор	6.9		94	Тренировочная муж.	8.7	
39а	Коридор	23.1		96	Баня детская	7.3	
40	Тамбур	2.4		97	Гардероб	19.0	
41	Загрузочная	12.2		99	Холл	50.8	
42	Тамбур	5.5		100	Вестибюль	22.5	
43	Лестница	18.6		101	Отдел продаж	6.8	
44	Лифтовой холл	11.3		102	Лифтовой холл	5.8	
45	Лаборатория	3.8		103	К/И	8.4	
46	К/И	2.3		103а	Бельевого	5.9	
47	Санузел	2.6		106	Помещение стерилизации мед.инвентаря и пригот. физрастворов	10.1	
48	Санузел	2.6		107	Тех.помещение	5.5	
49	Фитобар	15.4		108	Санузел	3.5	
50	Коридор	42.9		109	Санузел	3.5	
51	Раздевалка мужская	145.0		110	Санузел МГН	5.5	
52	Тамбур	5.6		111	Бассейн	64.1	
53	Вход	17.5		112	Раздевалка для юристов	13.9	
53а	Тамбур	13.5		113	Кабинет врача остеопата	14.6	
54	Бар	12.7		114	Тамбур	4.0	
55	Коридор	5.5		114а	Тамбур	12.5	
55а	К/И	2.8		115	Холл	22.5	
56	Санузел	10.5		116	К/И	2.9	
57	Коридор	15.2		117	Комната матери и ребенка	4.2	
57а	К/И	1.0		119	Пом. эрудитового массажа и гимнастики	18.9	
57б	К/И	0.9		121	Тамбур	10.6	
57б	Пом. Бельевого	4.3		122	Тамбур	2.2	
58	Душевые	20.2		123	Лестница	18.6	
58а	Тамбур	16.1		124	Гардероб	19.9	
59	Душевые	23.4		125	Кабинет врача остеопата	20.2	
				126	Кабинет врача терапевта	18.7	
				128	Кабинет врача хиропраكتера/Реабилитолога	23.1	
				128а	Помещение массажа	23.1	
				128б	Помещение электро-физиотерапии	48.9	
				129	Раздев. Мужская с душевой	10.3	
				130	Коридор	55.3	
				131	Раздев. Женская с душевой	10.1	
				132	Тамбур	4.4	
				133	Лестница	20.7	

СХЕМА БЛОКИРОВКИ

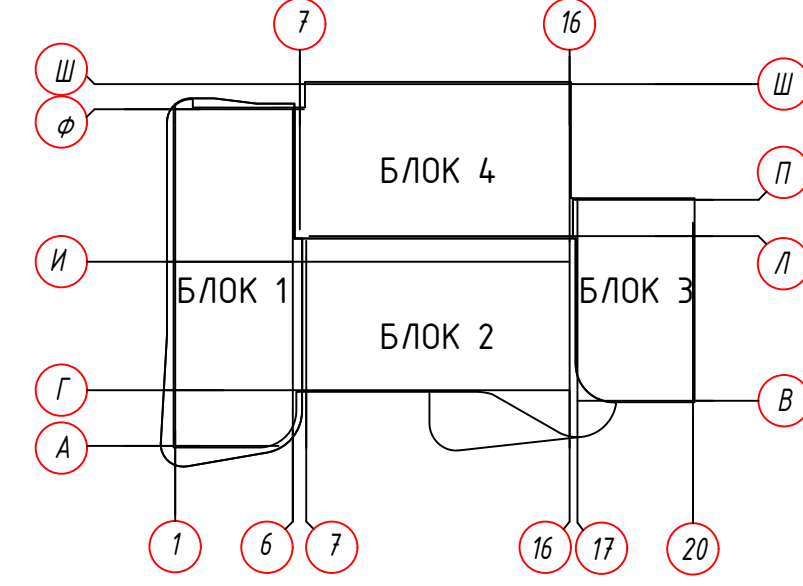


				-ХС			
				Физкультурно-оздоровительный комплекс с санаторной горой Астана, район Есиль, ул. Хусейн Ван Тала, зд. №25			
Изм.	Кол.	№ док.	Лист	Подпись	Дата	Лист	Лист
ГМП	Галкина	С.	02.26		02.26		
Проектировщик							
Разработчик							
				Физкультурно-оздоровительный комплекс (блоки 1, 2, 3, 4)			
				Одобрено на оп. -4,050			
				100 "Vitality Group"			

План тех. этажа

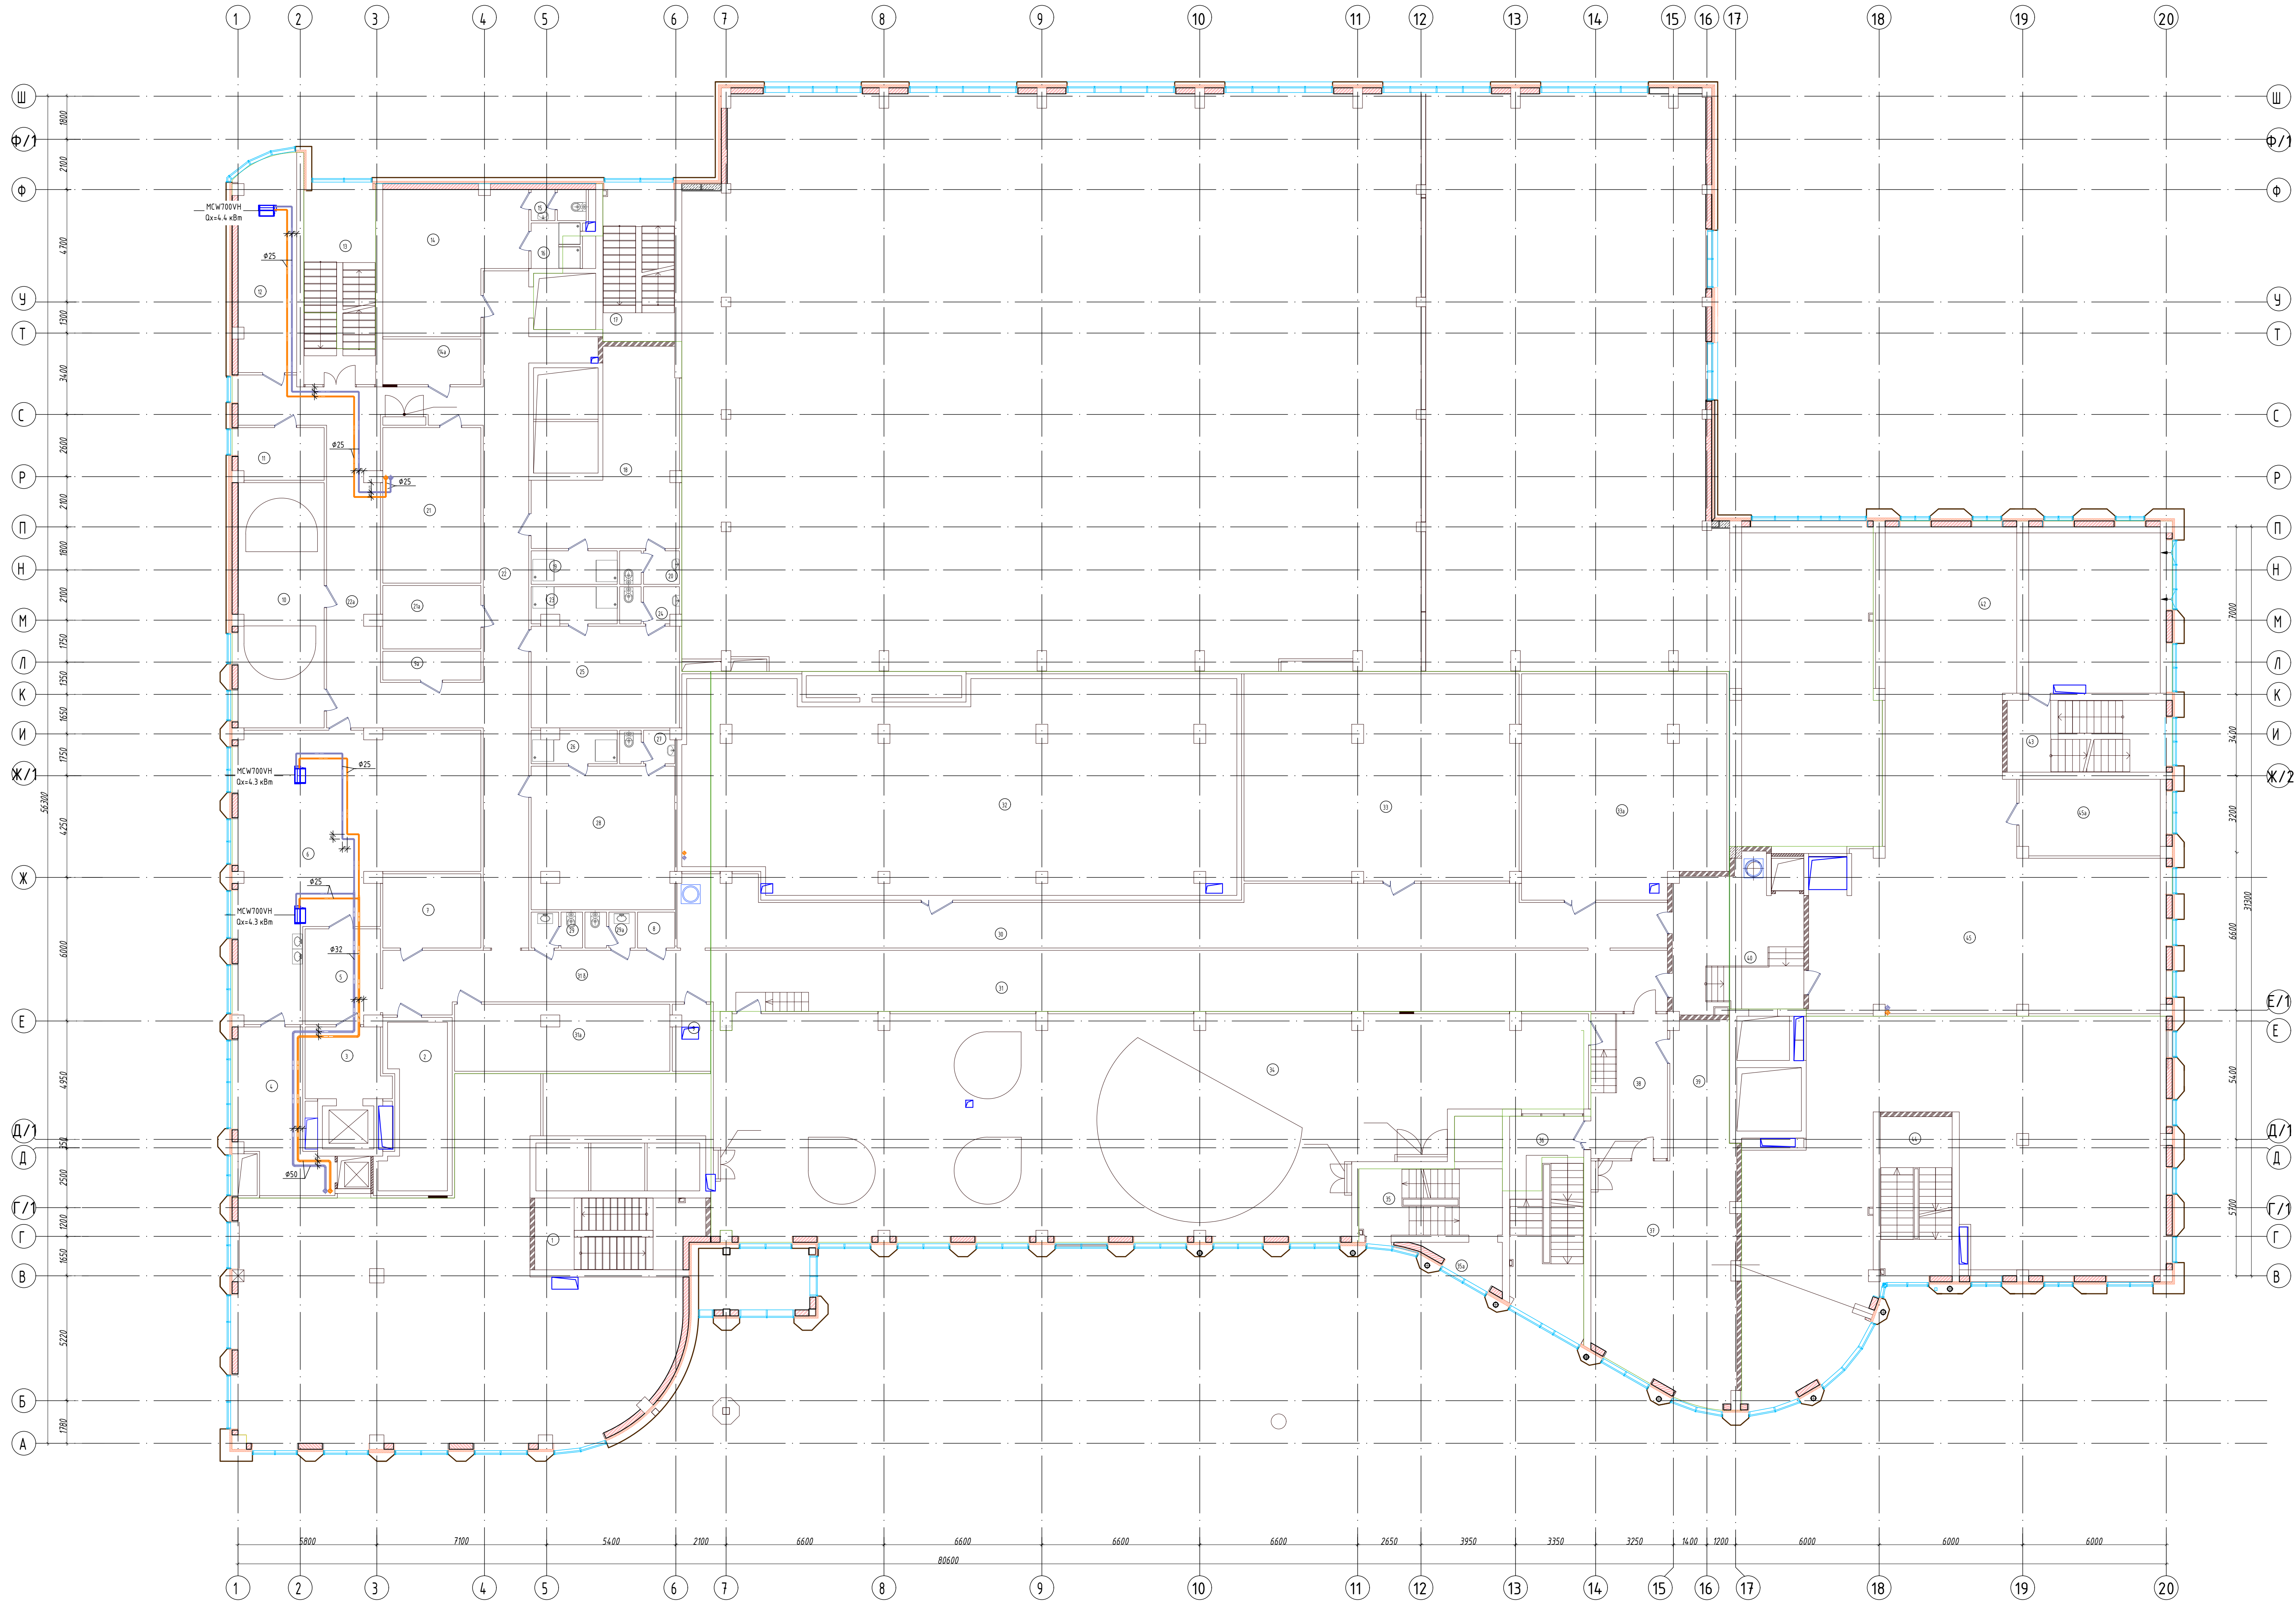

Экспликация помещений			
Поз	Наименование	площадь	Кот. помеще-ния
1	Лестничная клетка	20.1	
2	Венкамера	20.6	
3	Сервировочная	9.9	
4	Моечная	20.9	
5	Сервировочная	12.3	
6	Столовая персонала	86.1	
7	Пом. Официантов	12.70	
8	Тех.помещение	2.3	
9	Кухня	4.30	
9а	Тех.помещение	4.9	
10	Тех.помещение	37.60	
11	Тех.помещение	8.20	
12	Диспетчерская	21.7	
13	Лестничная клетка	25.2	
14	Гардеробная	31.70	
14а	Курительная	7.80	
15	Санузел	2.9	
16	Душевая	3.80	
17	Лестничная клетка	19.9	
18	Гардеробная	35.1	
19	Душевая	5.0	
20	Санузел	3.4	
21	Комната тренинга персонала	26.60	
22	Коридор	53.8	
22а	Коридор	52.70	
23	Душевая	53	
24	Санузел	3.6	
25	Гардеробная	26.40	
26	Душевая	4.70	
27	Санузел	3.1	
28	Гардеробная	35.9	
29	Санузел	3.2	
29а	Санузел	3.1	
30	Коридор	91.7	
31	Коридор	101.9	
31а	Цех выпечки	25.20	
31б	Коридор	31.1	
32	Венкамера	210.4	
33	Тех.помещение	98.9	
33а	Тех.помещение	78.20	
34	Тех.помещение	299.70	
35	Лестничная клетка	16.60	
35а	Лоджия	4.5	
36	Лестничная клетка	27.1	
37	Тех.помещение	55.1	
38	Коридор	19.4	
39	Тех.помещение	14.8	
40	Лифтовой холл	31.20	
42	Тех.помещение	98.7	
43	Лестничная клетка	19.56	
44	Лестничная клетка	19.51	
45	Тех.помещение	112.4	
45а	Кроссовая	19.90	

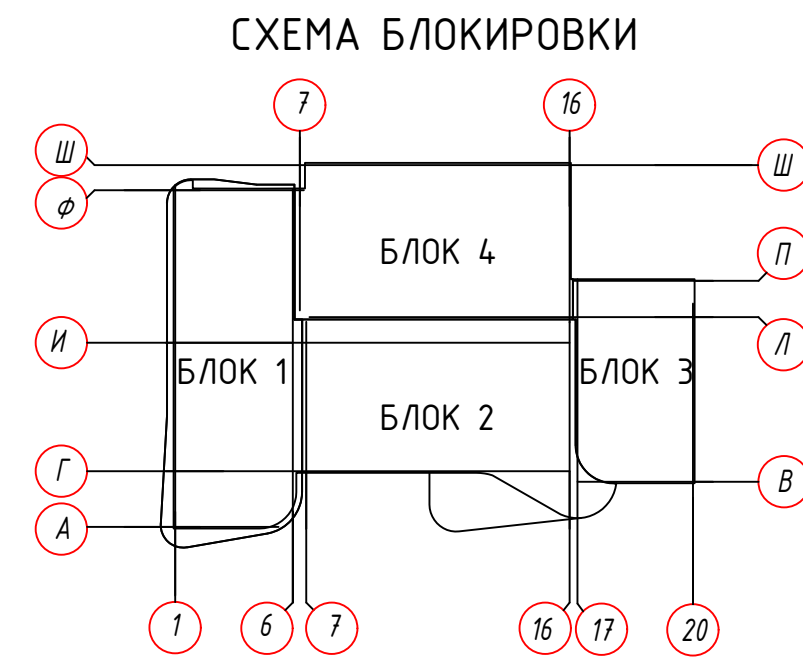

Изм.				Итого			
№	Кол.	Изм.	Лист	Подпись	Дата	Лист	Листов
1	1	1	1	Галицкий С. В.	02.26	1	1
2	1	1	1	Галицкий С. В.	02.26	1	1
3	1	1	1	Галицкий С. В.	02.26	1	1

Физкультурно-оздоровительный комплекс с гостиницей город Астана, район Есиль, ул. Хусейн-бен-Талас, зд. №25


Физкультурно-оздоровительный комплекс (Блоки 1, 2, 3, 4)

Оптический план

поставлено на опт. -4,050


100 "citylight group"

План 2 этажа

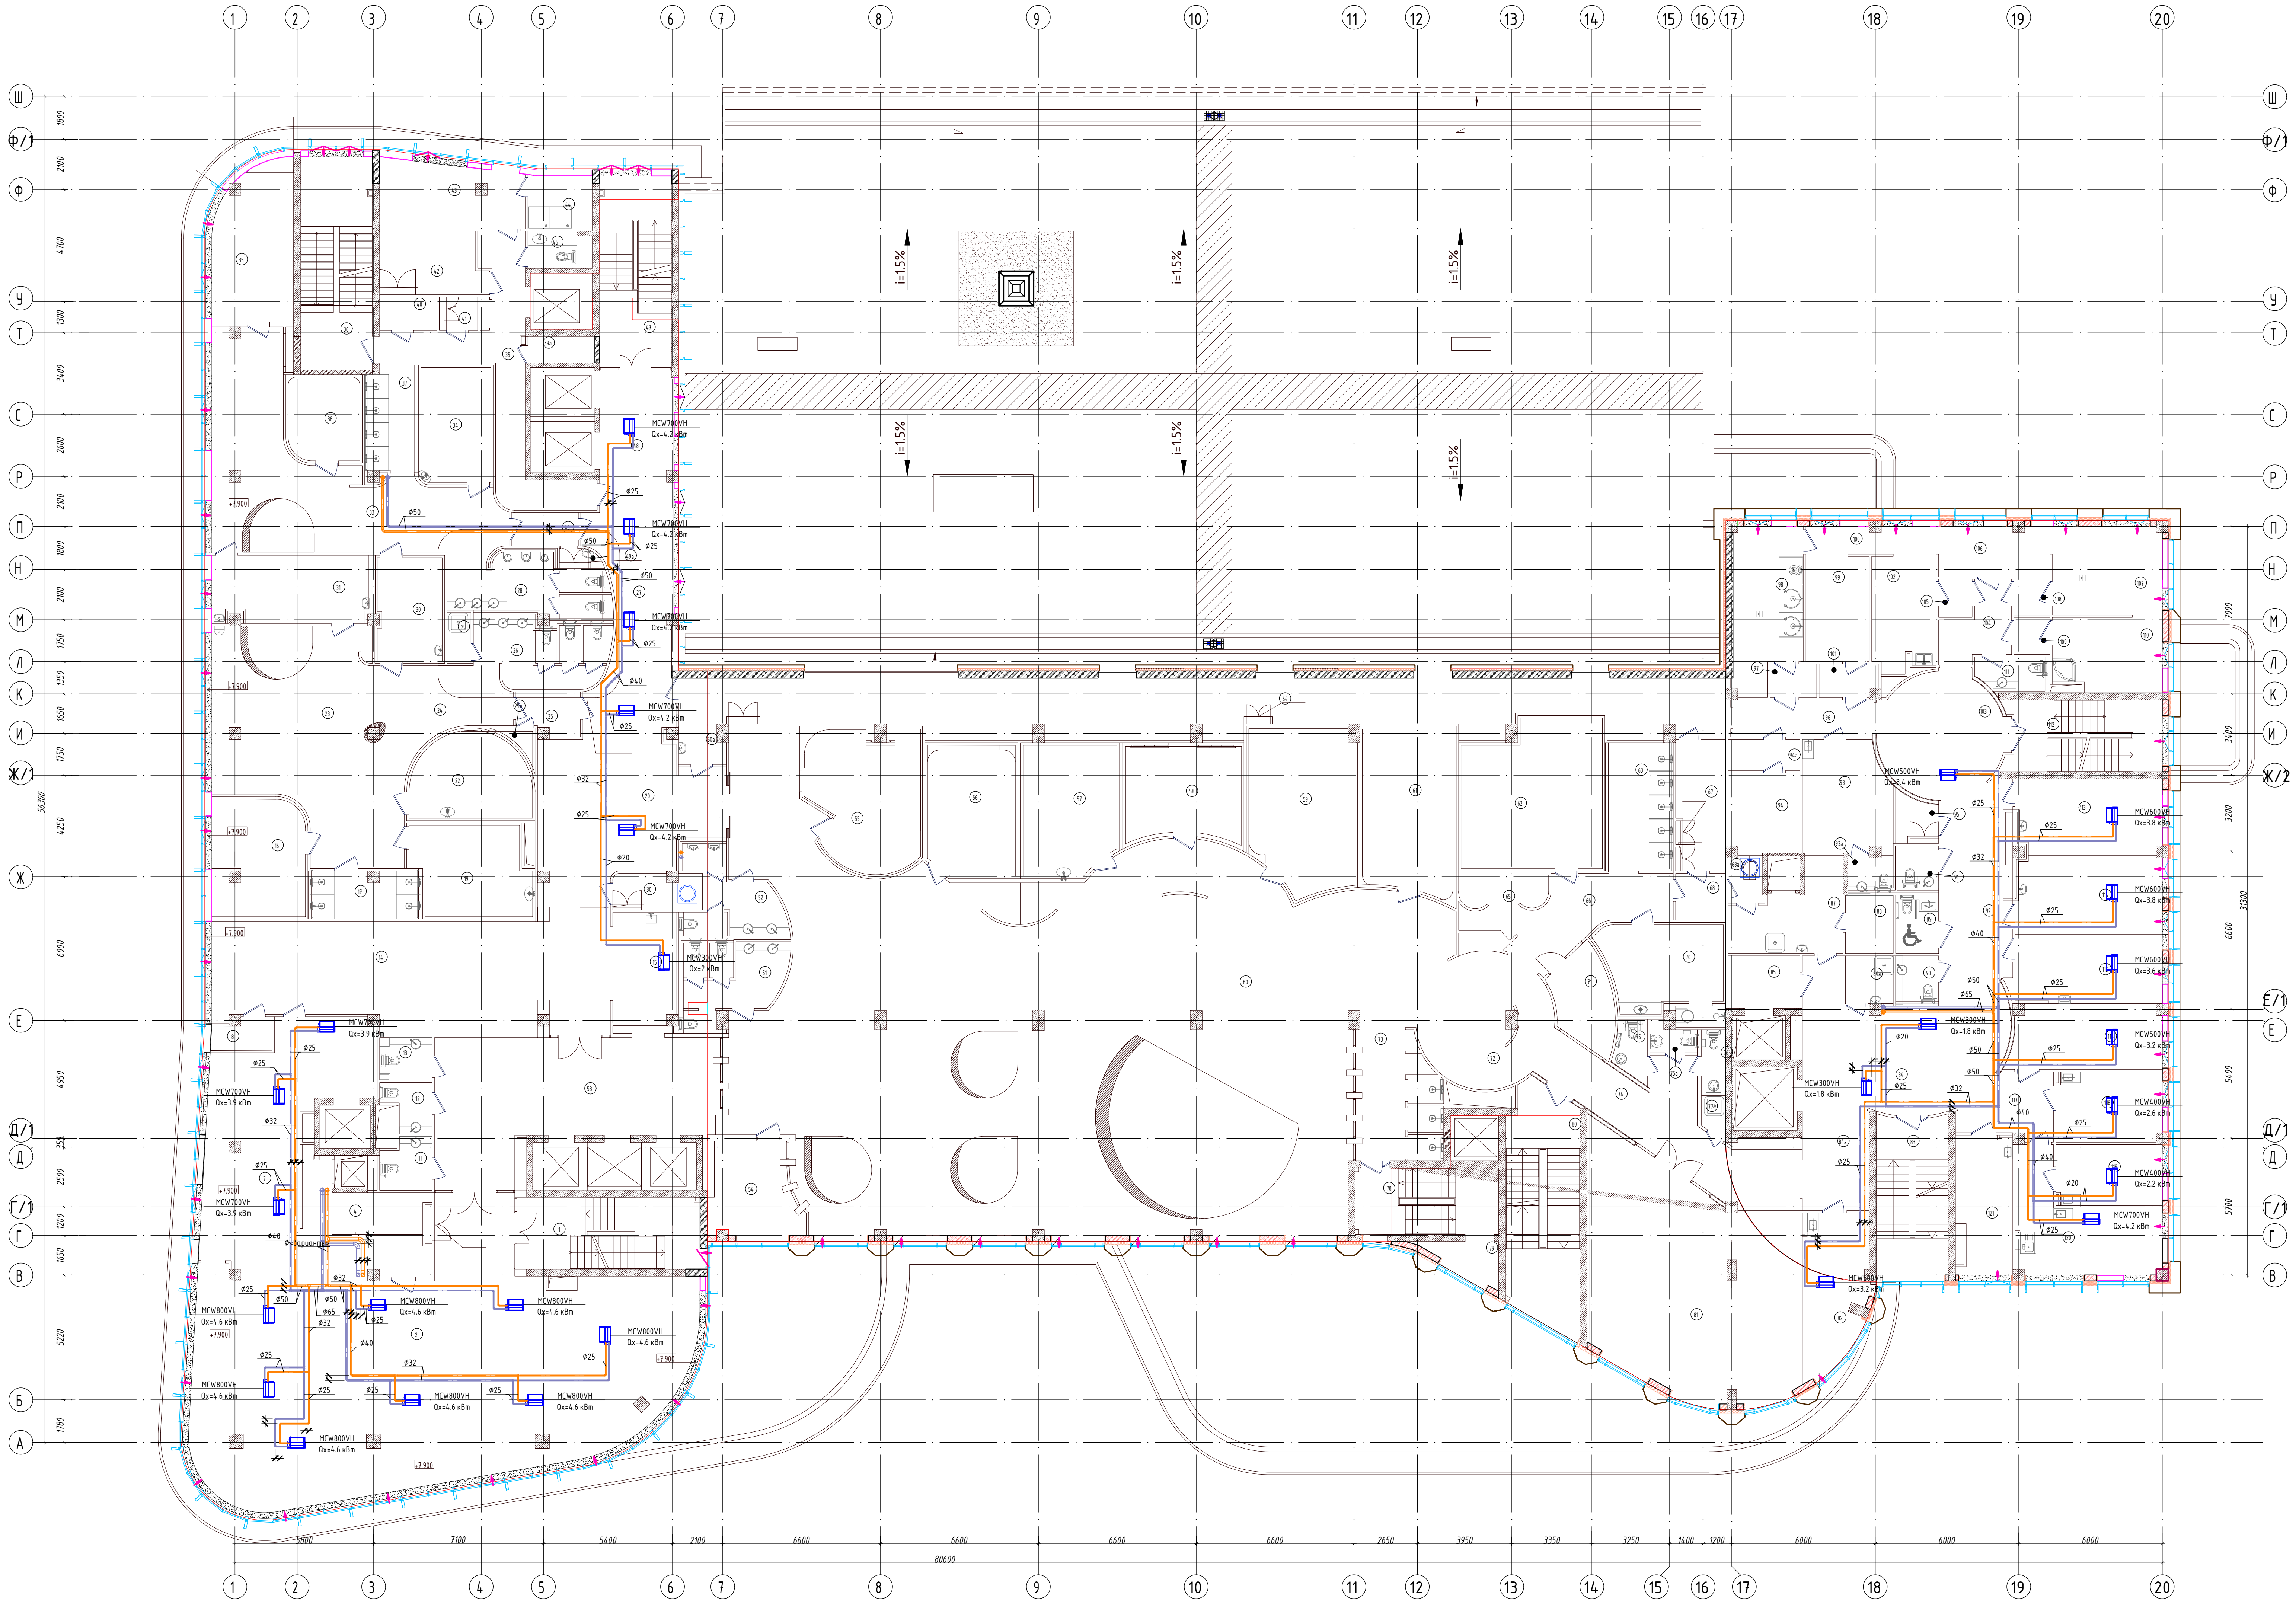


Экспликация помещений (начало)				Экспликация помещений (окончание)			
Поз	Наименование	площадь	Кат. помеще-ния	Поз	Наименование	Площадь	Кат. помеще-ния
1	Лестничная клетка	22.5		83	Лестница	19.4	
2	Ресторан	183.25		84	Холл	11.81	
4	Цех преобразительн. Очистки и сортировки посуды	10.32		84а	Коридор	6.39	
7	Догоготовочная-сервировочная бара	57.93		85	Лифтовой холл	4.7	
8	Комната для курения	2.94		87	К/М	4.132	
11	Санузел	4.3		88	Холод. Камеры временного хранения отходов	4.7	
12	Санузел	3.49		89	Санузел ММГН	4.22	
13	Санузел	3.76		89а	К/М	13.42	
14	Зона фито бара	59.96		90	Санузел	3.12	
15	Фито бар	12.35		91	Санузел	2.8	
16	Русская баня	18.4		92	Коридор	22.3	
17	Душевая	8.44		93	Процедурный кабинет гидрокалопроктолога с гигиеническим душем	16.44	
19	Персон. Хаман-пиллжабачная	17.26		93а	Санузел	2.42	
20	Ресепшен	55.21		94	Тех помещение	9.68	
22	Хаман	16.14		94а	К/М	3.73	
23	Женское отделение	63.37		95	Кладовая хранения чистого белья	2.81	
24	Коридор	14.66		96	Коридор	9.32	
25	Коридор	3.65		97	Раздевальня посетителей	3.19	
25а	К/М	1.09		98	Душ шарка	18.31	
26	Санузел	13.32		99	Душ виши	11.62	
27	Холл	32.6		100	Коридор	5.87	
28	Санузел	12.7		101	Раздевальня посетителей	3.19	
29	К/М	2		102	Таласотерапия	12.36	
30	Индивидуальное парение	11.61		103	Холл	22.94	
31	Пилинг	9.04		104	Коридор	7.42	
32	Пилинг	8.25		105	Раздевальня посетителей	2.12	
33	Мужское отделение	56.87		106	Помещение обслуживающего персонала	9.67	
34	Персон. Хаман-пиллжабачная	14.03		107	Кабинет гидроассажа	16.8	
35	Сауна	19.09		108	Раздевальня посетителей	2.13	
36	Лестница	26.26		109	Раздевальня посетителей	2.2	
37	Душевые	9.49		110	Кабинет гидроассажа	13.57	
38	Хаман	10.24		111	Санузел	3.47	
39	Коридор	25.05		112	Лестница	18.82	
39а	Тех. Помещение	2.92		113	Кабинет врача проктолога	18.65	
40	Комната слабых токов	3.21		114	Процедурный кабинет аппаратной терапевтической коррекции (восточная)	18.39	
41	Оборуд. Хаман	1.71		115	Процедурный кабинет косметолога лица и децелле. бодас	17.17	
42	Тех. Помещение	10.45		116	Процедурный кабинет аппаратной терапевтической коррекции (криолиполиз)	16	
44	Душевая	4.37		117	Коридор	9.37	
45	Санузел	3.04		118	Кабинет врачей-косметологов	12.62	
47	Лестница	23.6		119	Процедурный кабинет массажа	10.96	
48	Холл	14.26		120	Процедурный кабинет обертывания/укрепления	20.67	
49	Коридор	3.76		121	Криосауна	12.75	
49а	К/М	0.94					
50	К/М	5.02					
50а	К/М	2.78					
51	Санузел Ж	12.17					
52	Санузел М	10.15					
53	Холл	55.18					
54	Баня травяная	13.03					
55	Баня кокос	25.68					
56	Баня арома-фруктовая	19.73					
57	Хаман	20.56					
58	Баня каменная	18.2					
59	Баня русская можжевеловая	28.35					
60	Зал	410.35					
61	Баня финская	25.58					
62	Баня общая	34.43					
63	Душ	14.23					
64	Коридор	92.33					
65	Душ	7.51					
66	Коридор	15.45					
67	Тех. Помещение бани	10.59					
68	Тандыр	3.94					
68а	Помещение бельепровода	2.73					
70	Индивиду парение (2 стола)	18.51					
71	Снежная комната	8.86					
72	Холл	27.48					
73	Душевые	15.98					
74	Коридор	29.93					
75	Санузел	2.98					
75а	Санузел	2.02					
76	Санузел	2.55					
77	К/М	1.53					
78	Лестница	16.25					
79	Тандыр	3.61					
80	Лестница	28.83					
81	Сонная комната + Тепидариум	76.28					
82	Кабинет фитюра и прессо терапии	15.39					

СХЕМА БЛОКИРОВКИ

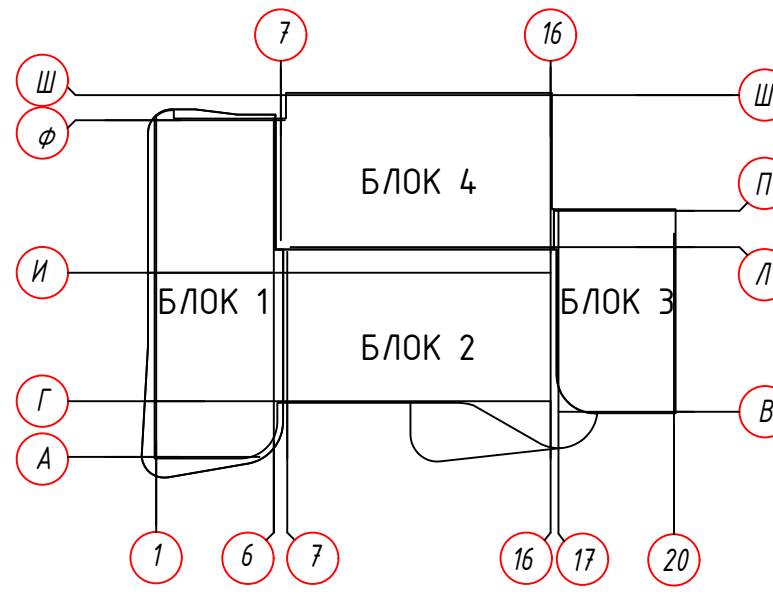


Изм.				Подпись				Дата			
Изм.	Кол.	И. Дем.	Лист	Изм.	Кол.	И. Дем.	Лист	Изм.	Кол.	И. Дем.	Лист
Гип	Гальперин	С.	02.26	Гип	Гальперин	С.	02.26	Гип	Гальперин	С.	02.26
Проект	Проект	Проект	02.26	Проект	Проект	Проект	02.26	Проект	Проект	Проект	02.26
Физкультурно-оздоровительный комплекс с гостиницей гор. Астана, район Есиль, ул. Хусейн Ван Талая, зб. №25				Физкультурно-оздоровительный комплекс (Блоки 1, 2, 3, 4)				Однотипный план			
Получено на опр. -4,050				РП				100 "Vitality Group"			

План 3 этажа

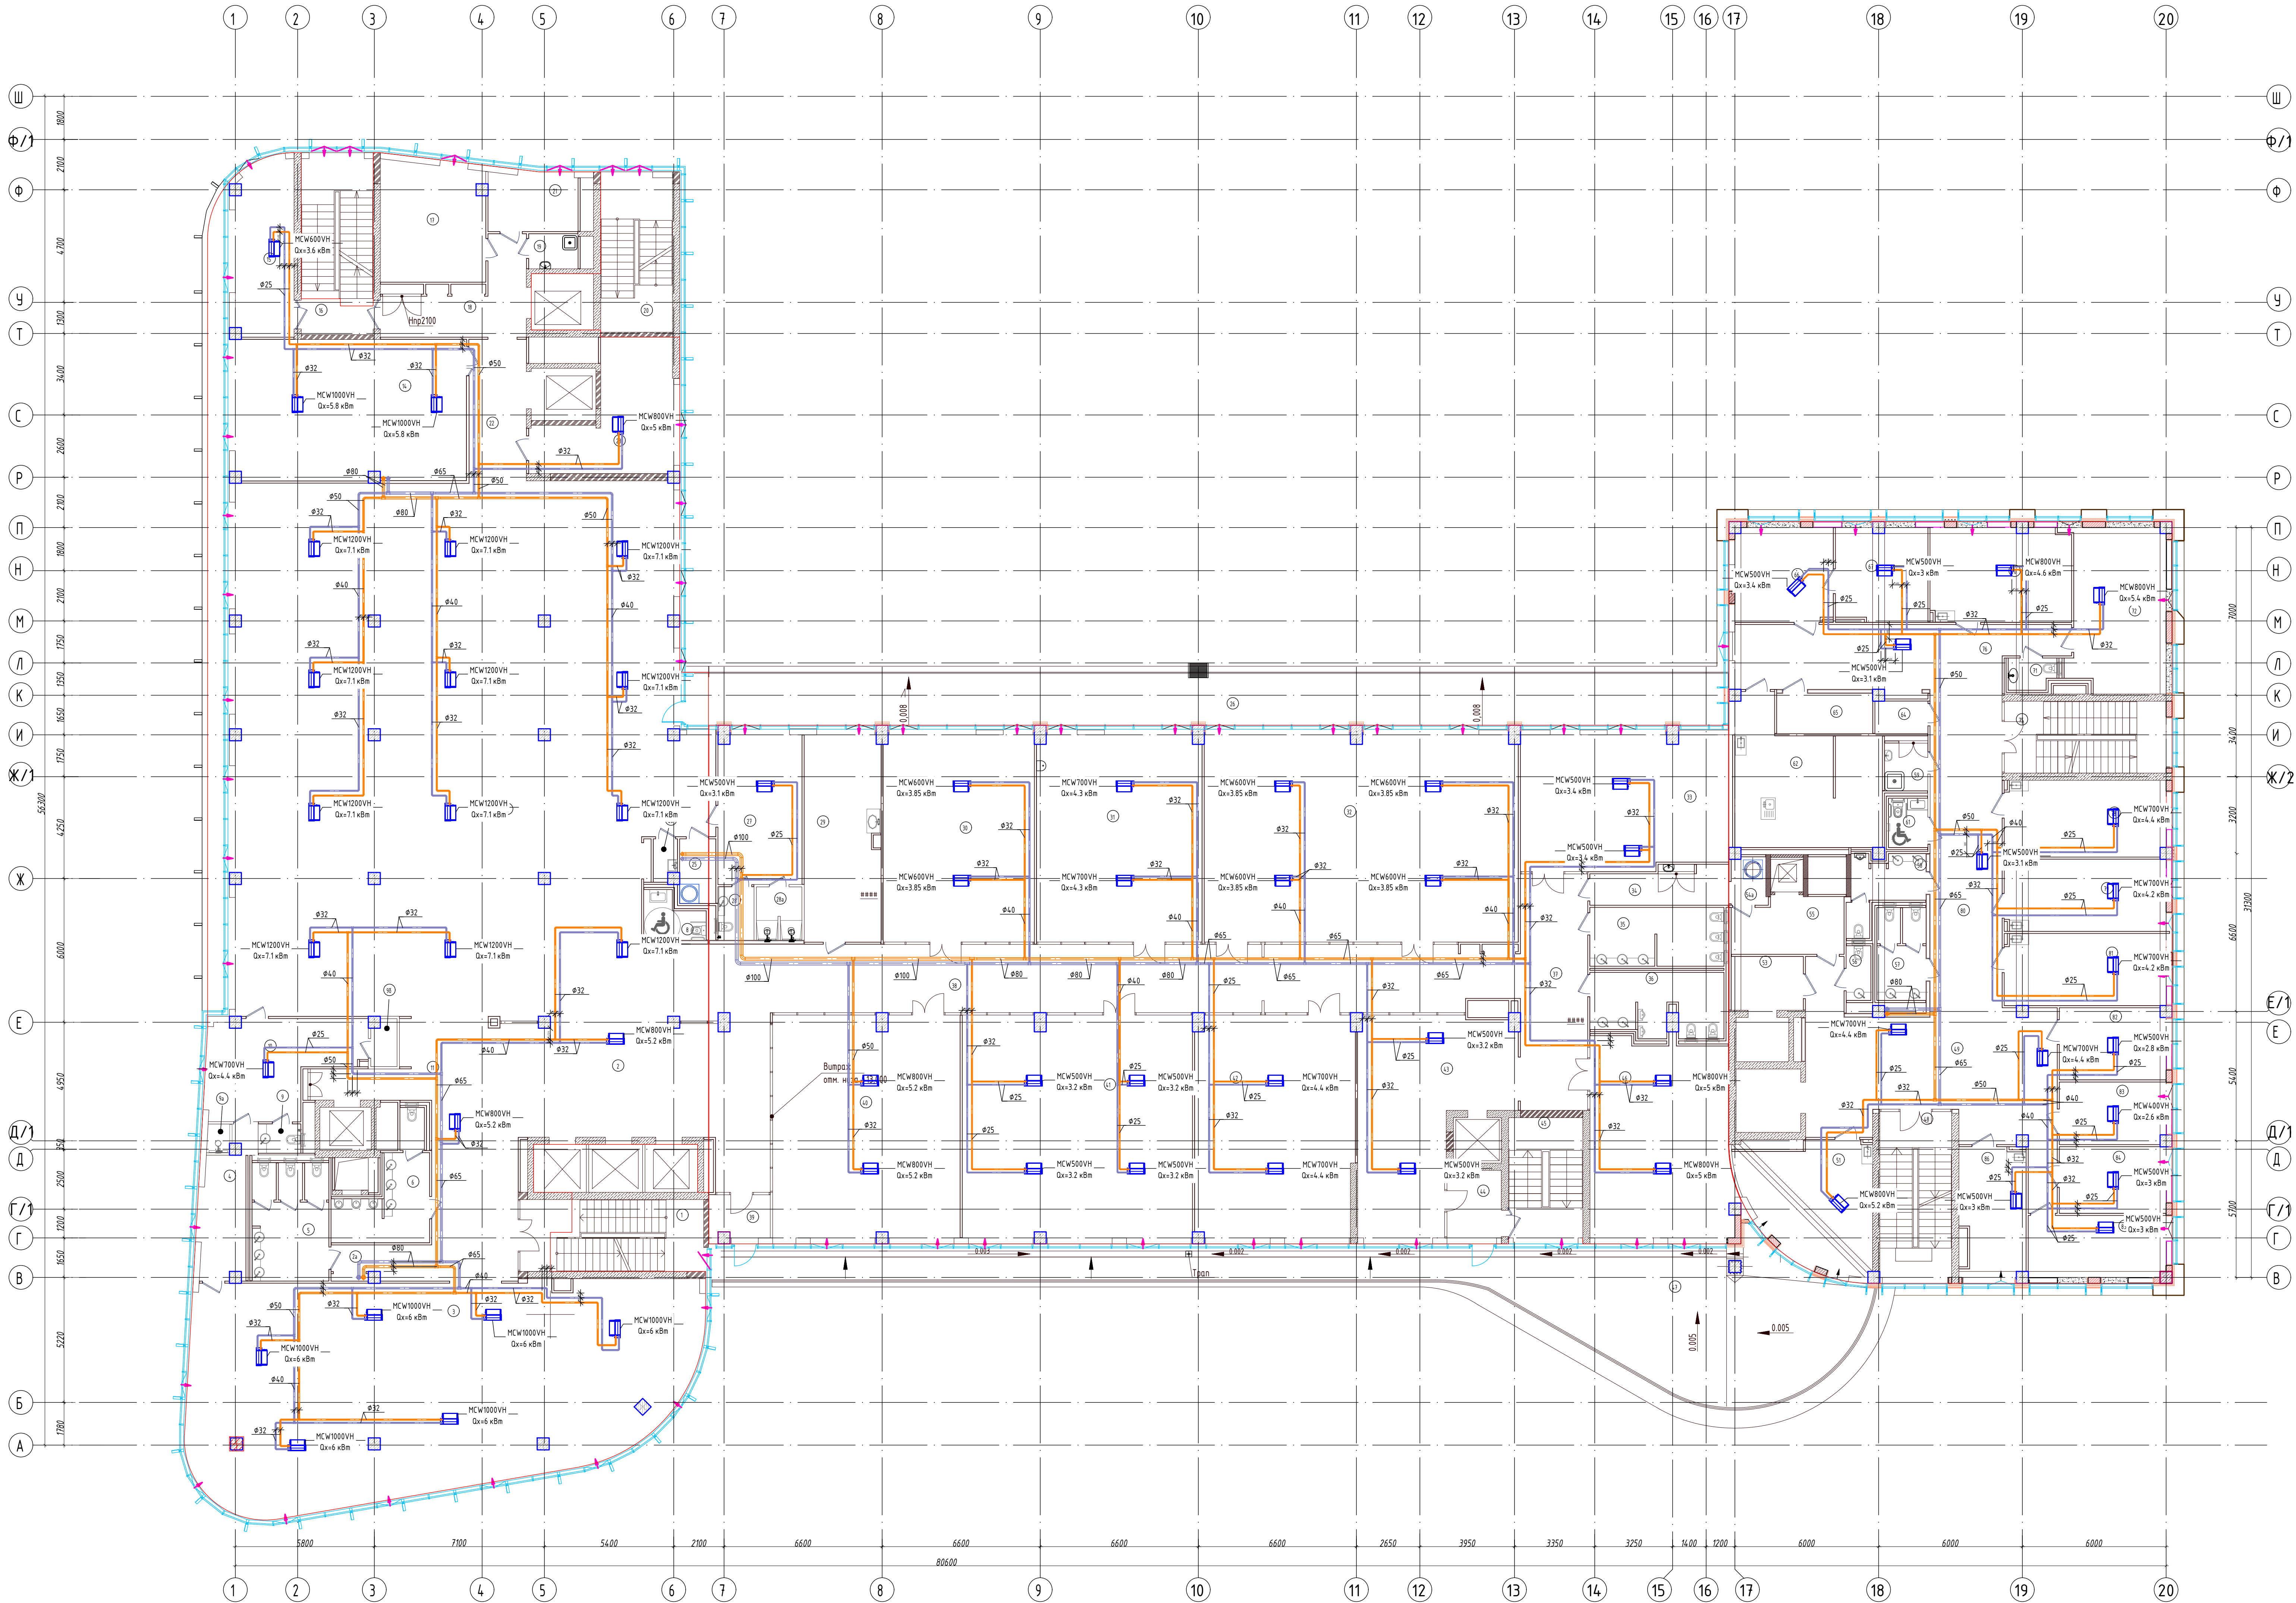

Экспликация помещений			
Поз	Наименование	площадь	Кол. помеще-ния
1	Лестничная клетка	23.1	
2	Холл	68.6	
2а	Коридор	27.1	
3	Зона кардио тренажеров	179.6	
4	Зал персонального стрелка	9.80	
5	Санузел Ж	14.92	
6	Санузел М	12.61	
8	Санузел	4.2	
9	Санузел	2.2	
9а	Душевая	2.2	
9б	Душевая	2.0	
10	Тренировочная М	22.1	
11	Фитобар	13.4	
12	Тренировочный зал	426.4	
14	Скайл студия	57.9	
15	Кабинет менеджера	17.7	
16	Лестница	22.8	
17	Тех.помещение	21.6	
18	Коридор	16.6	
19	К/У	3.00	
20	Лестница	19.9	
21	Иниенарная	9.4	
22	Коридор	14.1	
23	Кабинет персонального триннга	24.3	
25	Тех.помещение	4.0	
26	К/У	1.6	
26а	Лобжия	91.8	
27	Тренировочная Ж	22.2	
28	Санузел	3.3	
28а	Душевые	4.1	
29	Кабинет медсестры	28.2	
30	Студия пилатес Индивиду. Занятия пилатес	55.5	
31	Студия боевых искусств	60.7	
32	Взрослая и детская студия групповых и парциальных занятий	115.4	
33	Детский клуб	49.0	
34	Коридор	8.7	
35	Санузел	13.5	
36	Санузел	13.52	
37	Коридор	56.6	
38	Коридор	72.8	
39	Тамбур	4.8	
40	Студия Body & Mind, Аэробик, Аэройоги	73.8	
41	Взрослая студия групповых и танцев, занятий	90.8	
42	Детская спортивно-шаровая студия	62.5	
43	Ресепшен	45.26	
44	Тамбур	6.55	
45	Лестница	16.2	
46	Детская студия функциональной тренировки	49.2	
47	Лобжия	117.1	
48	Лестница	21.4	
49	Холл	57.3	
51	Кабинет УЗИ	25.8	
53	Лифтовой холл	6.70	
54а	Бельепоход	2.75	
55	Холод. Камеры временного хранения отходов	10.7	
56	Санузел	2.3	
57	Санузел	7.7	
58	Санузел	7.2	
59	К/У	3.42	
61	Санузел ММГН	3.3	
62	Лаборатория - заборы крови и материала	21.3	
64	Коридорная	3.0	
65	Кабинет хранения чистого белья	6.7	
66	Кабинет врача дерматолога-венеролога	16.3	
67	Процедурный кабинет дерматолога-венеролога	14.8	
70	Кабинет врача гинеколога	22.9	
71	Санузел посетителей	2.5	
72	Процедурный кабинет гинеколога	26.6	
75	Лестница	20.2	
76	Коридор	35.2	
78	Кабинет врача онколога	21.4	
79	Кабинет врача эндокринолога	20.3	
80	Коридор	40.8	
81	Кабинет врача кардиолога	20.5	
82	Кабинет Главного врача	13.50	
83	Кабинет Зам.гл.врача	11.70	
84	Кабинет бухгалтерии	12.6	
85	Перезаборная	15.0	
86	Кабинет врача диетолога-нутрициониста	14.8	

СХЕМА БЛОКИРОВКИ

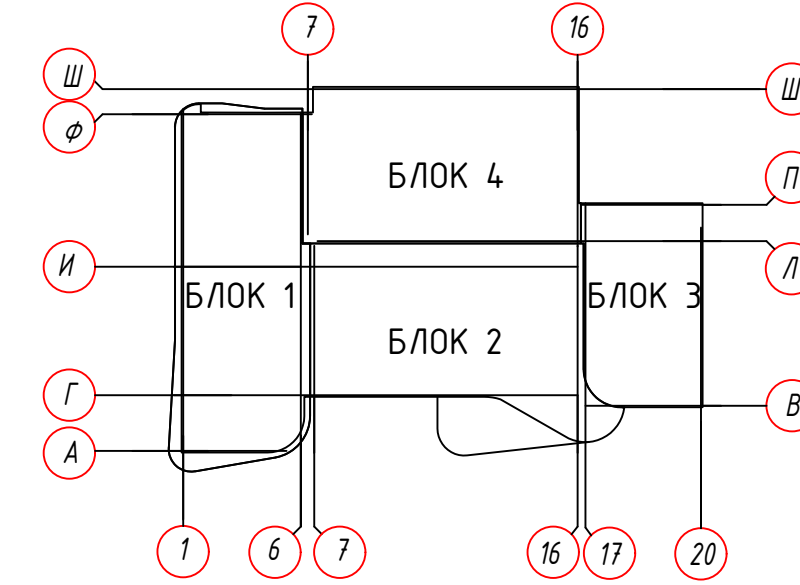


				-ХС			
				Физкультурно-оздоровительный комплекс с гостиницей город Астана, район Есиль, ул. Хусейн Бен Талая, эд. №25			
Изм.	Кол.	И.Дан.	Лист	Подпись	Дата	Специальность	Лист
ГМП	Галижанов	С.	02.26		02.26	Физкультурно-оздоровительный комплекс (блоки 1, 2, 3, 4)	РП
Проверил			02.26		02.26		
				Одобрено: план			
				подана на опр. -4,050			
				100 "unitary group"			

План 4 этажа




Экспликация помещений				Экспликация помещений			
Поз	Наименование	площадь	Кат. помеще-ния	Поз	Наименование	площадь	Кат. помеще-ния
Блок 1				Блок 3			
1	Лестничная клетка	218		60	Лестничная клетка	218	
2	Ресепшен	42.7		61	Лифтовый холл	44.50	
3	Кабинет	19.0		№1	Номер 1		
4	Кабинет	15.7			В том числе		
5	Переговорная	35.9		62	Холл	5.60	
6	Кабинет ген.директора	58.9		63	Спальня	13.5	
7	Помещение	2.2		64	Санузел	5.8	
8	Комната отдыха	18.7		65	Лифтовый холл	13.3	
9	Миникухня	5.2		66	Тех.помещение	5.8	
10	Санузел	2.5		67	Кухня	4.2	
11	Холл	61.6		68	Кухня	4.2	
12	Кухня	7.0		69	Помещение персонала	6.4	
13	Сервер ресепшен	2.5		70	Санузел	2.6	
14	Санузел	7.5		71	Санузел	4.5	
15	Каб. маникюра и педикюра	30.6		72	Комнат медсестры	6.7	
16	Санузел	2.5		73	Коридор	42.30	
17	Санузел	2.5		74	Вельевая	2.4	
18	Коридор	13.5		75	Кроссовая	2.5	
19	Барбер	11.9		№2	Номер 2		
20	Парикмахерская	17.4			В том числе		
21	Парикмахерская	15.2		76	Холл	5.3	
22	Кабинет	17.6		77	Санузел	7.2	
23	Кабинет	14.8		78	Спальня	41.3	
24	Кабинет	17.2		79	Коридор	5.4	
25	Кабинет	16.7		№3	Номер 3		
26	Кабинет Вип косметолога	16.9			В том числе		
27	Коридор	15.6		80	Холл	3.9	
28	Электроощитовая и кроссовая	4.4		81	Санузел	4.7	
29	Персональный мастер	18.6		82	Спальня	25.0	
30	Лестница	22.9		№4	Номер 4		
31	Стерилизационная	10.2			В том числе		
32	Помещение персонала	22.0		83	Холл	5.5	
33	Санузел	3.1		84	Спальня	10.0	
34	Коридор	5.7		85	Санузел	26.7	
34а	Кухня	3.3		86	Лестница	20.8	
35	Лестница	19.9		№5	Номер 5		
36	Холл	31.6			В том числе		
37	Вип маникюр и педикюр	22.1		87	Холл	7.7	
38	Кабинет	15.2		88	Спальня	25.45	
39	Санузел	3.9		89	Санузел	26.8	
40	Парк аппаратов	11.7		90	Массажная	8.8	
40а	Кроссовая	3.6		№6	Номер 6		
41	Коридор	7.0			В том числе		
42	Санузел	3.3		91	Холл	7.1	
43	Коридор	6.8		92	Массажная	6.7	
44	Кабинет	15.3		93	Санузел	7.8	
45	Холл	14.0		94	Спальня	24.0	
46	Коридор	9.1			Номер 7		
47	Кабинет	12.0			В том числе		
48	Кабинет	14.6		95	Холл	10.7	
49	Кабинет	13.6		96	Санузел	6.8	
50	Коридор	14.2		97	Массажная	8.9	
50а	Коридор	23.3		98	Спальня	27.6	
51	Склад вельевая	6.1				462.28	
52	Каб. маникюра и педикюра	14.6					
53	Кабинет	18.5					
54	Кухня	6.4					
55	Ресепшен	40.9					
56	Кабинет директора салона	17.4					
57	Визажист	13.2					
57а	Укладка сушка	13.3					

СХЕМА БЛОКИРОВКИ

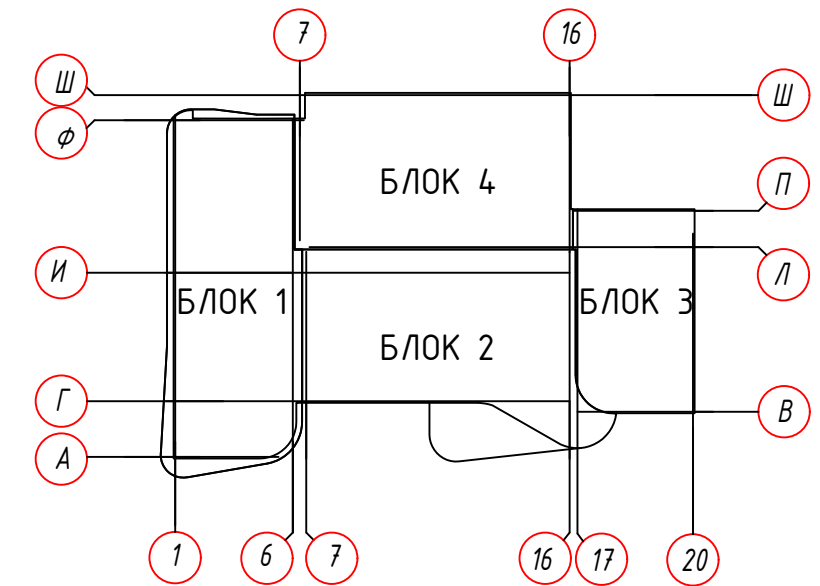


				-ХС			
				Физкультурно-оздоровительный комплекс с гостиницей город Астана, район Есиль, ул. Хусейн Ван Талая, зд. №25			
Изм.	Кол.	И.Дан.	Лист	Подпись	Дата	Специальность	Лист
ГМП	Галимжанов	С.	02.26		02.26	Физкультурно-оздоровительный комплекс (Блоки 1, 2, 3, 4)	Листов
Пробирка							
Разработчик							
				Одобренный план			
				подпись на оп. -4,050			
				100 "Vitality Group"			

План 5 этажа

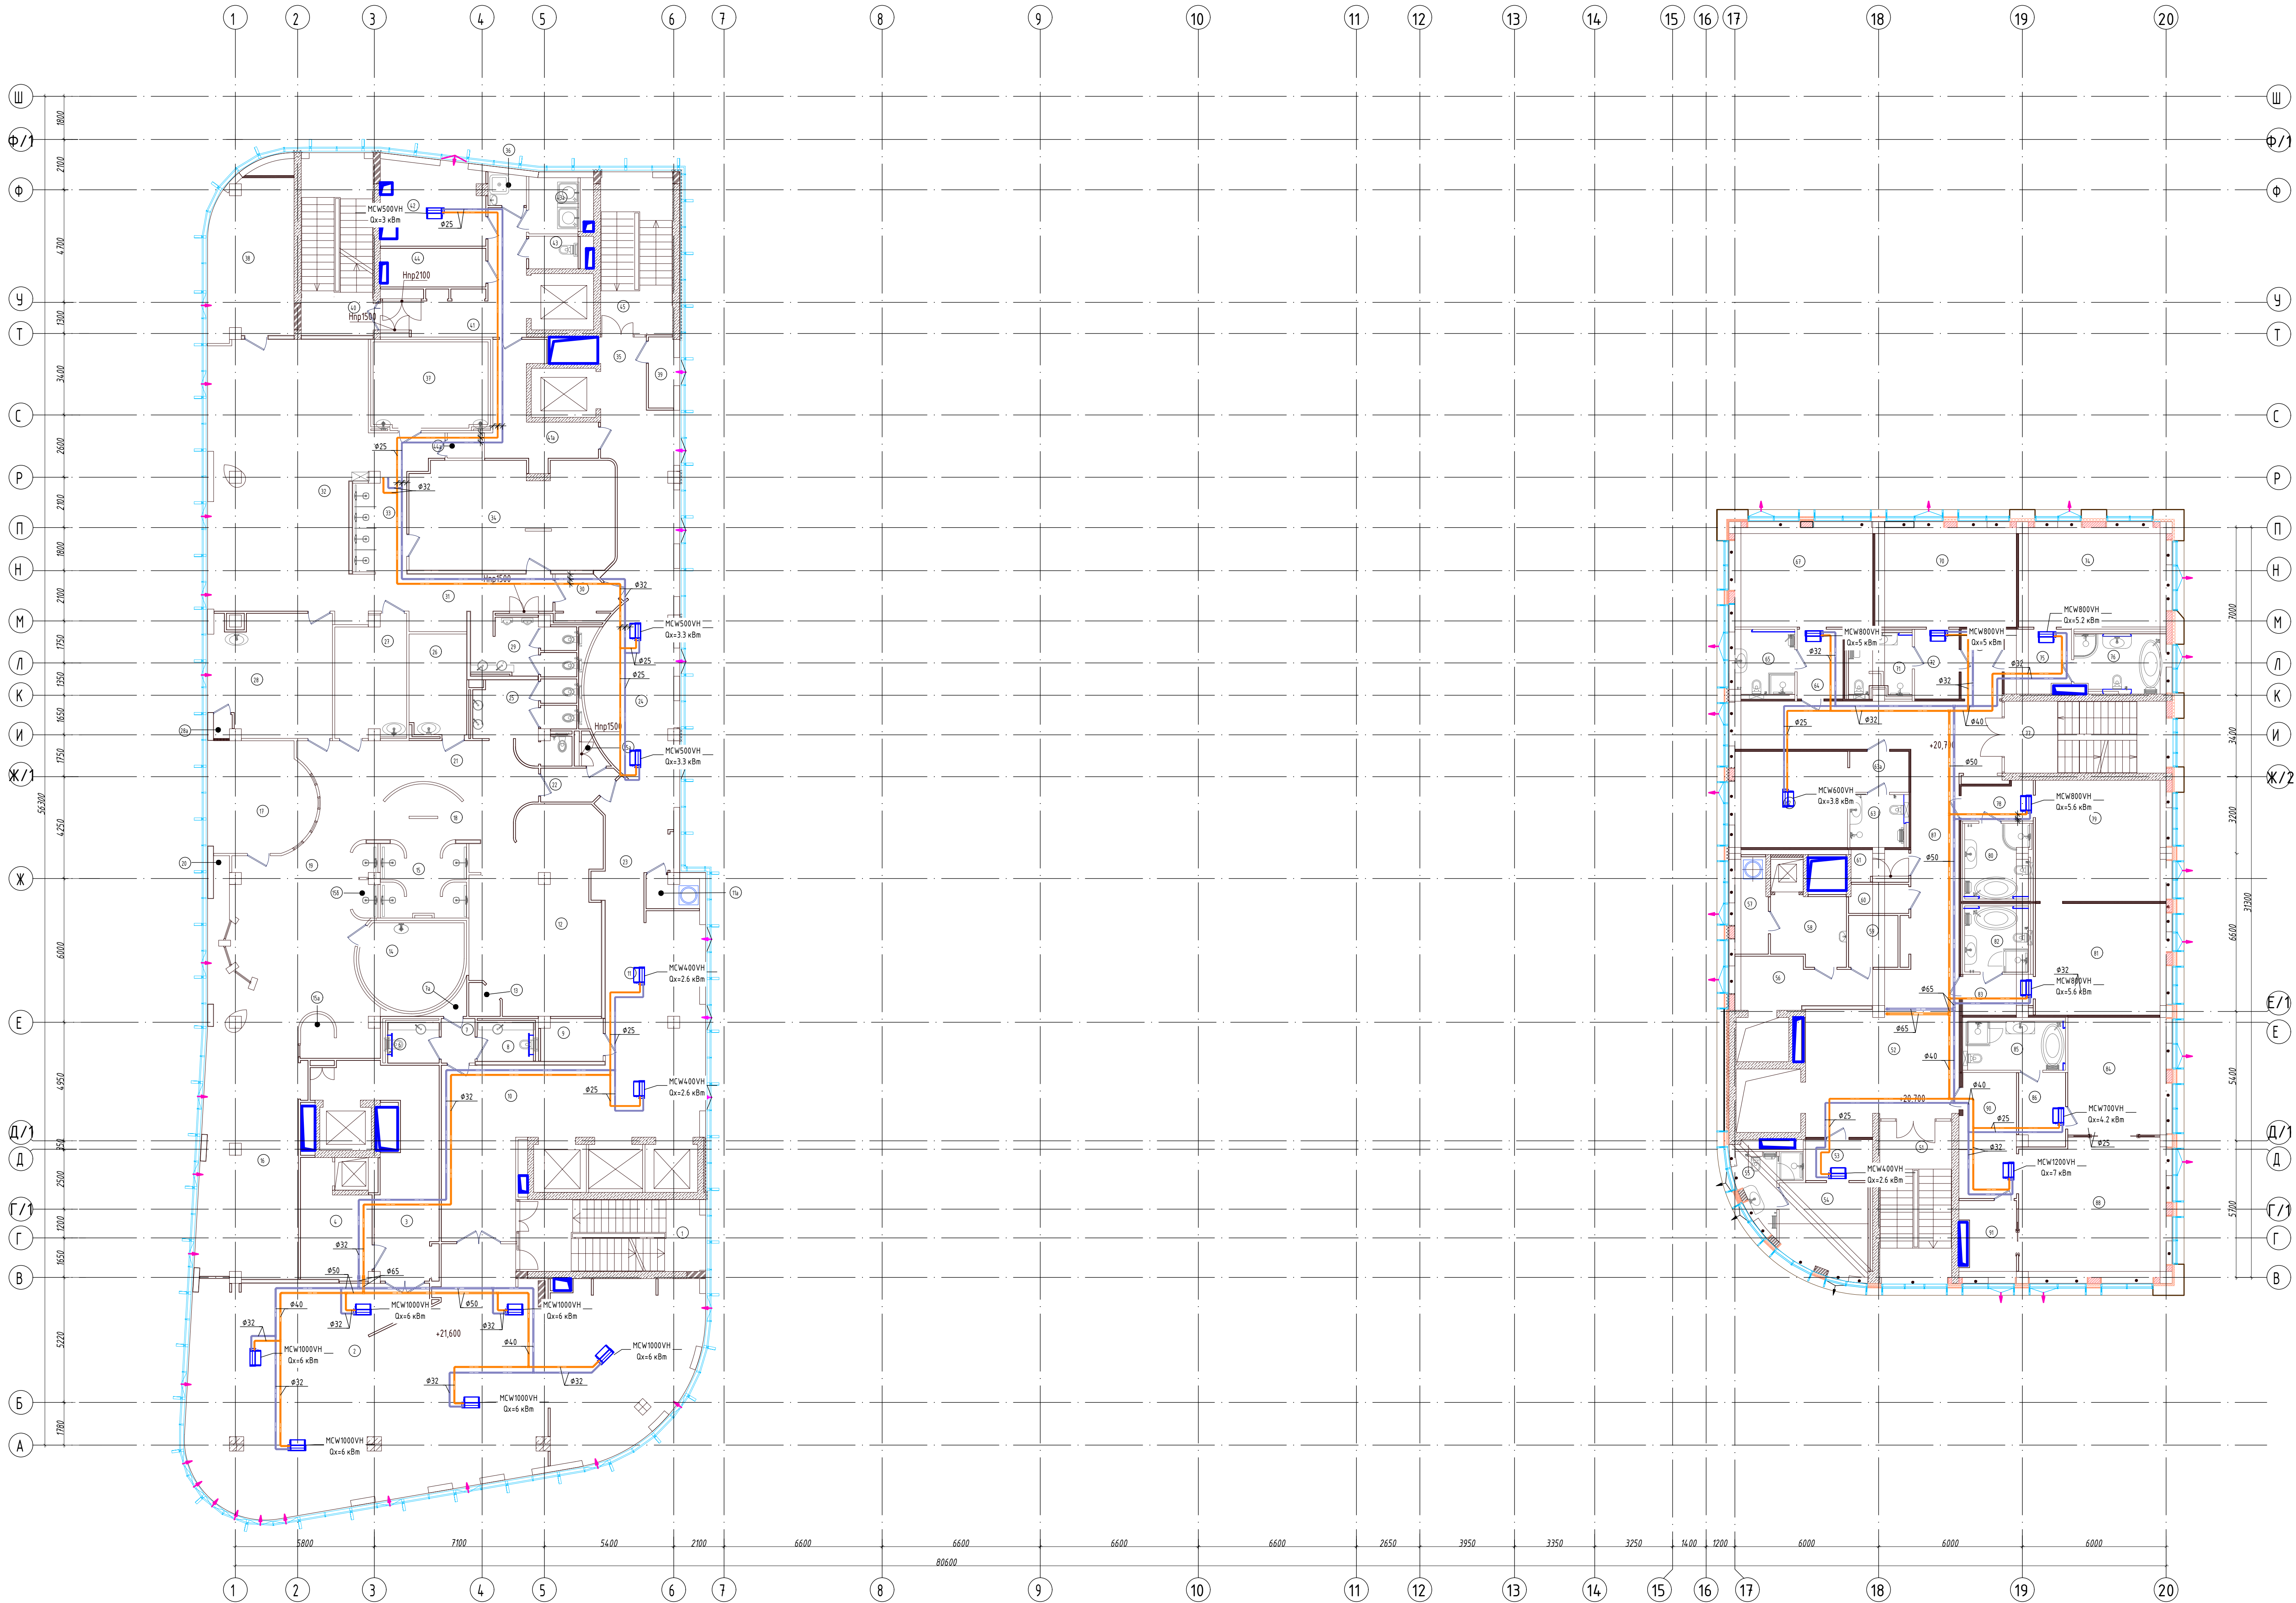



Экспликация помещений (начало)				Экспликация помещений (окончание)			
Поз	Наименование	площадь	Кат. помеще-ния	Поз	Наименование	площадь	Кат. помеще-ния
1	Лестничная клетка ЛМ-3.1	23.2		51	Лестница ЛМ-1.3	19.60	
2	Помещение	180.0		52	Холл	31.5	
3	Раздаточная	25.4			Номер 1		
4	Очистка, сортировка посуды	12.60			в том числе		
6	Санузел	3.60		53	Холл	5.4	
7	Тамбур	2.6		54	Спальня	12.8	
7a	Оборудование ханам	1.0		55	Санузел	5.4	
8	Санузел	3.8		56	Лифтовый холл	16.2	
9	Гардероб	4.5		57	Пособное помещение	5.4	
10	Холл	45.4		58	Пти	8.6	
11	Ресепшен	25.7		59	Кухня	4.4	
11a	Пом. Бельперовода	2.8		60	Кроссовая	2.9	
12	Пом. Бельперовода	43.1		61	Бельевая	3.0	
13	Комната переобувания	1.5			Номер 2		
14	Ханнам	15.30			в том числе		
15	Душевые	10.9		62	Спальня	18.8	
15a	Душевые	2.4		63	Санузел	5.0	
15b	Душевые	2.9		63a	Холл	4.2	
16	Зона отдыха	85.2			Номер 3		
17	Сауна	19.4			в том числе		
18	Фены	7.0		64	Холл	5.5	
19	Холл	54.0		65	Санузел	6.7	
20	Тех.помещение	1.2		67	Спальня	24.4	
21	Коридор	18.4			Номер 4		
22	Тамбур	3.9			в том числе		
23	Холл	15.6		70	Спальня	24.4	
24	Холл	32.4		71	Санузел	6.5	
25	Санузел	12.1		72	Холл	5.4	
25a	Санузел	1.4		73	Тамбур	4.9	
26	Массажная	10.0			Номер 5		
27	Индивидуальное парение	13.85			в том числе		
28	Массажная	24.63		74	Спальня	25.4	
28a	Тех.помещение	0.35		75	Холл	7.2	
29	Санузел	9.9		76	Санузел	9.1	
30	Тамбур	4.3		77	Лестница ЛМ- 2.3	20.2	
31	Коридор	15.9			Номер 6		
32	Зона отдыха	75.44			в том числе		
33	Душевые	8.30		78	Холл	4.6	
34	Вип раздевалка	37.90		79	Спальня	27.4	
35	Лифтовый холл	21.3		80	Санузел	8.2	
36	К/И	2.1			Номер 7		
37	Ханнам	18.8			в том числе		
38	Сауна	22.6		81	Спальня	25.2	
39	Комната для курения	3.4		82	Санузел	7.4	
40	Лестница ЛМ-2.1	22.8		83	Холл	4.7	
41	Коридор	13.2			Номер 8		
41a	Коридор	12.72			в том числе		
42	Комната персонала	15.0		84	Спальня	20.1	
43	Санузел	2.3		85	Санузел	8.4	
43a	Душевые	4.80		86	Гардероб	5.8	
44	Тех.помещение	7.0		87	Коридор	5.64	
44a	Душ	1.5		88	Гостиная	34.7	
45	Лестница ЛМ-1.1	20.3		90	Холл	12.3	
				91	Кухня	6.8	

СХЕМА БЛОКИРОВКИ

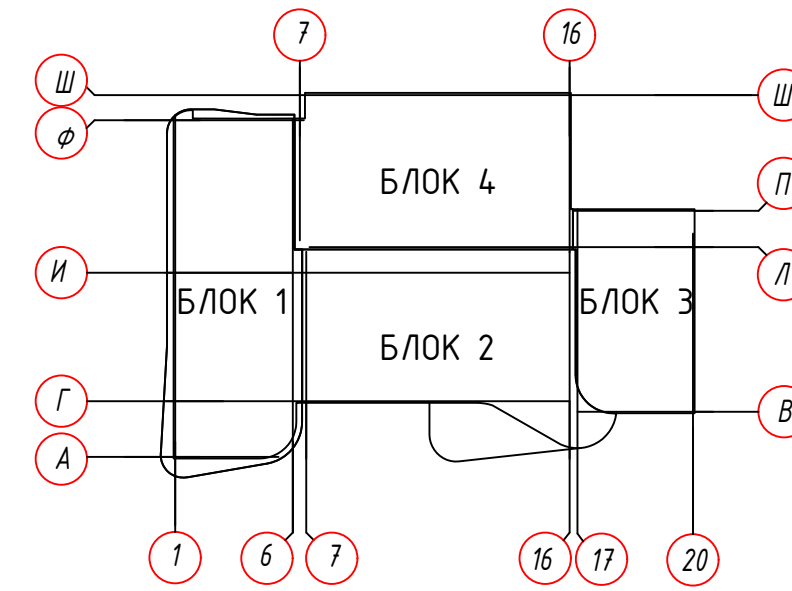

				-ХС			
				Физкультурно-оздоровительный комплекс с гостиницей гор. Астана , район Есиль , ул . Хусейн Бей Талап , зб . №25			
Изм.	Кол.	№ док.	Лист	Подпись	Дата	Специальность	Лист
ГМП	Галимжанов С.	02.26	02.26			Физкультурно-оздоровительный комплекс (блоки 1, 2, 3, 4)	Лист
Проверил		02.26	02.26			РП	*
Разработчик						Одобрено на опр. -4,050	100 "citycity Group"

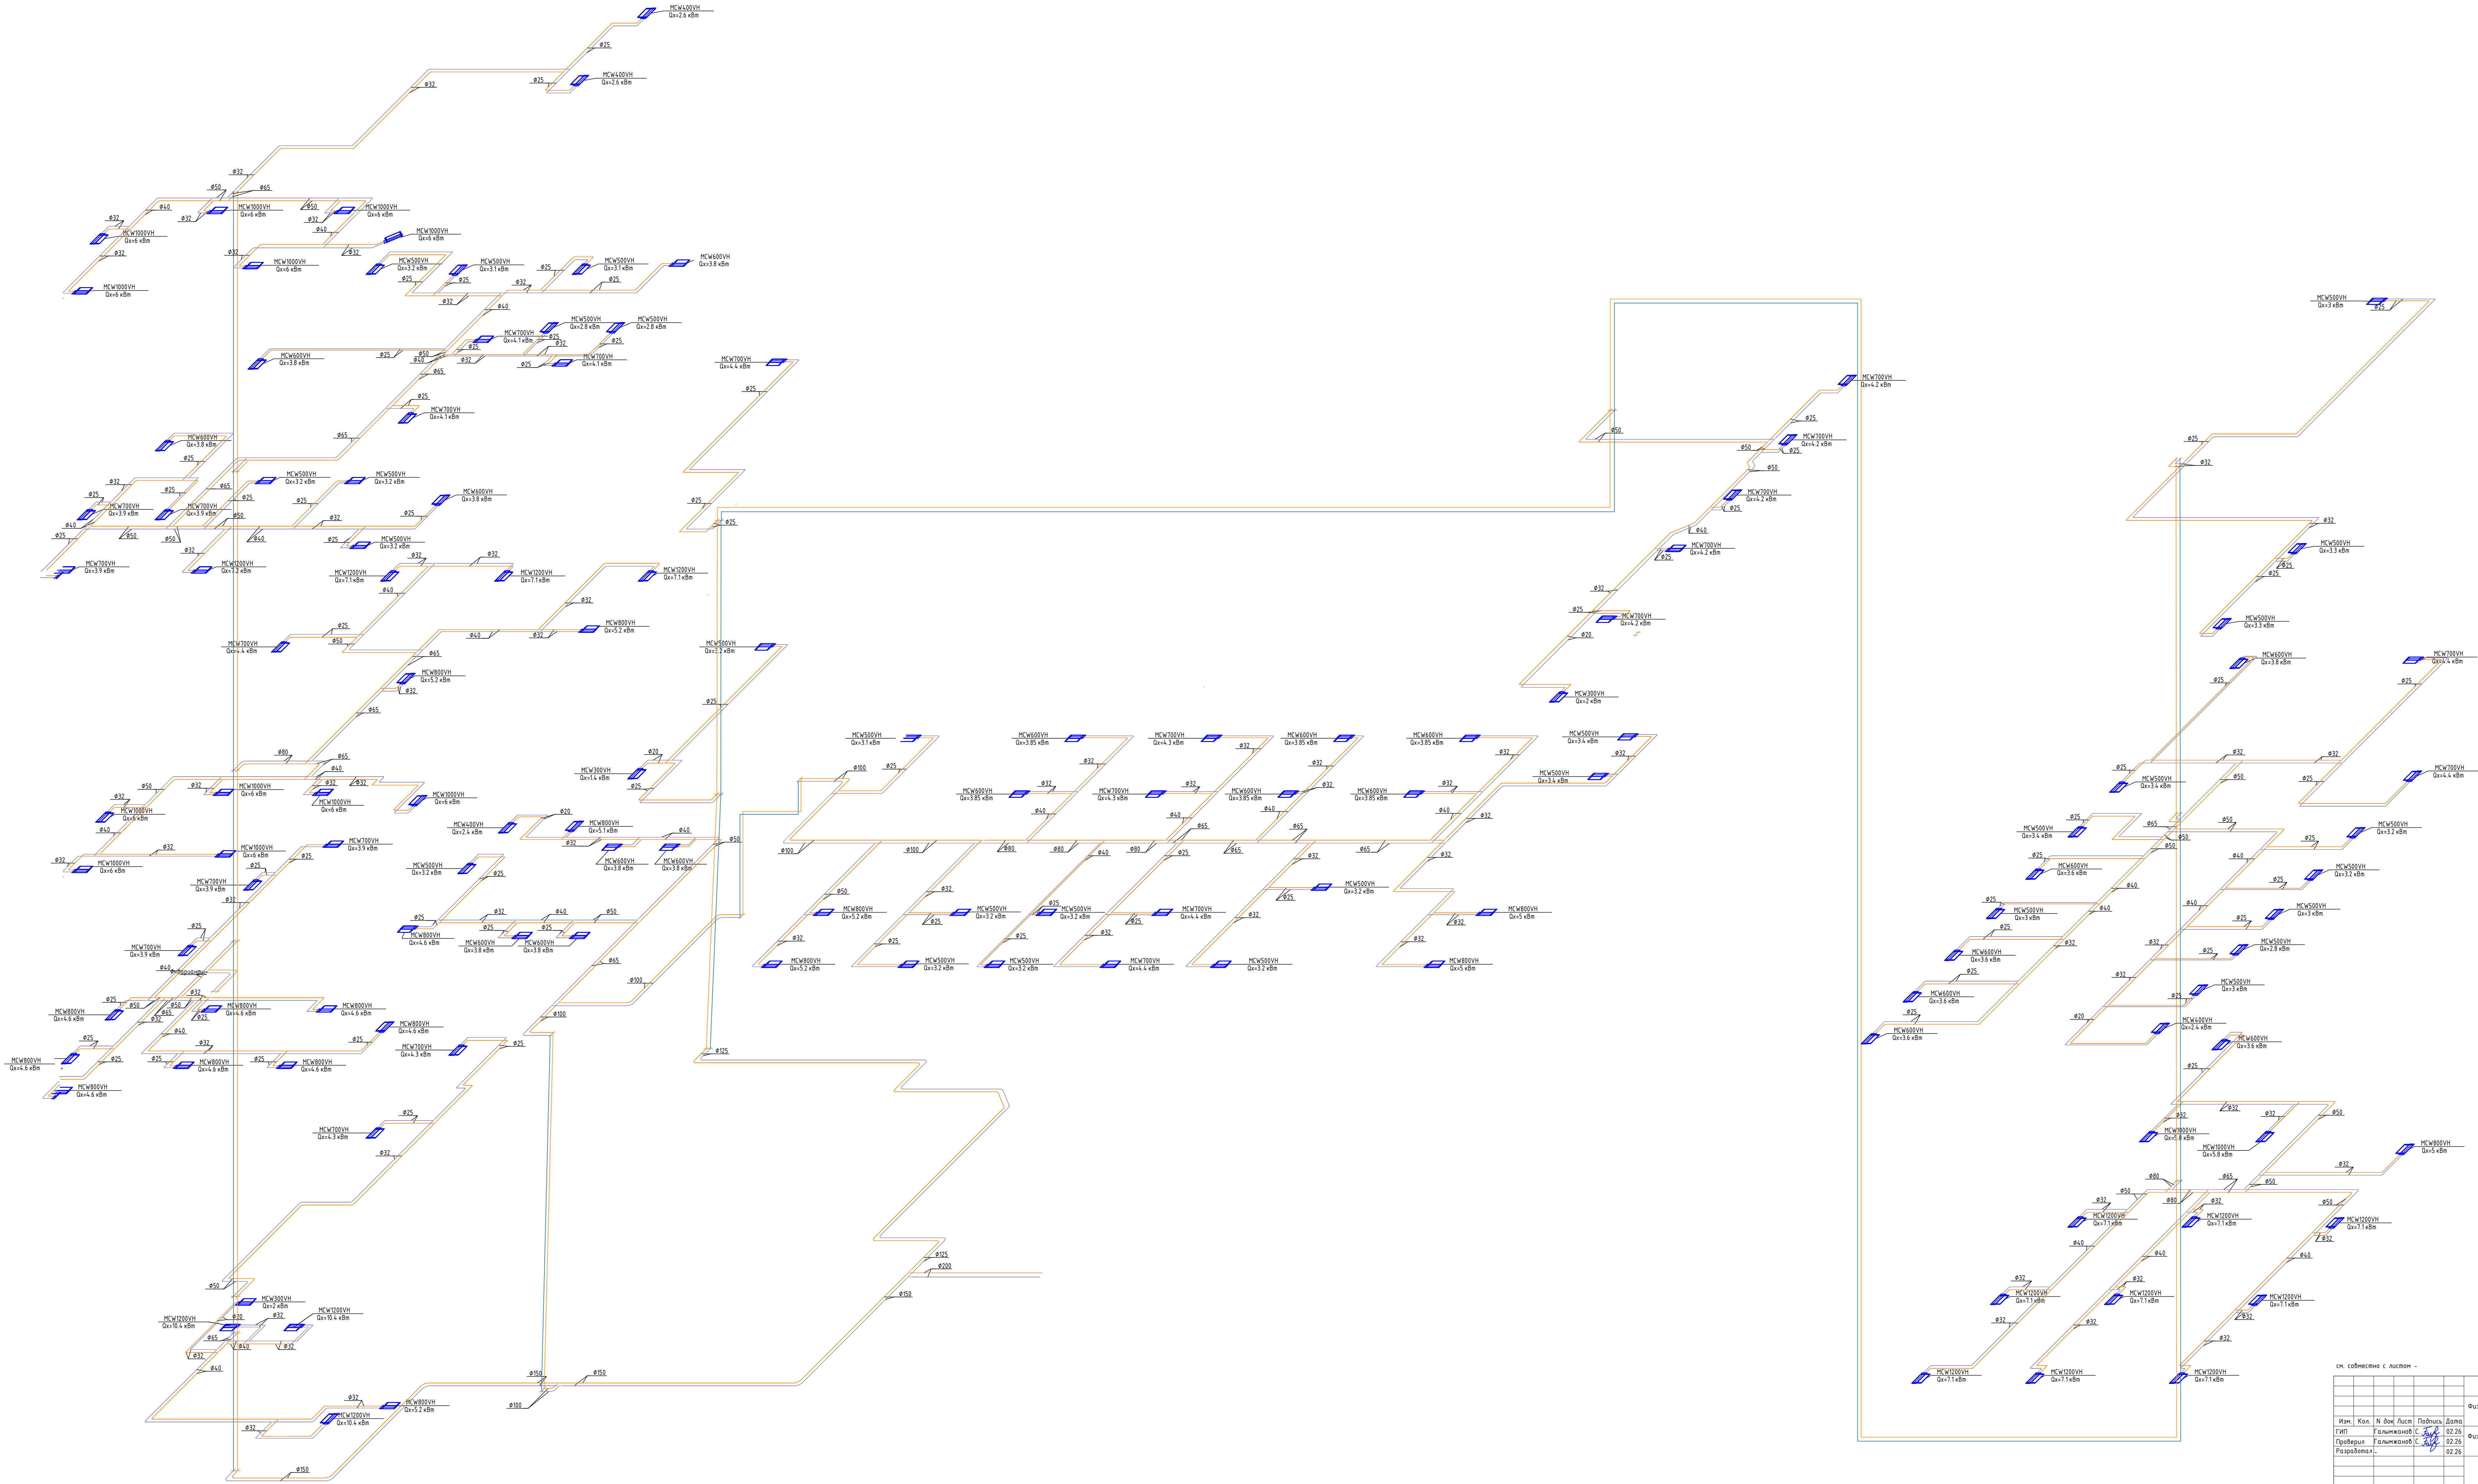

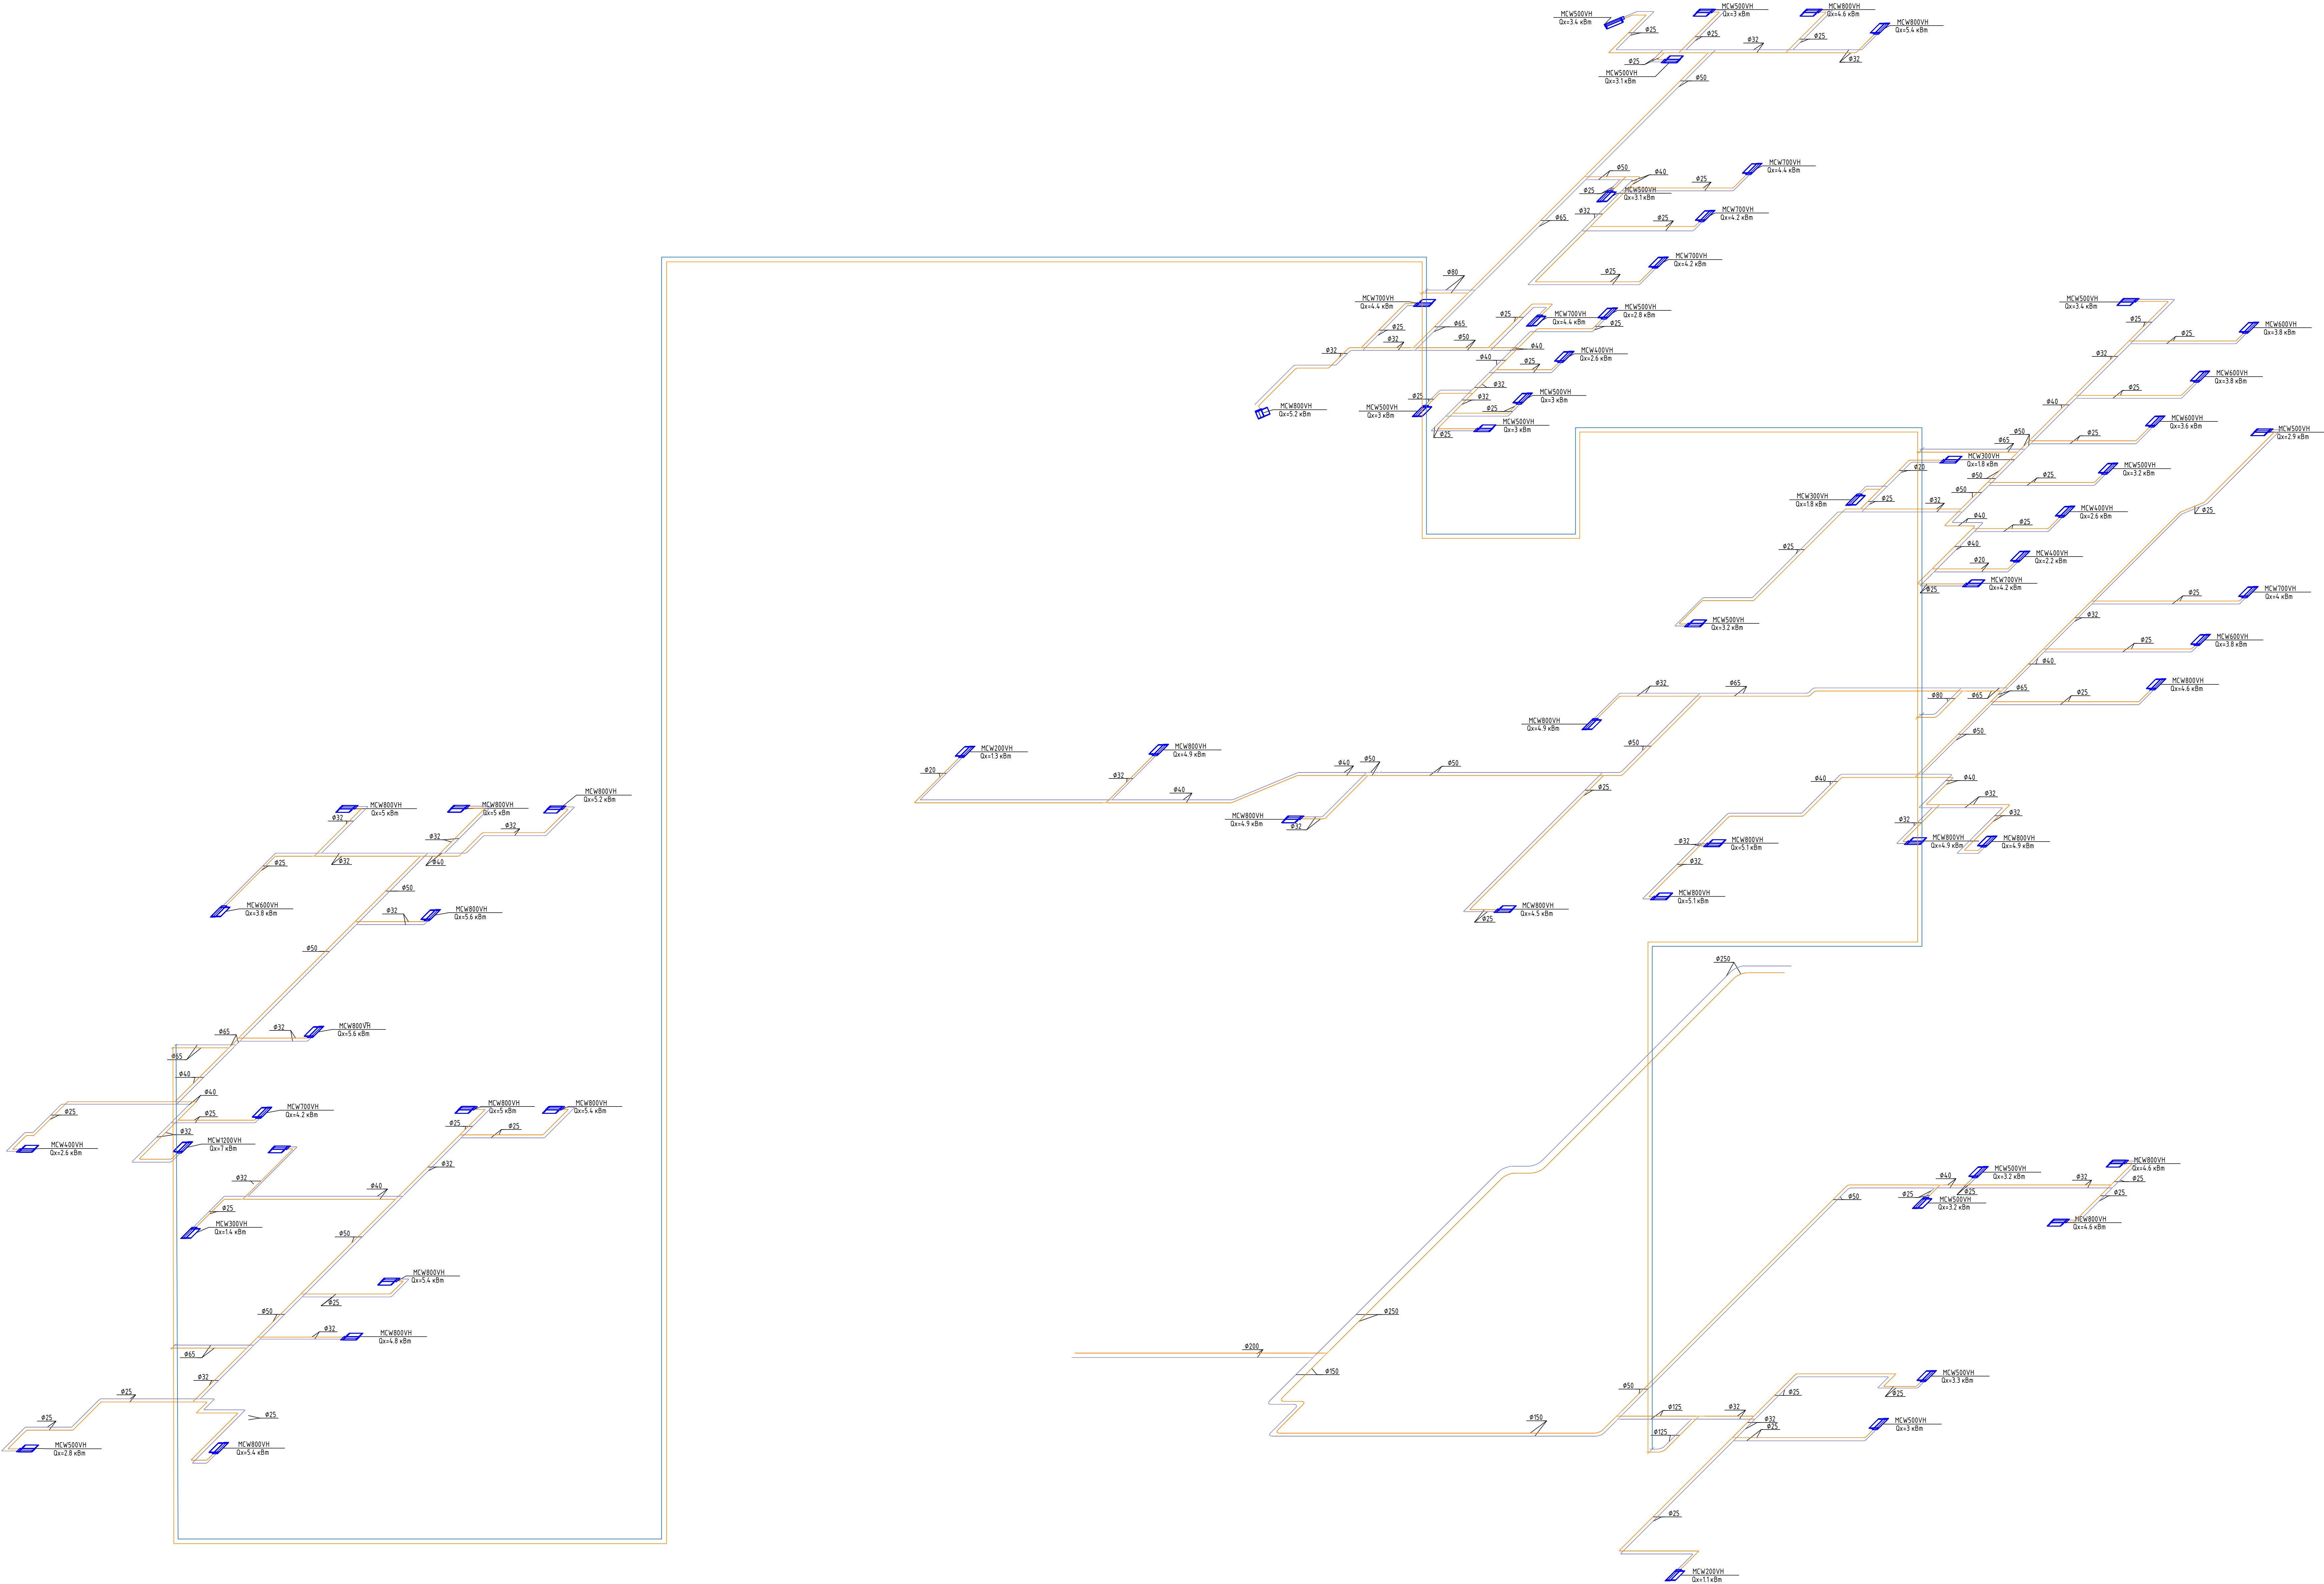

см. совместно с листом -

						-ХС			
						Физкультурно -оздоровительный комплекс с гостиницей город Алтана , район Есиль , ул . Хусейн Ван Талая , жд №25			
Изм.	Кол.	Н.Дан	Лист	Подпись	Дата				
ГМП	Галижанов	С.	02.26			Физкультурно-оздоровительный комплекс			
Пробирка	Галижанов	С.	02.26			(блоки 1, 2, 3, 4)			
Разработчик			02.26						
						Аксонометрия			
						100 "Utility Group"			

Согласовано		
Взам. инв. №		
Подп. и дата		
Инв. № подл.		

Поз.	Наименование и техническая характеристика	Тип, марка, обозначение документа, опросного листа	Код изделия	Поставщик	Ед. изме-ре-ния	Кол-во	Масса 1 ед., кг.	Примечание
	Фильтр сетчатый ф20	РИД-FVR-R			шт	11		
	Фильтр сетчатый ф25	РИД-FVR-R			шт	122		
	Фильтр сетчатый ф32	РИД-FVR-R			шт	75		
	Кран шаровый стальной приварной ф20	LD			шт	22		
	Кран шаровый стальной приварной ф25	LD			шт	251		
	Кран шаровый стальной приварной ф32	LD			шт	150		
	Трубки теплоизоляционные, b=10 мм для ф20				м	80.4		
	Трубки теплоизоляционные, b=10 мм для ф25				м	1126.9		
	Трубки теплоизоляционные, b=10 мм для ф32				м	872.3		
	Трубки теплоизоляционные, b=10 мм для ф40				м	290.8		
	Трубки теплоизоляционные, b=10 мм для ф50				м	348.8		
	Трубки теплоизоляционные, b=10 мм для ф65				м	250.3		
	Трубки теплоизоляционные, b=10 мм для ф80				м	52.4		
	Трубки теплоизоляционные, b=10 мм для ф100				м	110.3		
	Трубки теплоизоляционные, b=10 мм для ф125				м	153.7		
	Трубки теплоизоляционные, b=10 мм для ф150				м	121.4		
	Трубки теплоизоляционные, b=10 мм для ф200				м	42.3		
	Трубки теплоизоляционные, b=10 мм для ф250				м	53.7		
	Крепление труб				кг	1922.9		

						ХС.С				
						Реабилитационно-диагностический центр с гостиницей, расположенный по адресу: город Астана, район Есиль, ул. Хусейн бен Талал, зд. №25. (корректировка)				
Изм.	Кол.уч.	Лист	№ док.	Подп.	Дата	Блоки 1, 2, 3, 4		Стадия	Лист	Листов
								РП	2	
						Спека 2				